

555 JOHNSON

SCOPE:

SHEET INDEX

A000	TITLE SHEET
A001	BUILDING STATISTICS
A002	BUILDING CODE ANALYSIS
A101	SITE PLAN
A210	GROUND FLOOR PLAN
A220	SECOND FLOOR PLAN
A230	THIRD FLOOR PLAN
A240	FOURTH FLOOR PLAN
A250	ROOF DECK PLAN
A310	EXTERIOR ELEVATIONS
A311	EXTERIOR ELEVATIONS

PROJECT CONTACTS

BUILDING OWNER:
EBC CAPITAL

ARCHITECTS:
SCOTT SULLIVAN (C-33139)
RELATIVITY ARCHITECTS
1145 N MCCADDEN PLACE,
LOS ANGELES, CA 90038
310.573.4300
scott@relativityarchitects.com

MEP ENGINEERING:

STRUCTURAL ENGINEERING:

SURVEYOR:

CIVIL:

LANDSCAPE ARCHITECT:

PROJECT INFO / LEGAL DESCRIPTION

ADDRESS: 555 JOHNSON AVENUE, BROOKLYN, NY 11237

ASSESSOR PARCEL NO.: FA

TRACT:

BLOCK: #2988

LOT: #1, #14, #25, #37, #49

ZONING: M3-1

LOT PARCEL AREA: #1 - 22,800 SQ.FT.
#14 - 32,240 SQ.FT.
#25 - 4,467 SQ.FT.
#37 - 16,400 SQ.FT.
#49 - 7,500 SQ.FT.
TOTAL - 83,407 SQ.FT.

LAND USE: INDUSTRIAL & MANUFACTURING

COMMUNITY DISTRICT: BROOKLYN COMMUNITY DISTRICT 1

CITY COUNCIL DISTRICT: COUNCIL DISTRICT 34

STORIES: 4 + ROOF DECK

FLOOR AREA:

HEIGHT: 70 FT

OCCUPANCY: STAGES - F-1
PARKING GARAGE - S-2
MILLWORK SHOP - F-1
OFFICE - B

CONSTRUCTION TYPE: TYPE III - A


FIRE SPRINKELRS: STAGES - S1
OFFICE - SM

LEGAL DESCRIPTION:

APPLICABLE CODES:

PARKINGS: 63 STALLS
25 STALLS ON STREET

VICINITY MAP: NTS

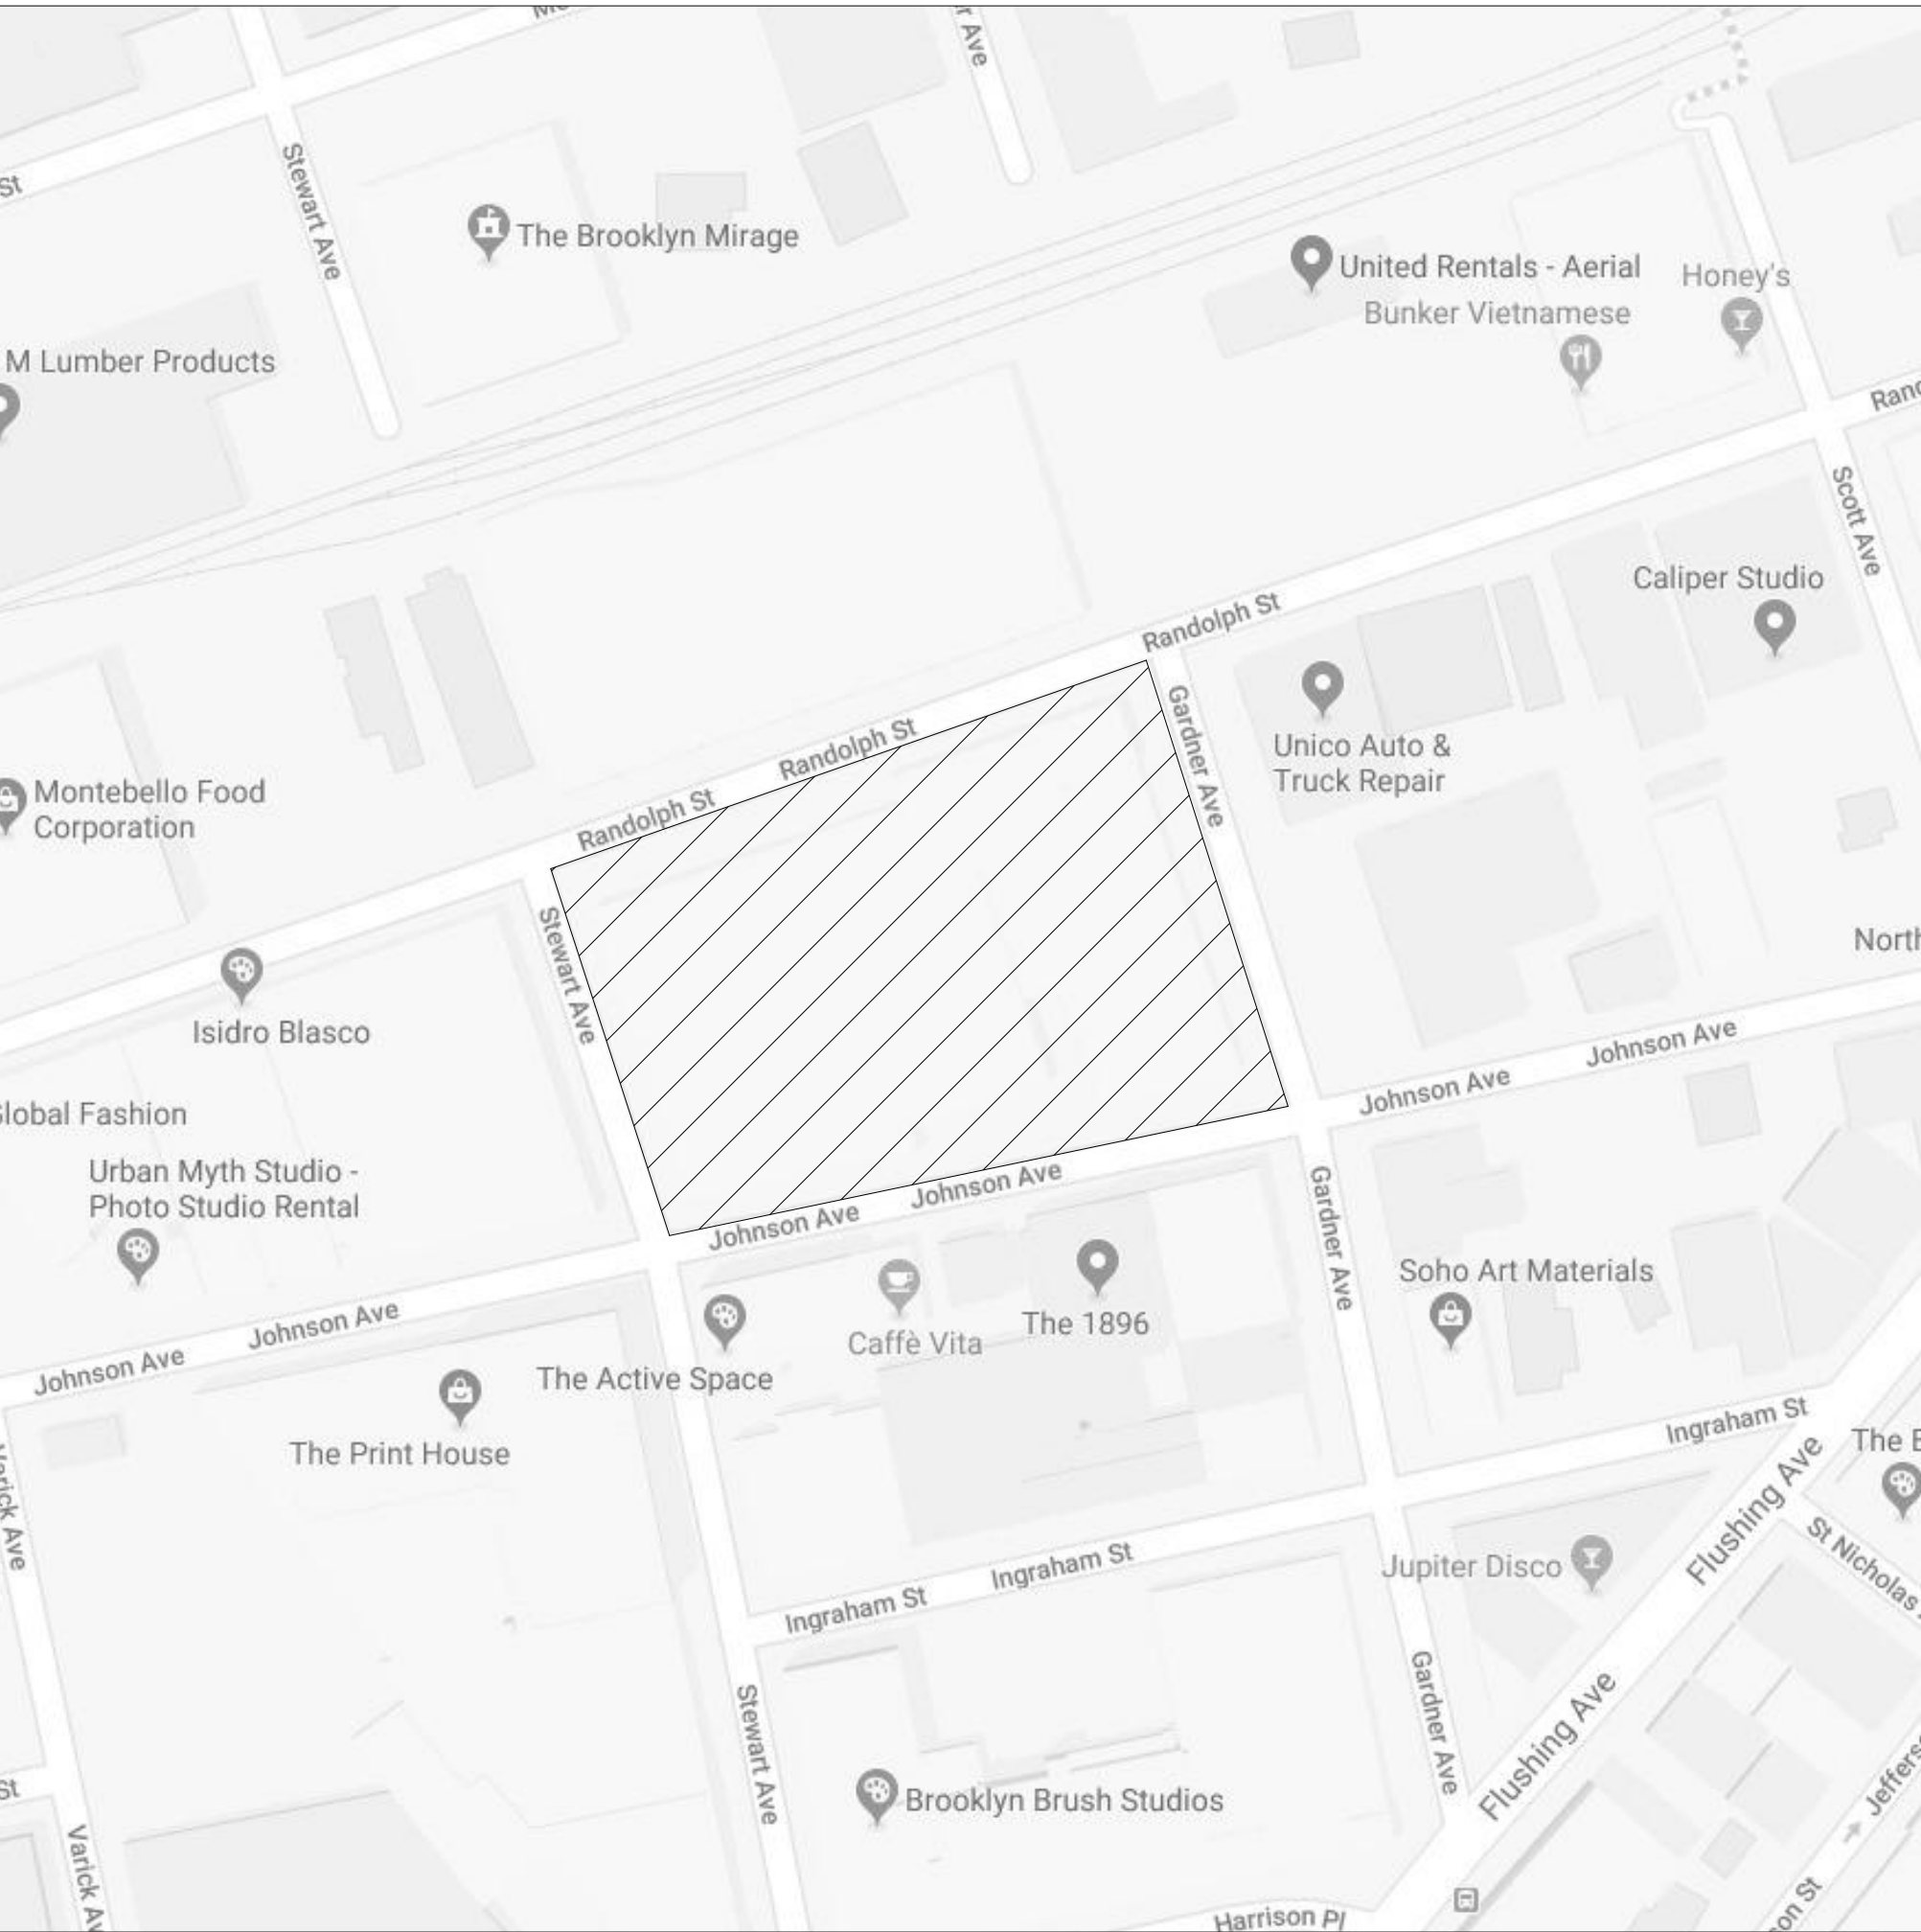


555 JOHNSON
555 JOHNSON AVE
BROOKLYN, NY 11237

TITLE SHEET

DATE	ISSUE	#Project Description
DRAWN BY		
JOB NO.	#Pin	
SCALE		

SHEET
A000

RELATIVITY
ARCHITECTS

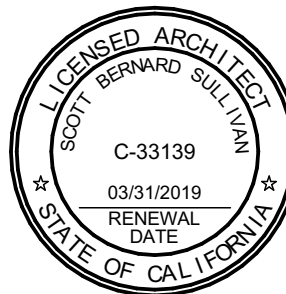

www.relativityarchitects.com
1145 N MCCADDEN PL, LA, CA 90038 P:310.573.4300

P:\19264_555 Johnson\8 Drawings\Working Models\20191207 - 555 Johnson - IS.jen 2019-12-27

BUILDING STATISTICS				
USE GROUPS AND PARKING				
USE GROUPS CLASSIFICATION				
		PARKING REQUIRED:		PROVIDED:
	OFFICES: GROUP 6, PRC-B1	1 PER 600 SF (ZR 73-44)	37,371 SF = 63 STALLS	63 STALLS
	MILLWORK SHOP: GROUP 16, PRC-B1	1 PER 600 SF (ZR 73-44)	6,896 SF = 12 STALLS	0
	MOTION PICTURE PRODUCTION SUTDIOS: GROUP 10A, PRC-D	1 PER 8 PERSONS W/ REDUCTION PER ZR 73-432	589 PERSONS = 74 STALLS	0
		SUM TOTAL OF PARKING PROVIDED:		149 STALLS
		LESS QUANTITY REDUCED BY 44-27:		(40) STALLS
		TOTAL PARKING REQUIRED:		109 STALLS
		STREET PARKING ON SITE:		25 STALLS
		TOTAL PARKING PROVIDED:		88 STALLS
LOADING BERTHS				
		LOADING BERTHS REQUIRED	TOTAL REQUIRED	PROVIDED:
	GROUP 16: 6,896 SF PROPOSED	NONE FOR FIRST 8,000 SF	0	0
	GROUP 10A: 58,811 SF PROPOSED	NONE FOR FIRST 8,000 SF	3 STALLS	4 STALLS
		1 FOR NEXT 17,000 SF		
		1 FOR NEXT 15,000 SF		
		1 FOR NEXT 20,000 SF		
		1 FOR NEXT 40,000 SF		
		0 FOR NEXT 150,000 SF		
	TOTAL LOADING BERTHS PROVIDED:		4 BERTHS	

PLUMBING FIXTURES CALCULATIONS						
REQUIRED						
OCCUPANCY GROUP	WC'S & URINALS - MALE	WATER CLOSETS - FEMALE	LAVATORIES - MALE	LAVATORIES - FEMALE	DRINKING FOUNTAINS	SERVICE SINK
B - FLOOR 1	@ 7.5 OCCUPANTS = 1	@ 7.5 OCCUPANTS = 1	@ 7.5 OCCUPANTS = 1	@ 7.5 OCCUPANTS = 1	1 PER 100 @ 15 OCCUPANTS = 1	1
B - FLOOR 2	NO B-OCCUPANCY ON FLOOR 2					
B - FLOOR 3	@ 91.5 OCCUPANTS = 4	@ 91.5 OCCUPANTS = 4	@ 91.5 OCCUPANTS = 4	@ 91.5 OCCUPANTS = 4	1 PER 100 @ 183 OCCUPANTS = 2	1
B - FLOOR 4	@ 66 OCCUPANTS = 3	@ 66 OCCUPANTS = 3	@ 66 OCCUPANTS = 3	@ 66 OCCUPANTS = 3	1 PER 100 @ 132 OCCUPANTS - 2	1
B - FLOOR 5	@ 73.5 OCCUPANTS = 4	@ 73.5 OCCUPANTS = 4	@ 73.5 OCCUPANTS = 3	@ 73.5 OCCUPANTS = 3	1 PER 100 @ 147 OCCUPANTS = 2	1
F-1 & F-2	1 PER 100 @ 658 OCCUPANTS = 7		1 PER 100 @ 658 OCCUPANTS = 7		1 PER 400 @ 658 OCCUPANTS = 2	1
S-1 & S-2	1 PER 100 @ 18 OCCUPANTS = 1		1 PER 100 @ 18 OCCUPANTS = 1		1 PER 1000 @ 18 OCCUPANTS = 1	1
PROVIDED						
B - FLOOR 1	1	1			1	1
B - FLOOR 2	NO B-OCCUPANCY ON FLOOR 2					
B - FLOOR 3	4	4	4	4	2	1
B - FLOOR 4	5	5	3	3	2	1
B - FLOOR 5	4	4	3	3	2	1
F-1 & F-2	8		8		2	1
S-1 & S-2	1		1		1	1

ROOM NUMBER	ROOM NAME	NET AREA (SQFT)	OCCUPANCY CLASSIFICATION	OCCUPANT LOAD	OCCUPANTS	EXIT REQUIRED	EXIT PROVIDED
100	STAGE #1	29,753	F-2	1/100	298	2	2
101	STAGE #2	29,058	F-2	1/100	291	2	2
102	MAIN LOBBY	1,071	B	1/100	11	1	2
103	GROUND FLOOR PAKRING	7,819	S-2	1/200	40	1	2
104	GOLD ROOM & STORAGE	3,790	S-1	1/300	13	1	2
105	MECHANICAL ROOM	1,304	Undefined	N/A	N/A	N/A	1
106	MILLWORK SHOP	6,896	F-1	1/100	69	1	2
107	LOBBY	322	B	1/100	4	1	2
200	SECOND FLOOR PARKING	22,519	S-2	1/200	113	2	2
202	UTILITY ROOM	382	Undefined	N/A	N/A	N/A	1
300	CAFETERIA & BAR	1,110	B	1/100	12	1	1
301	SCREENING ROOM #1	897	B	1/100	9	1	2
302	STORAGE	108	S-1	1/300	1	1	1
303	SCREENING ROOM #2	1,208	B	1/100	13	1	2
304	STORAGE	393	S-1	1/300	2	1	1
305	FLEX SPACE	1,046	B	1/100	11	1	1
306	PRODUCTION OFFICE	1,046	B	1/100	11	1	2
307	PRODUCTION OFFICE	1,046	B	1/100	11	1	2
308	FLEX SPACE	1,046	B	1/100	11	1	1
309	OFFICE	1,089	B	1/100	11	1	2
310	MENS BATHROOM	334	Undefined	N/A	N/A	N/A	1
311	WOMENS BATHROOM	472	Undefined	N/A	N/A	N/A	1
312	JANITOR & STORAGE	189	S-1	1/300	1	1	1
313	PHONE BOOTH	155	B	1/100	2	1	1
314	OFFICE	813	B	1/100	9	1	2
315	CONFERENCE ROOM	672	B	1/100	7	1	2
316	CONFERENCE ROOM	687	B	1/100	7	1	2
317	UTILITY ROOM	213	Undefined	N/A	N/A	N/A	1
318	KITCHEN	382	B	1/100	4	1	1
319	LOUNGE	1,185	B	1/100	12	1	2
320	CORRIDOR	2,907	Undefined	N/A	N/A	N/A	N/A
321	DECK	4,515	B	1/100	46	1	2
400	EXECUTIVE OFFICE	300	B	1/100	3	1	1
401	EXECUTIVE OFFICE	210	B	1/100	3	1	1
402	EXECUTIVE OFFICE	251	B	1/100	3	1	1
403	EXECUTIVE OFFICE	233	B	1/100	3	1	1
404	EXECUTIVE OFFICE	233	B	1/100	3	1	1
405	EXECUTIVE OFFICE	233	B	1/100	3	1	1
406	EXECUTIVE OFFICE	233	B	1/100	3	1	1
407	EXECUTIVE OFFICE	233	B	1/100	3	1	1
408	EXECUTIVE OFFICE	233	B	1/100	3	1	1
409	EXECUTIVE OFFICE	242	B	1/100	3	1	1
410	EXECUTIVE OFFICE	242	B	1/100	3	1	1
411	MENS BATHROOM	334	Undefined	N/A	N/A	N/A	1
412	WOMENS BATHROOM	472	Undefined	N/A	N/A	N	1
413	JANITOR & STORAGE	189	S-1	1/300	1	1	1
414	PHONE BOOTH	155	B	1/100	2	1	1
415	BULLPEN OFFICE	813	B	1/100	9	1	2
416	CONFERENCE ROOM	672	B	1/100	7		2
417	CONFERENCE ROOM	687	B	1/100	7	1	2
418	UTILITY ROOM	213	Undefined	N/A	N/A	N/A	1
419	KITCHEN	382	B	1/100	4	1	1
420	BULLPEN OFFICE	3,791	B	1/100	38	1	2
421	CORRIDOR	3,558	Undefined	N/A	N/A	N/A	N/A
422	OUTDOOR ROOF DECK	3,154	B	1/100	32	1	2
500	ROOF DECK	14,632	B	1/100	147	2	2
A1-1	STAIR & ELEVATOR CORE	250	Undefined	N/A	N/A	N/A	N/A
A1-2	STAIR & ELEVATOR CORE	250	Undefined	N/A	N/A	N/A	N/A
A1-3	STAIR & ELEVATOR CORE	250	Undefined	N/A	N/A	N/A	N/A
A1-4	STAIR & ELEVATOR CORE	250	Undefined	N/A	N/A	N/A	N/A
A1-5	STAIR & ELEVATOR CORE	250	Undefined	N/A	N/A	N/A	N/A
A2-1	STAIR & ELEVATOR CORE	421	Undefined	N/A	N/A	N/A	N/A
A2-2	STAIR & ELEVATOR CORE	421	Undefined	N/A	N/A	N/A	N/A
A2-3	STAIR & ELEVATOR CORE	421	Undefined	N/A	N/A	N/A	N/A
A2-4	STAIR & ELEVATOR CORE	421	Undefined	N/A	N/A	N/A	N/A
A2-5	STAIR & ELEVATOR CORE	421	Undefined	N/A	N/A	N/A	N/A

BUILDING AREAS

TOTAL NET FLOOR AREA - STAGES:	58,811 SQ.FT.
TOTAL NET FLOOR AREA - MILLWORK SHOP:	6,896 SQ.FT.
TOTAL NET FLOOR AREA - OFFICE:	37,371 SQ.FT.

TOTAL NET FLOOR AREA (EXCLUDED DECK & GARAGE): 103,078 SQFT

TOTAL NET FLOOR AREA - PARKING GARAGE: (LESS THAN 23' ABOVE CURB)	30,338 SQ.FT.
TOTAL NET FLOOR AREA - DECK:	22,301 SQ.FT.


BUILDING STATISTICS

DATE	ISSUE	#Project Description

DRAWN BY	#Pin
JOB NO.	
SCALE	1' = 1'-0", 1:0.77, 1:0.95

SHEET


A001

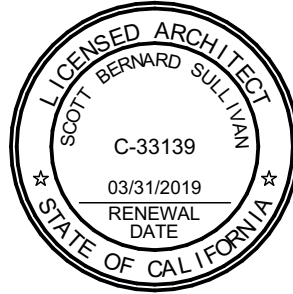

555 JOHNSON
555 JOHNSON AVE
BROOKLYN, NY 11237


RELATIVITY
ARCHITECTS

www.relativityarchitects.com
1145 N MCCADDEN PL, LA, CA 90038 P:310.573.4300

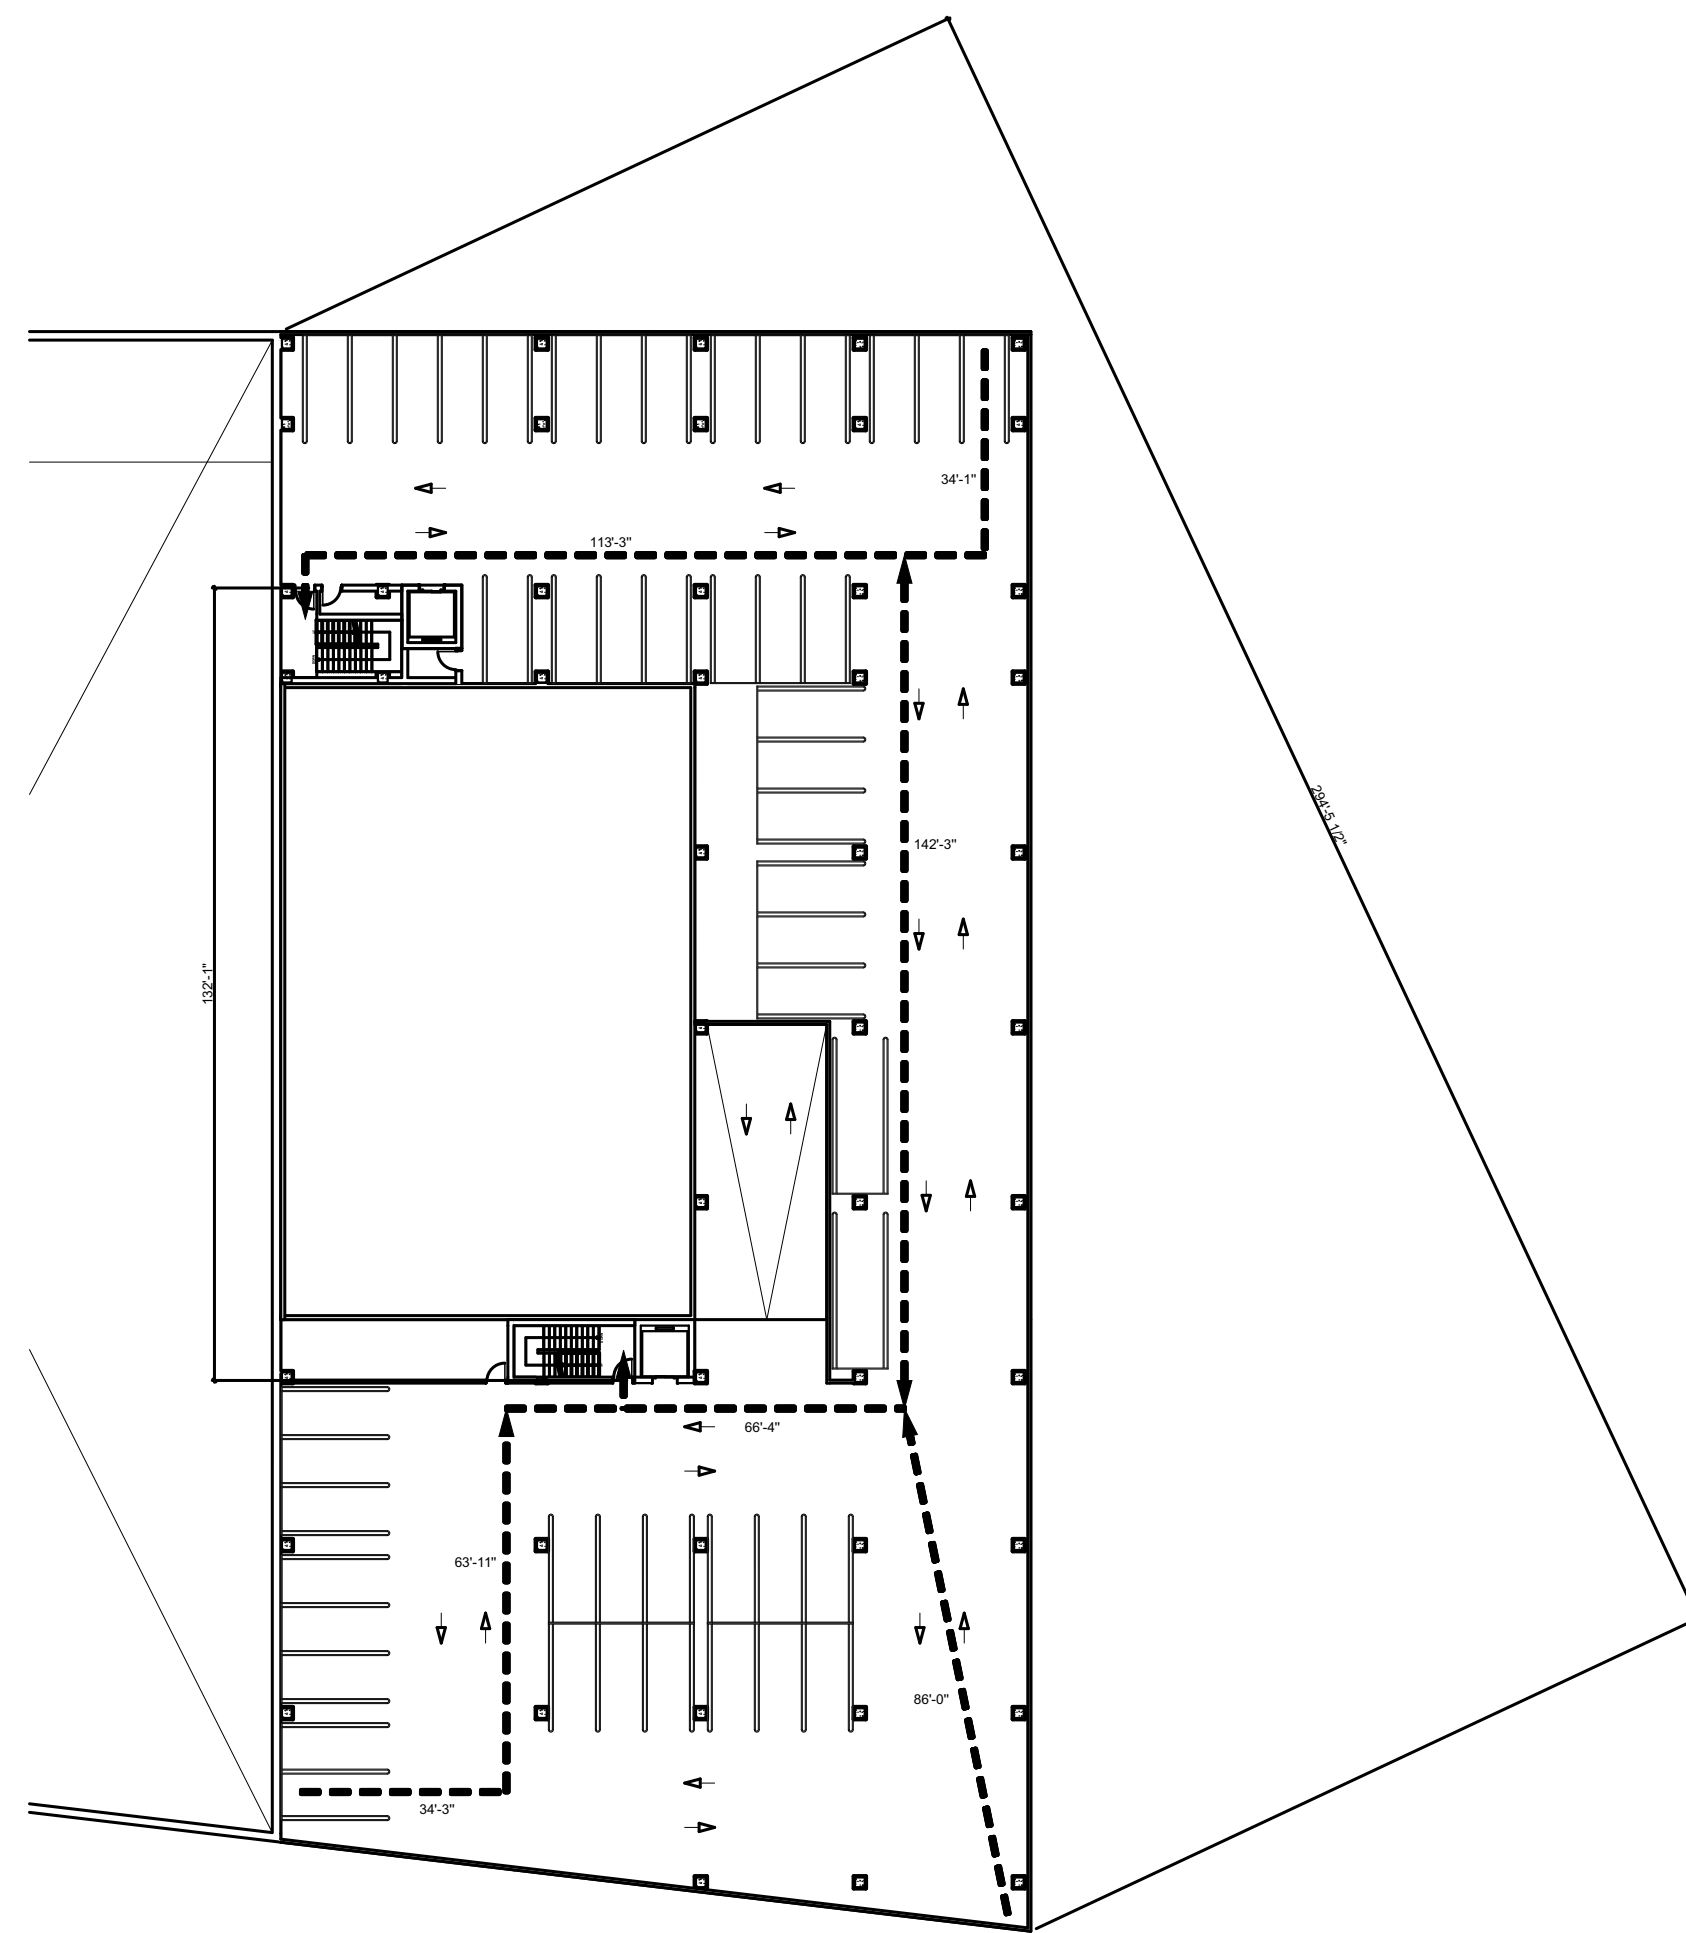


SECOND FLOOR EGRESS PLAN

SCALE: 1/32" = 1'-0"

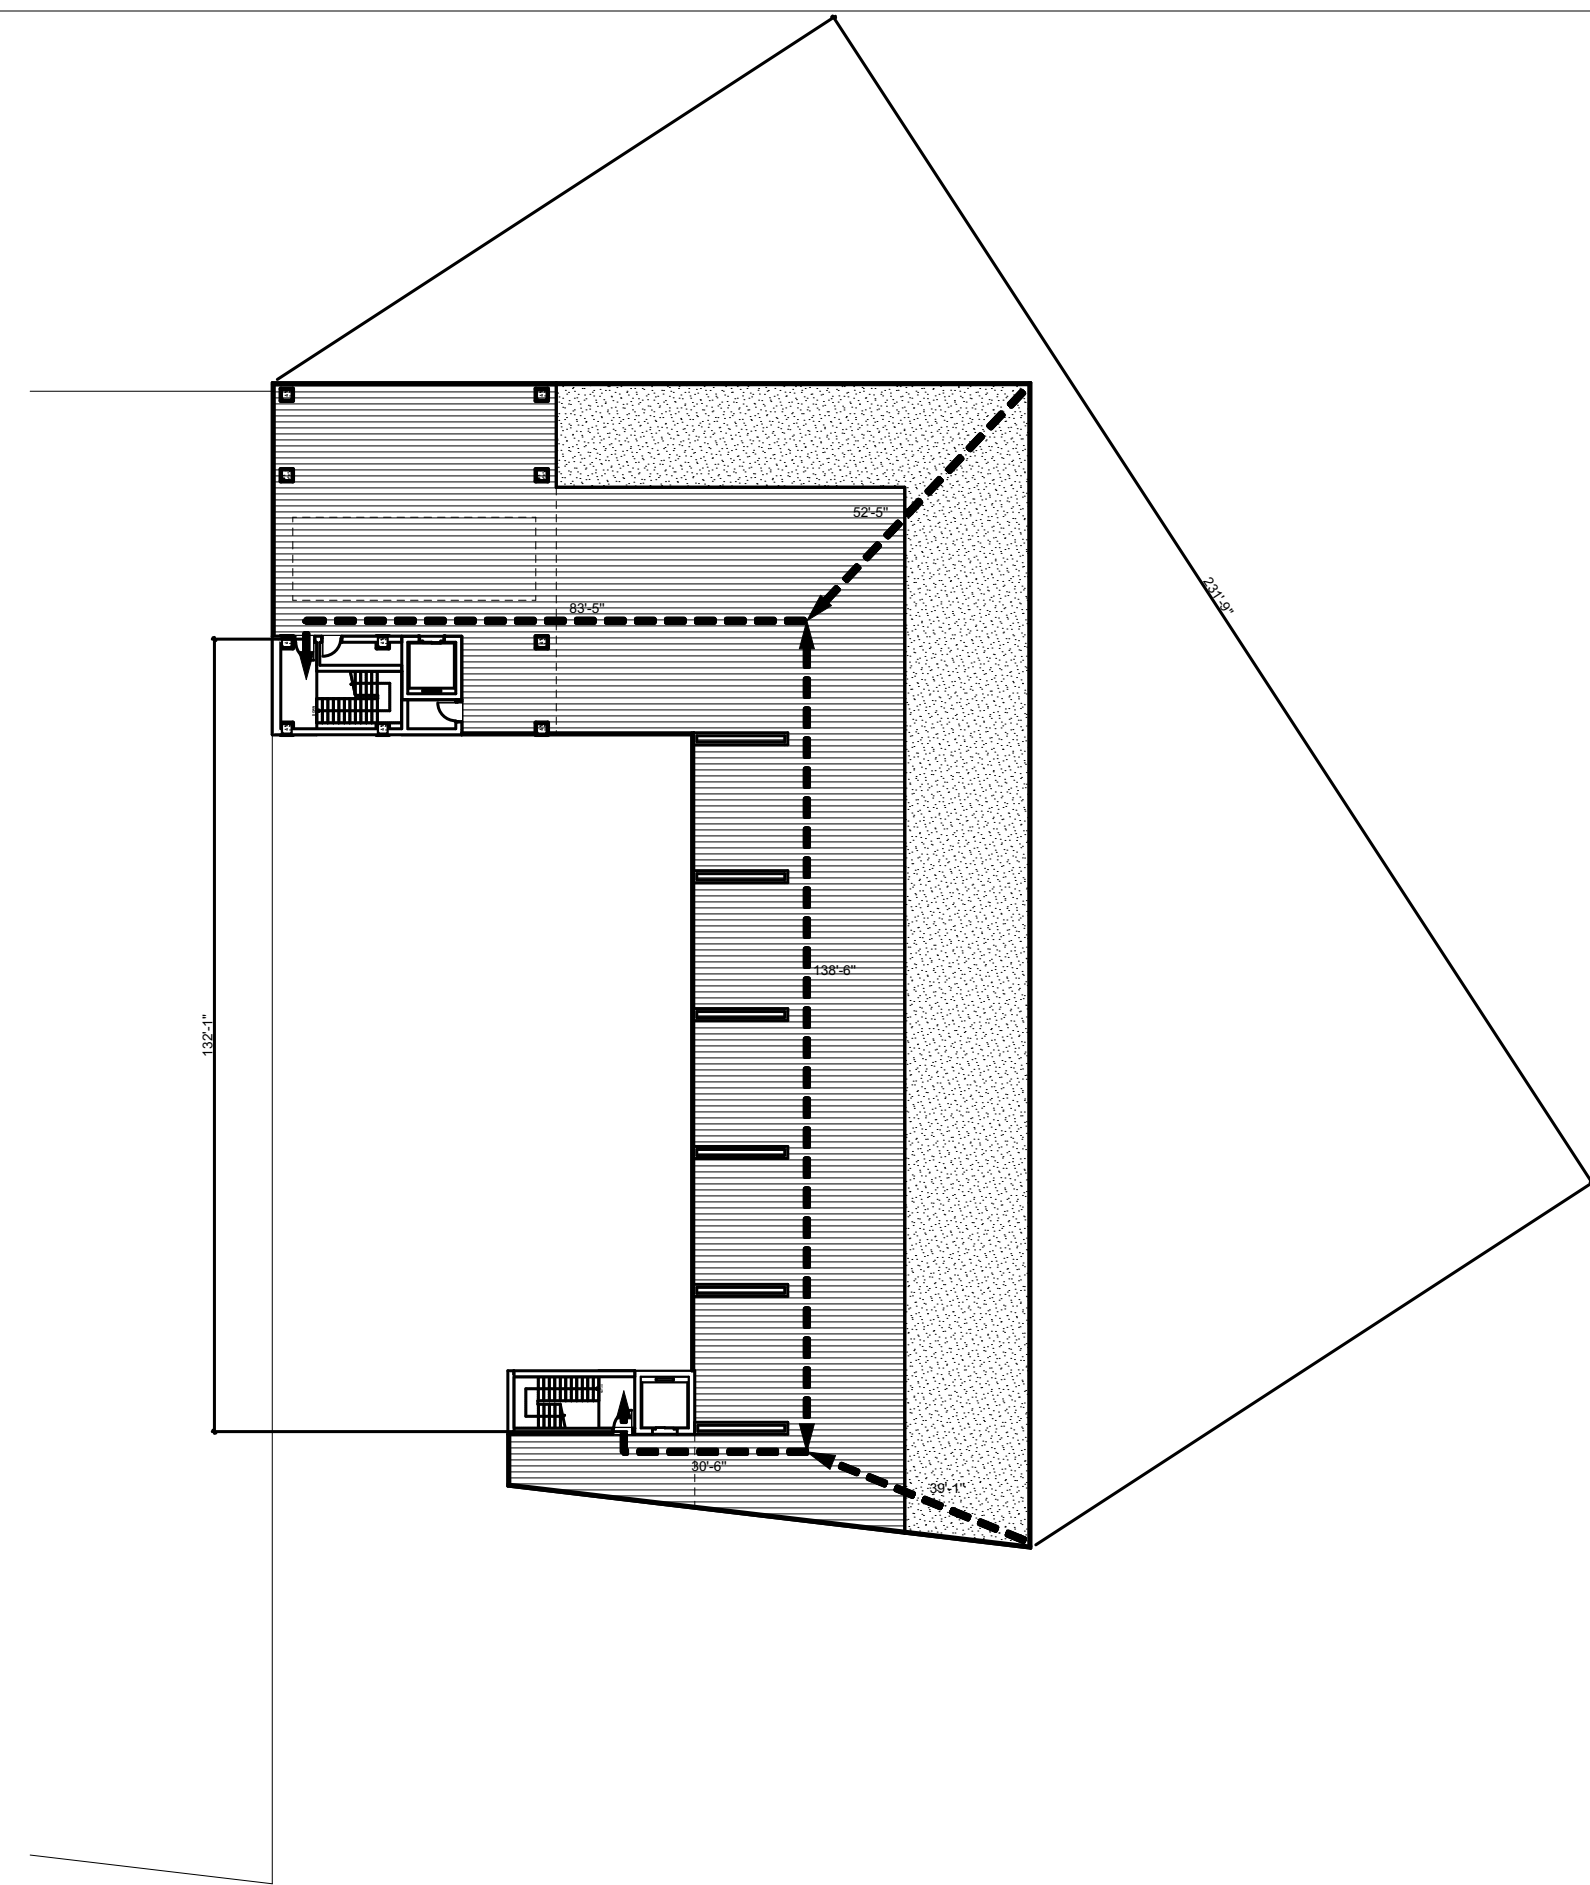


ROOF DECK EGRESS PLAN

SCALE: 1/32" = 1'-0"

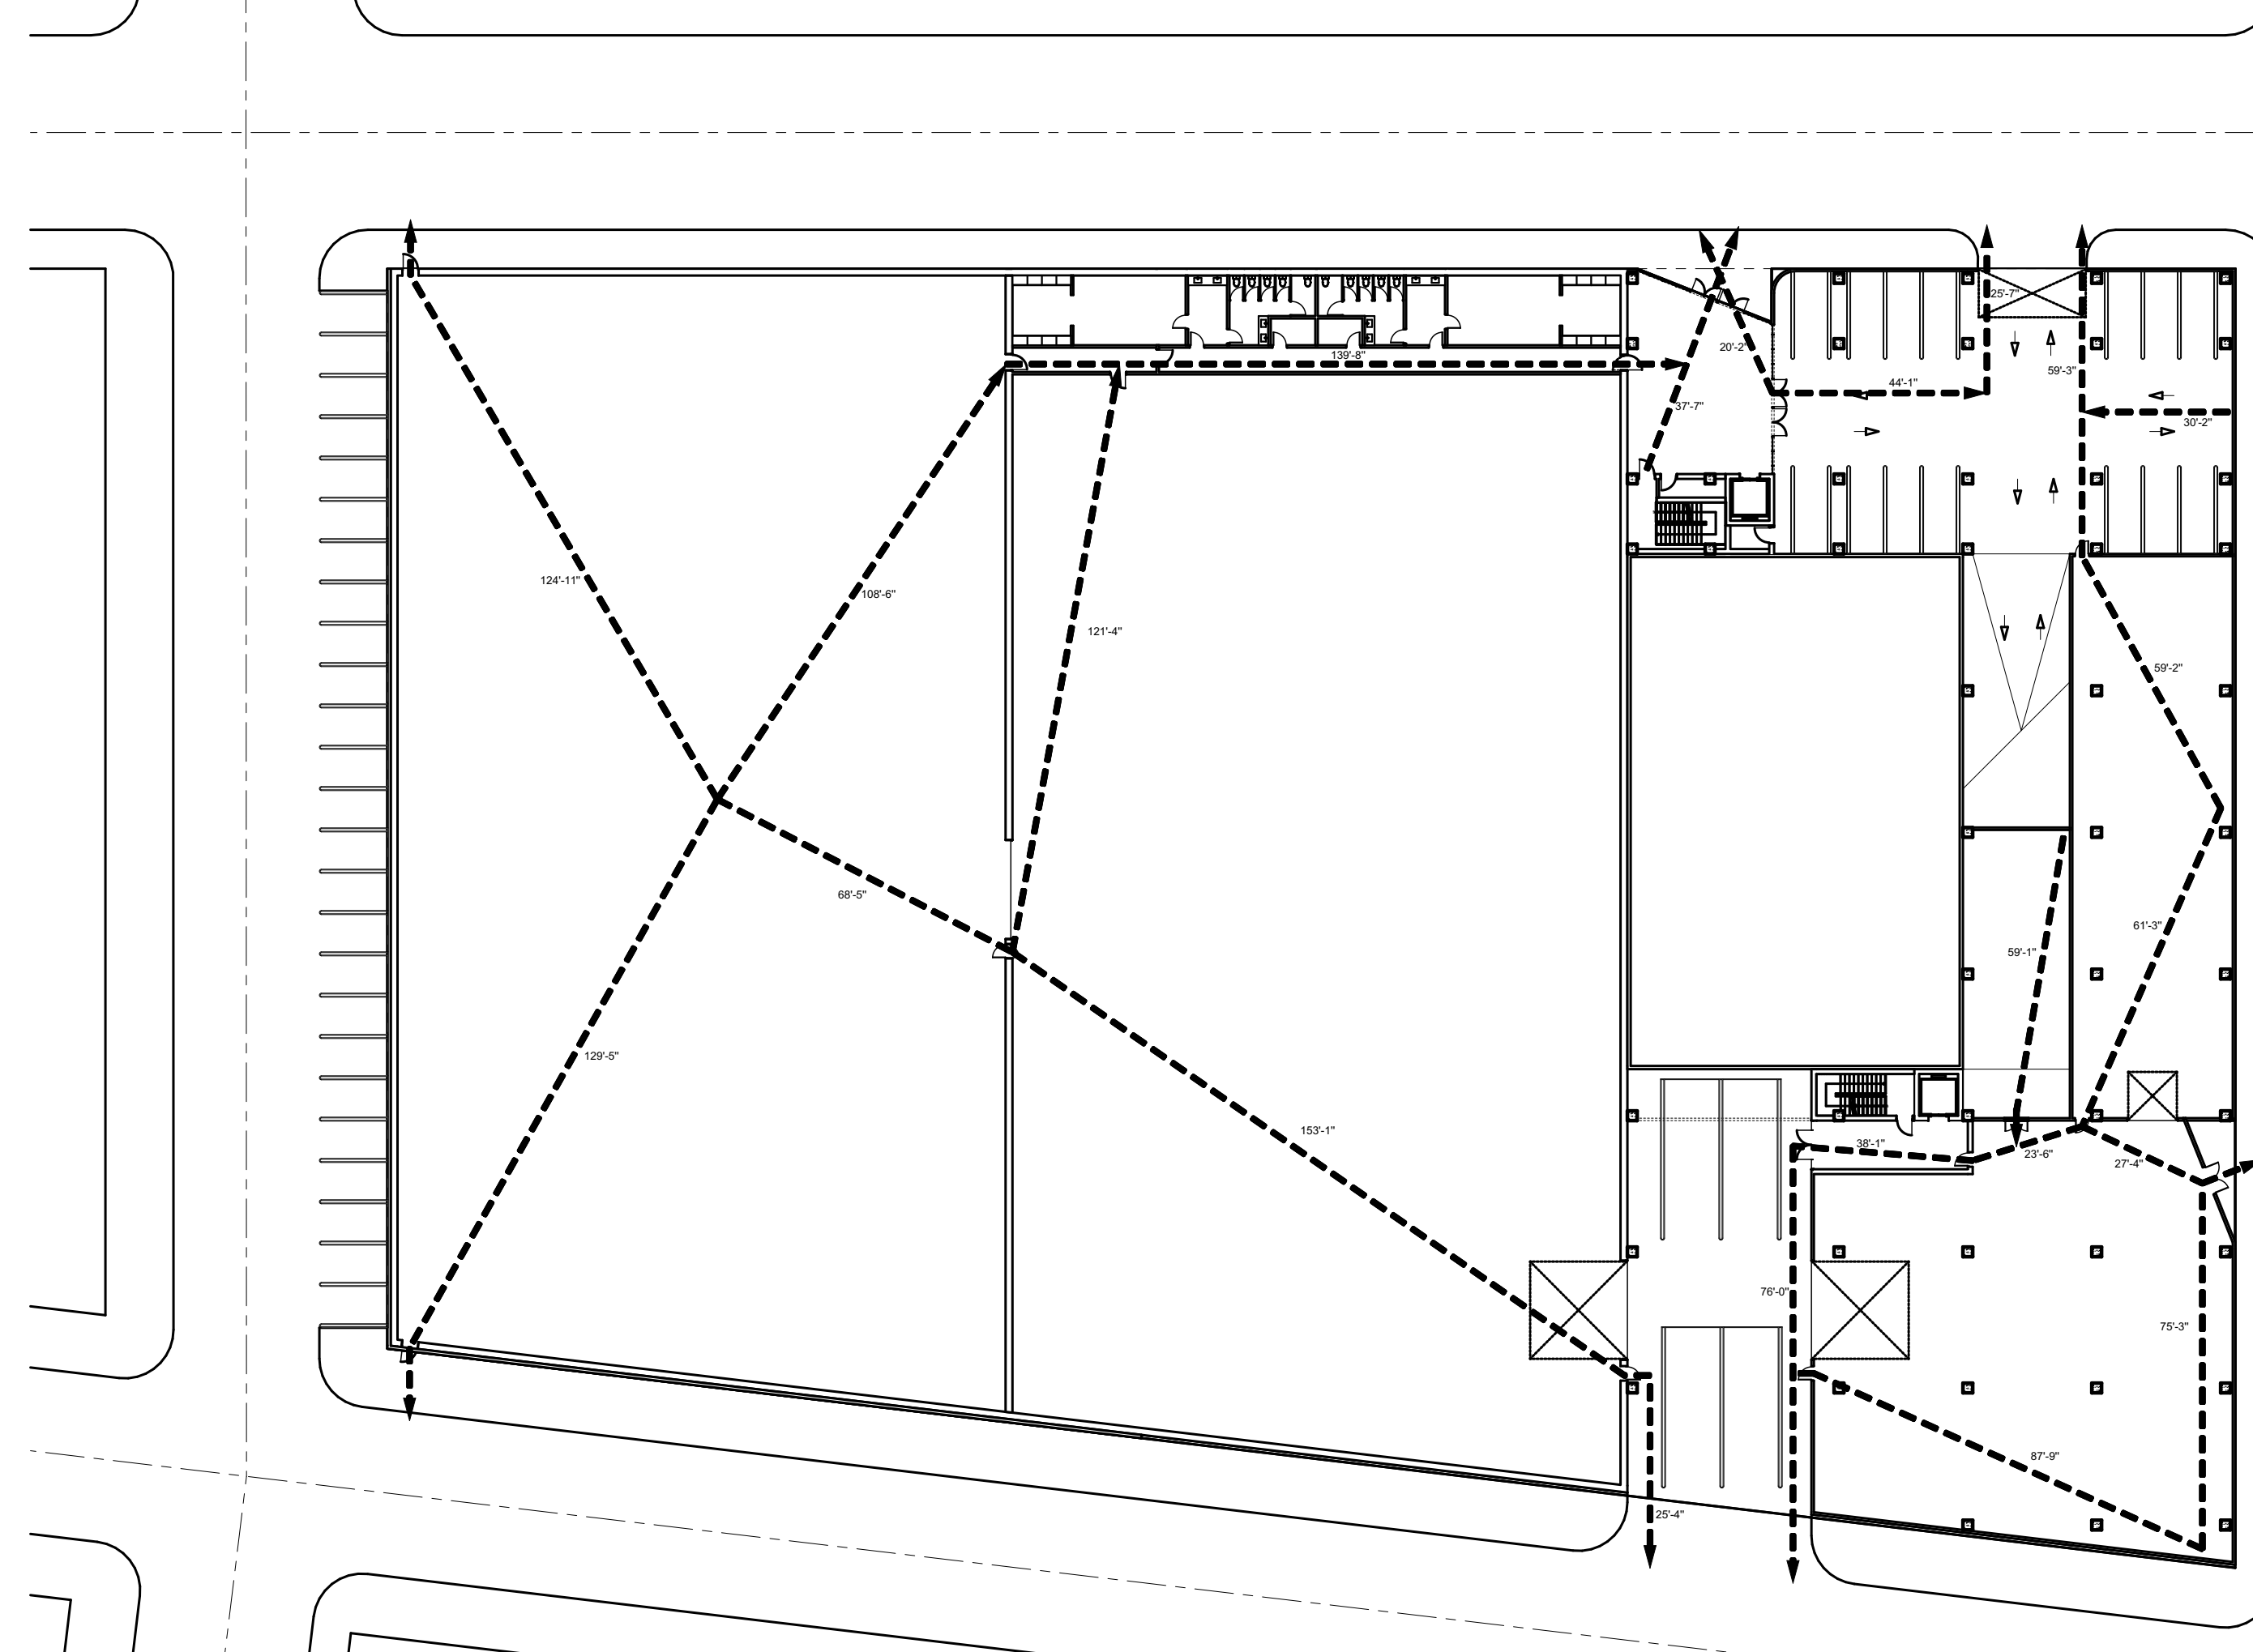


FIRST FLOOR EGRESS PLAN

SCALE: 1/32" = 1'-0"

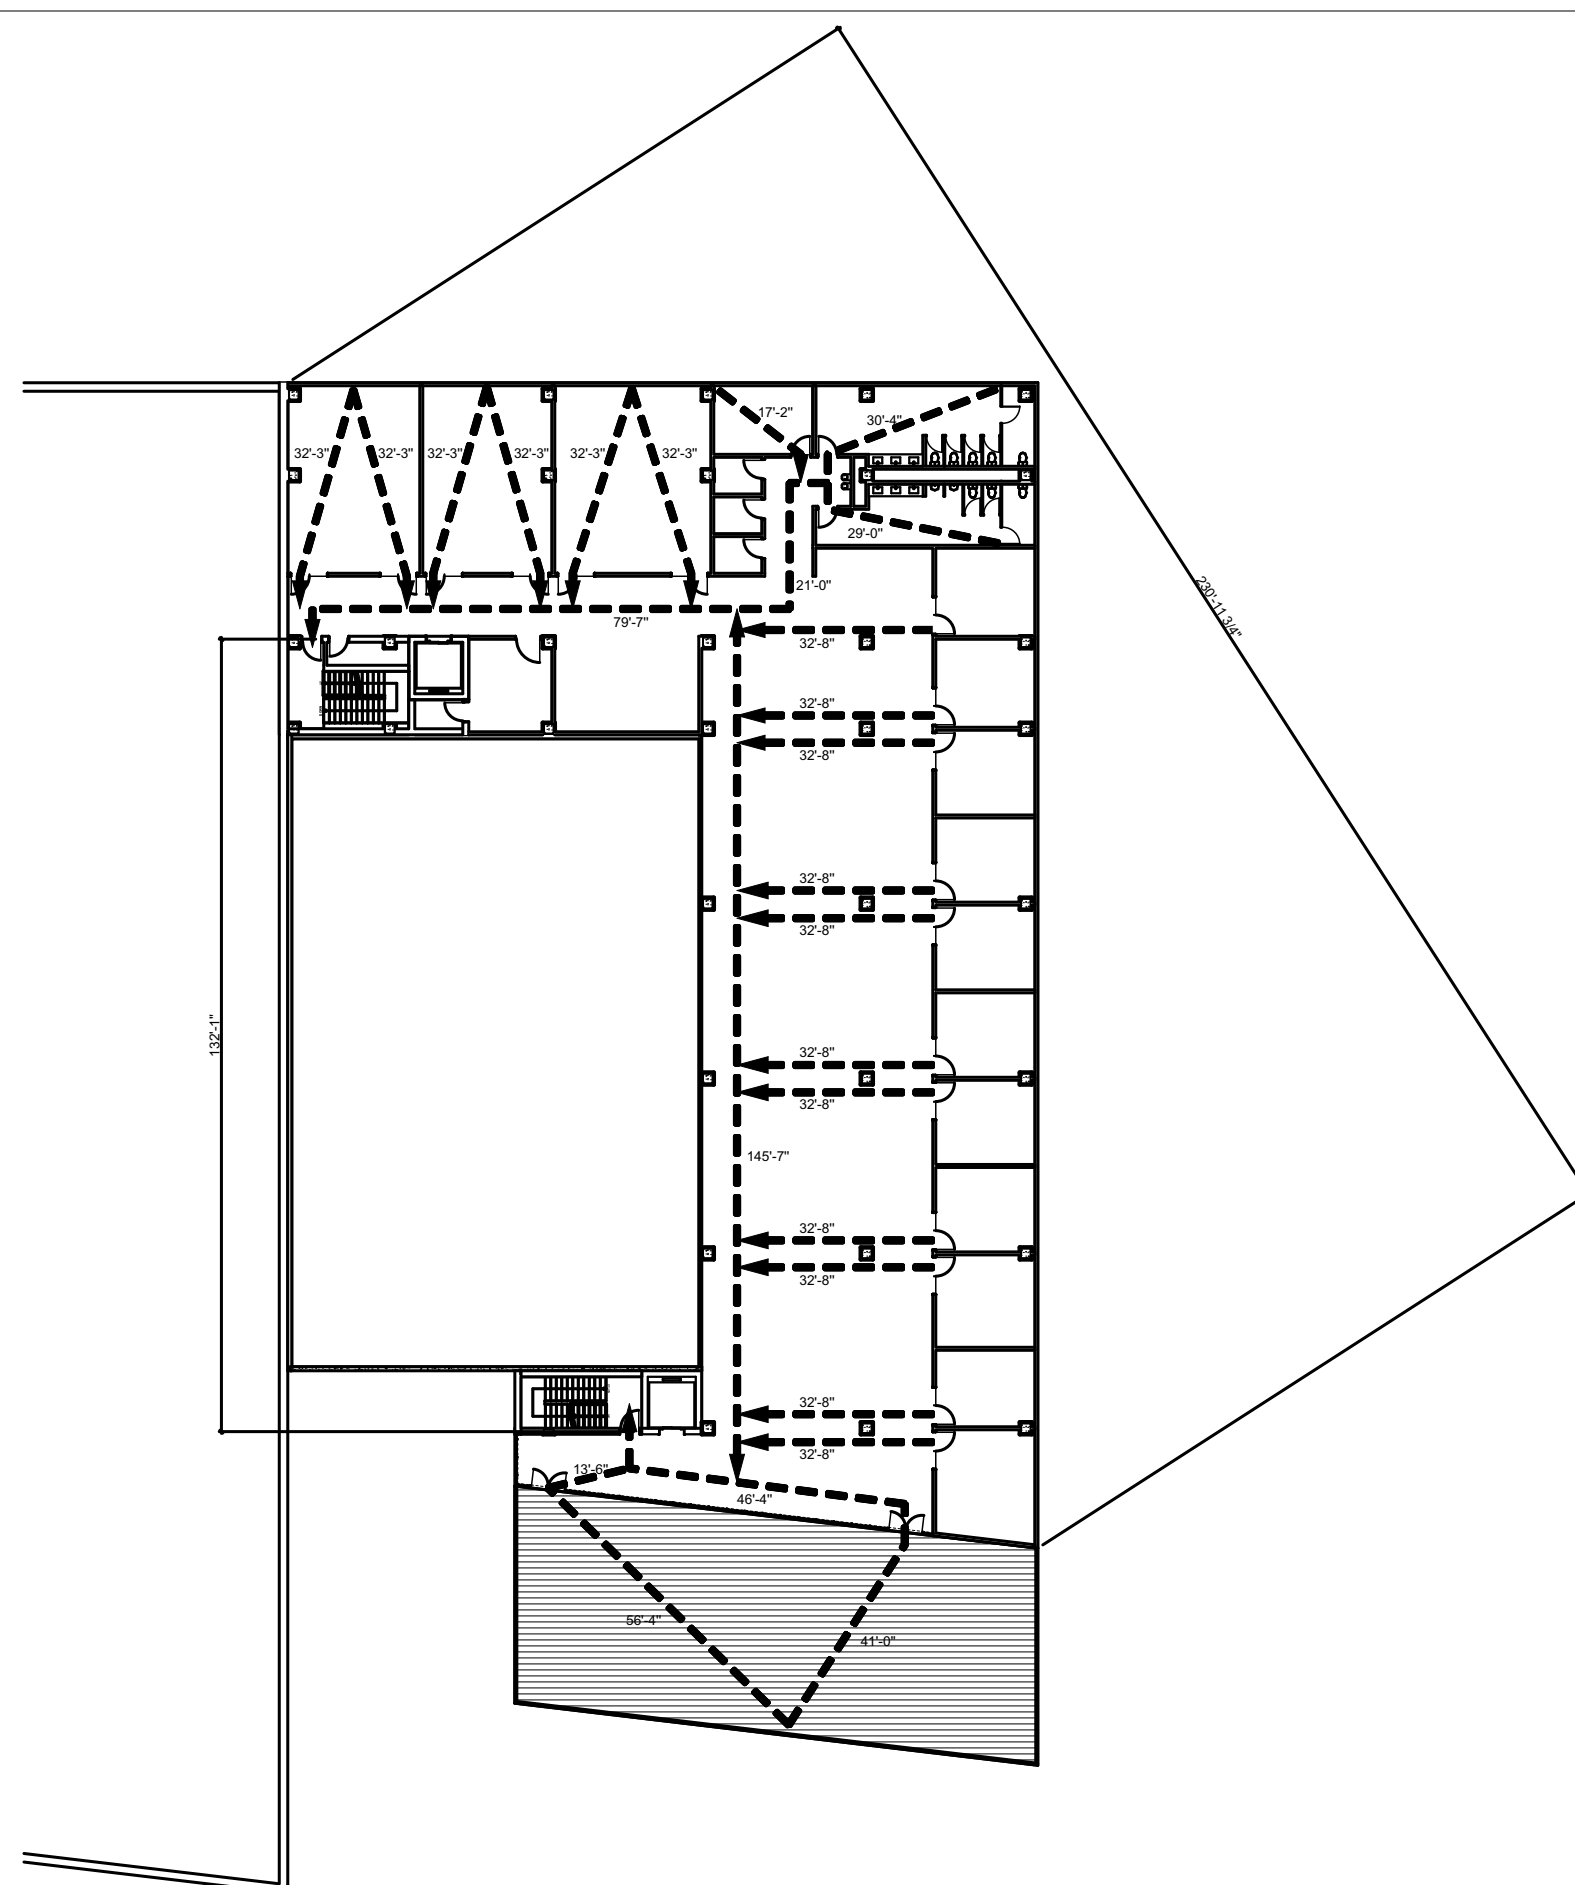

FOURTH FLOOR EGRESS PLAN

SCALE: 1/32" = 1'-0"

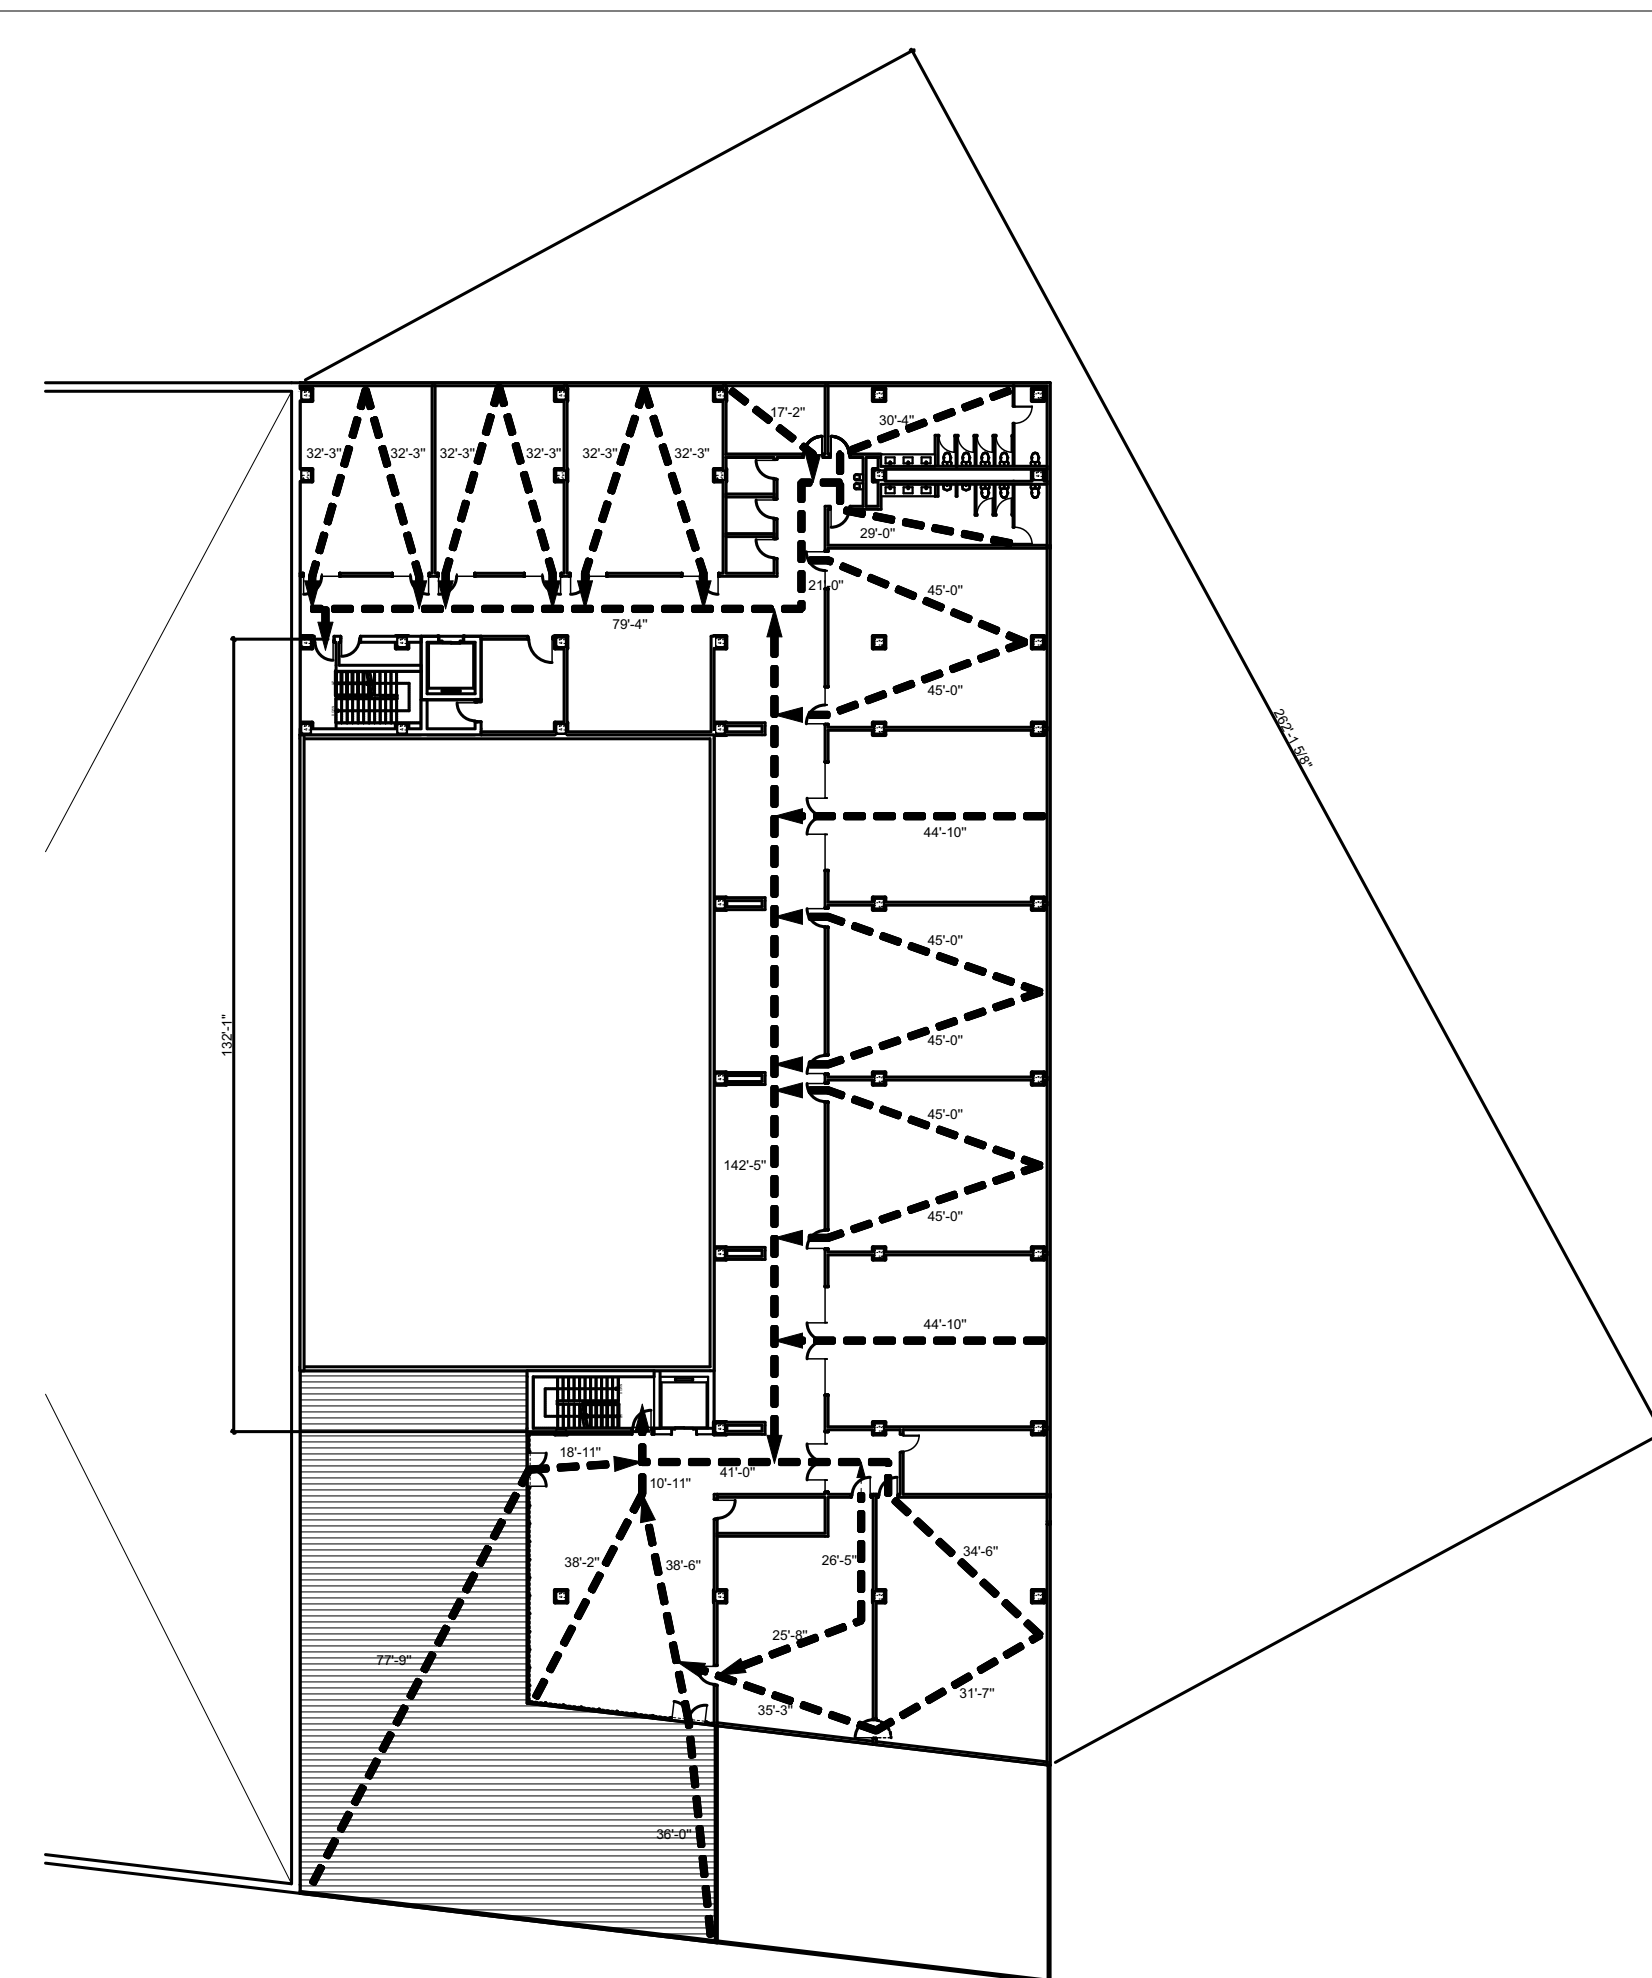

THIRD FLOOR EGRESS PLAN

SCALE: 1/32" = 1'-0"



BUILDING CODE ANALYSIS

DRAWN
BY

JOB
NO.

SCALE

JOB
NO.

SCALE

DATE	ISSUE
------	-------

UE


#Project Description

#Pin

$$1/32'' = 1'-0''$$


555 JOHNSON

555 JOHNSON AVE
BROOKLYN, NY 11237

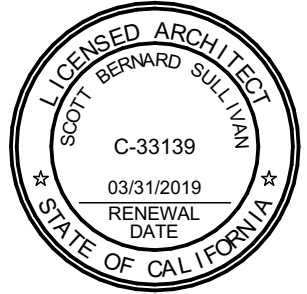

www.relativityarchitects.com
1145 N MCCADDEN PL, LA, CA 90038 P:310.573.4300

P:\1926A_555 Johnson\8 Drawings\Working Models\20191207 - 555 Johnson - JS.rvt 2019-12-07

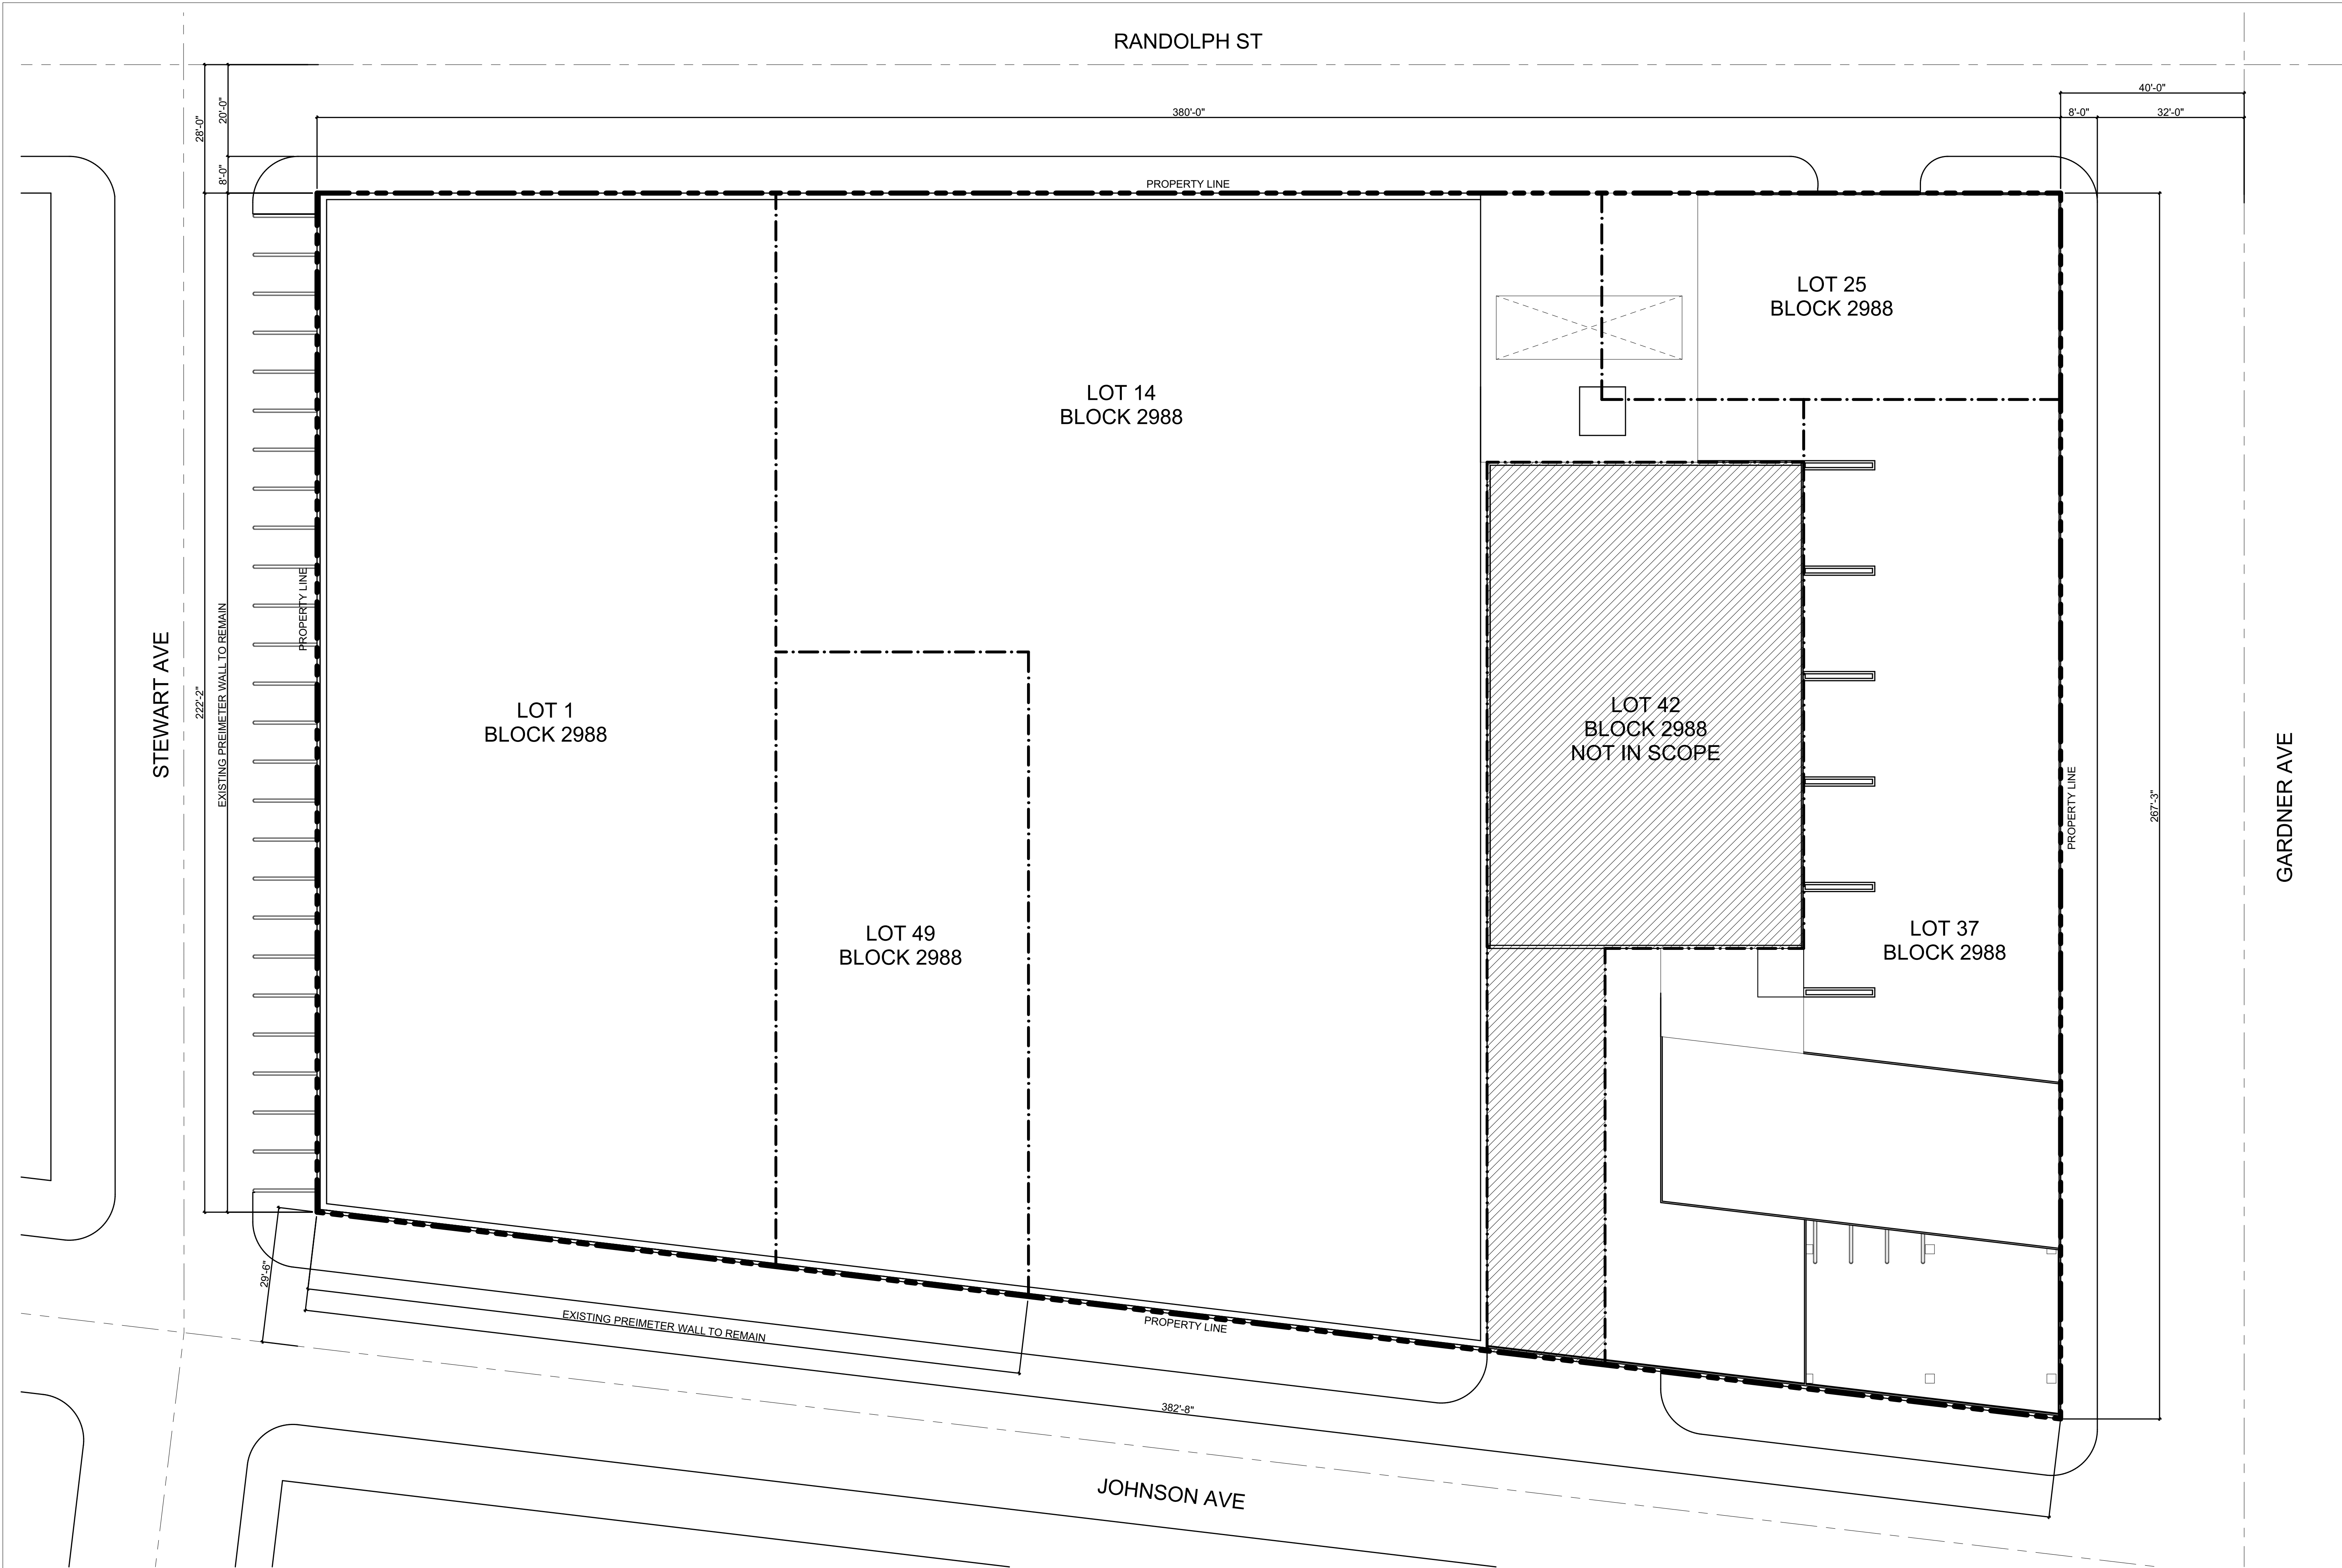


Site Plan
SCALE: 1/16" = 1'-0"

1

SITE PLAN		
DRAWN BY	DATE	ISSUE
JOB NO.		#Project Description
SCALE	1/16" = 1'-0"	#Pin

555 JOHNSON
555 JOHNSON AVE
BROOKLYN, NY 11237

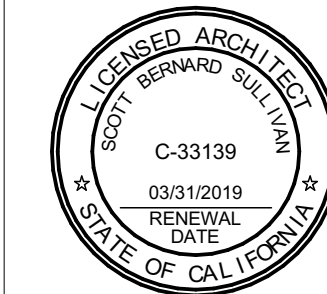


RELATIVITY
ARCHITECTS

www.relativityarchitects.com
1145 N MCCADDEN PL, LA, CA 90038 P:310.573.4300

P:\1926A_555 Johnson\8 Drawings\Working Models\20191207 - 555 Johnson - JS.rvt 2019-12-27

STEWART AVE

RANDOLPH ST

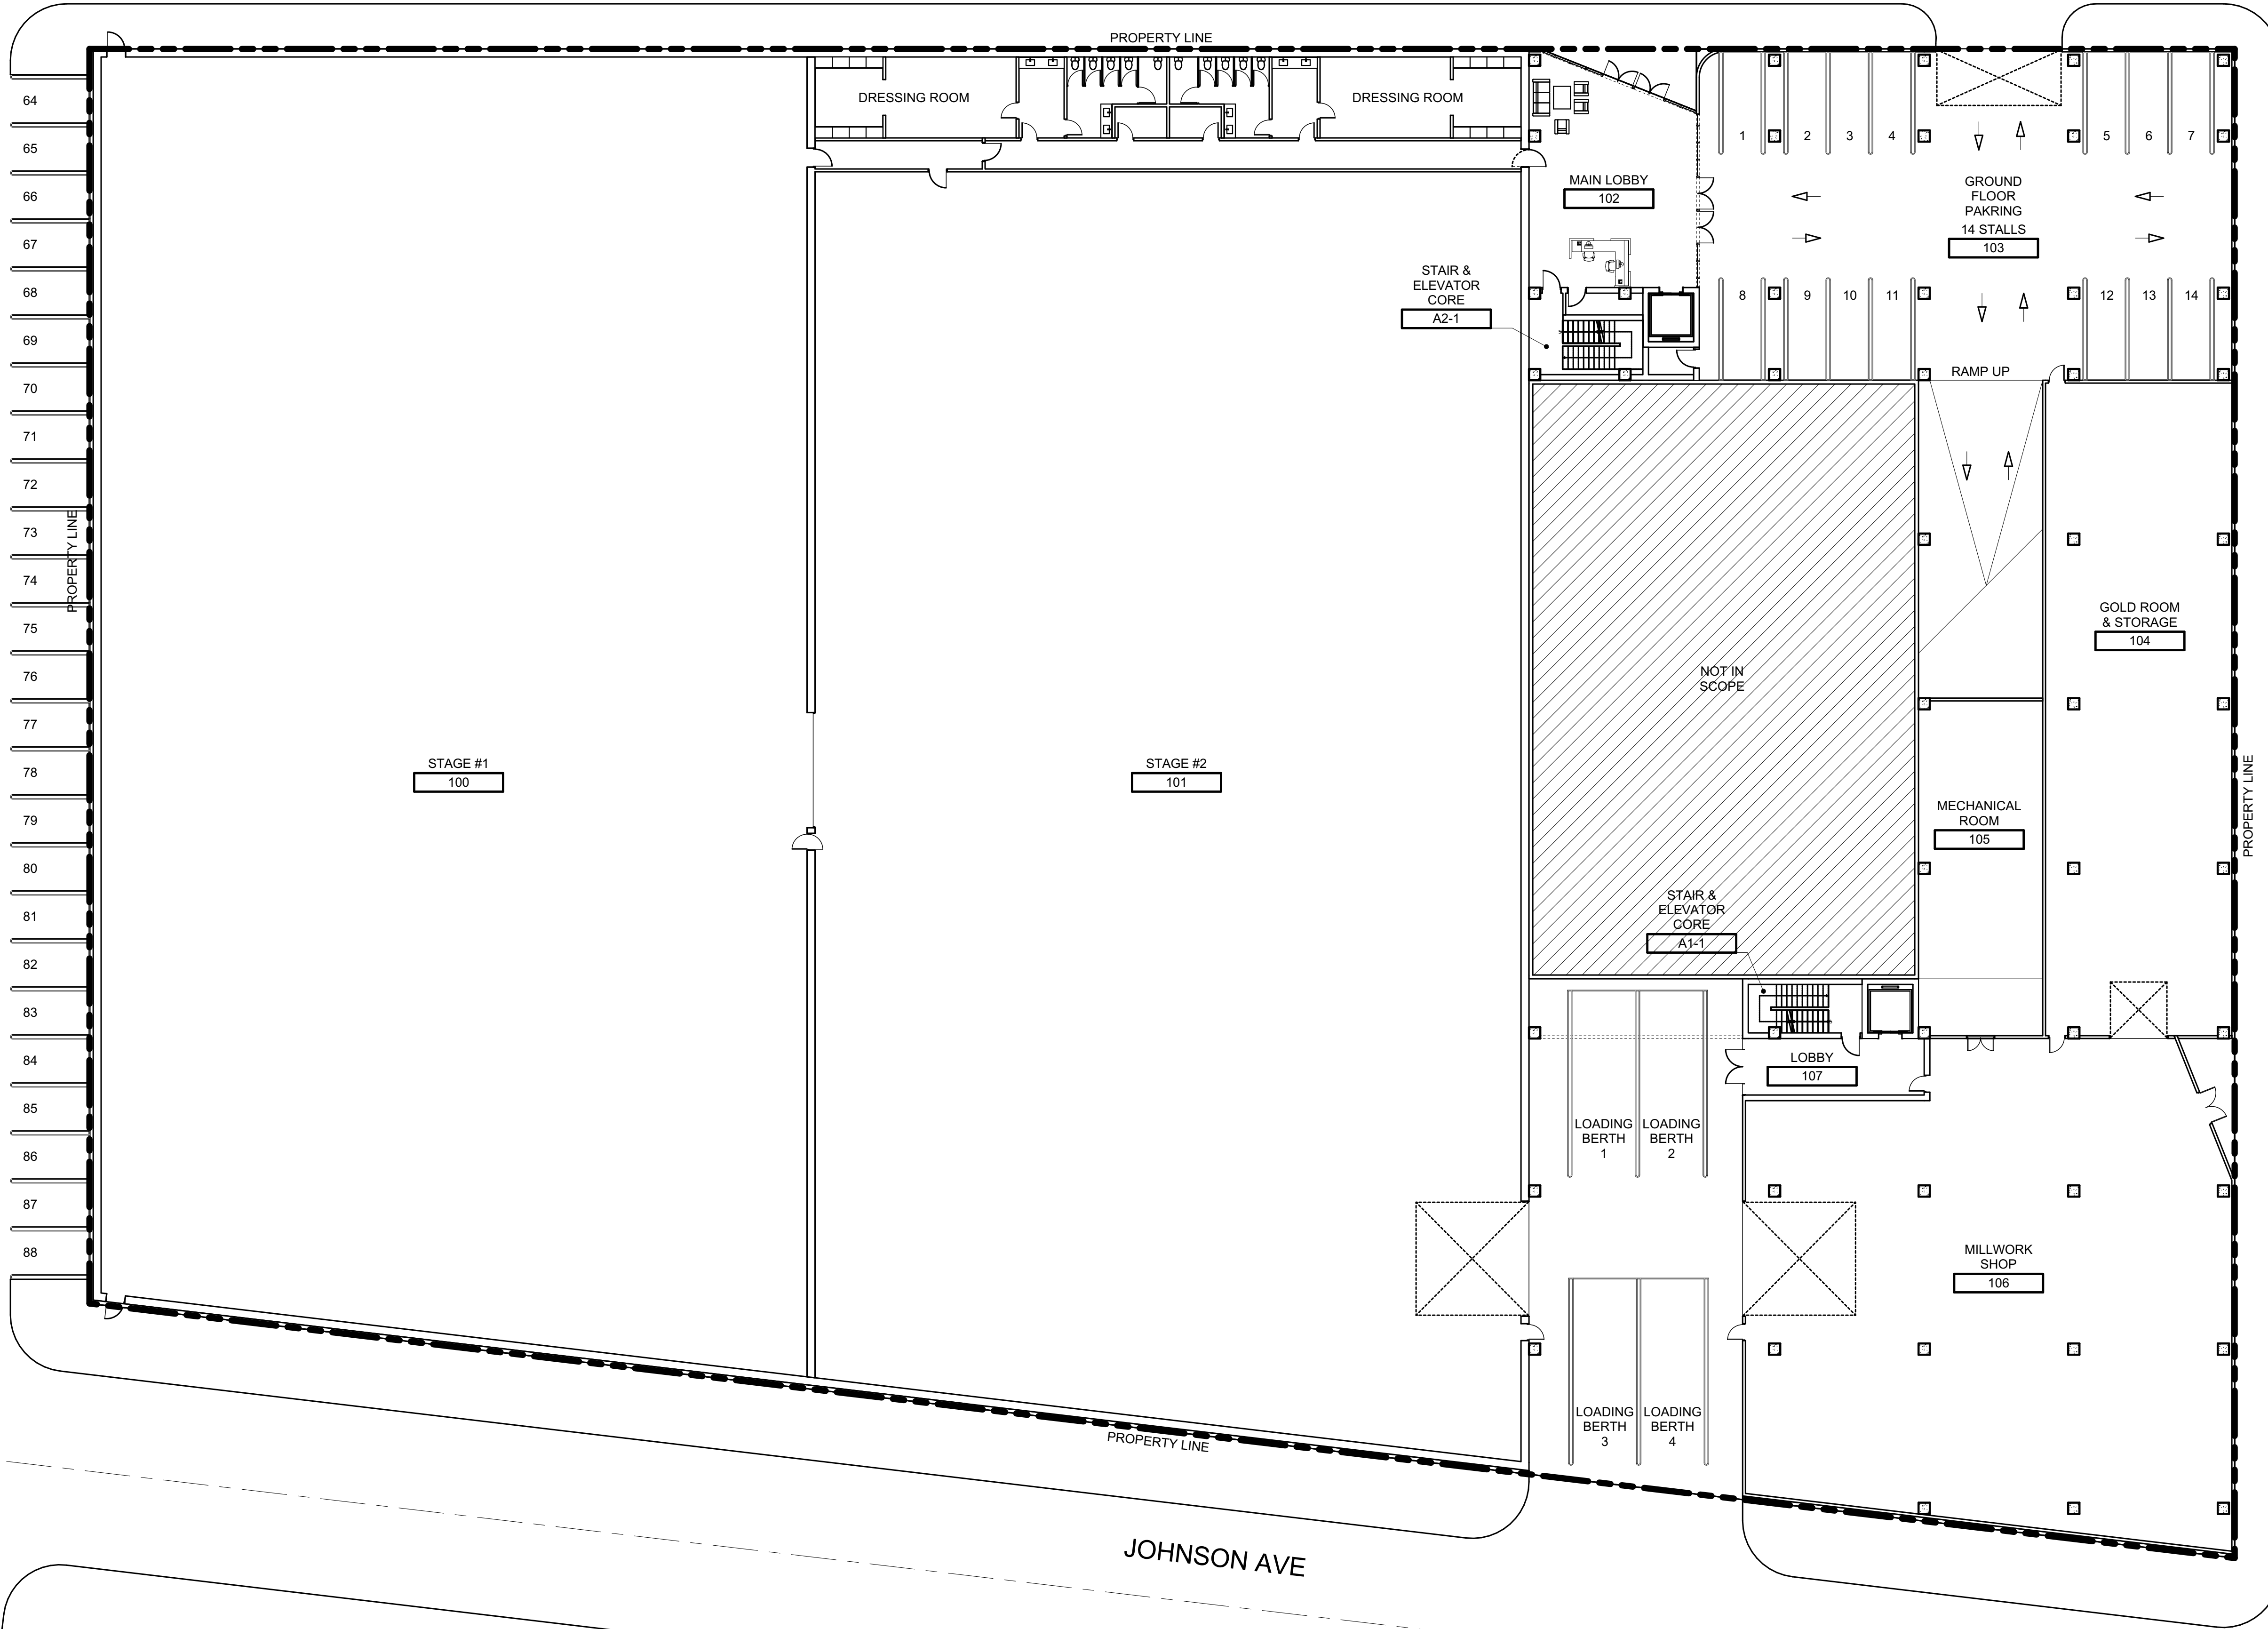

GARDNER AVE



JOHNSON AVE



GROUND FLOOR PLAN
SCALE: 1/16" = 1'-0"

1


GROUND FLOOR PLAN

DATE	ISSUE	#Project Description

DRAWN BY		#Pin
JOB NO.		
SCALE	1/16" = 1'-0"	

SHEET

A210

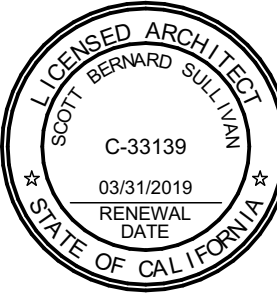


RELATIVITY
ARCHITECTS

www.relativityarchitects.com
1145 N MCCADDEN PL, LA, CA 90038 P:310.573.4300

555 JOHNSON
555 JOHNSON AVE
BROOKLYN, NY 11237

P:\1936A_555 Johnson\8 Drawings\Working Models\20191207 - 555 Johnson - JS.mxd 2019-12-27

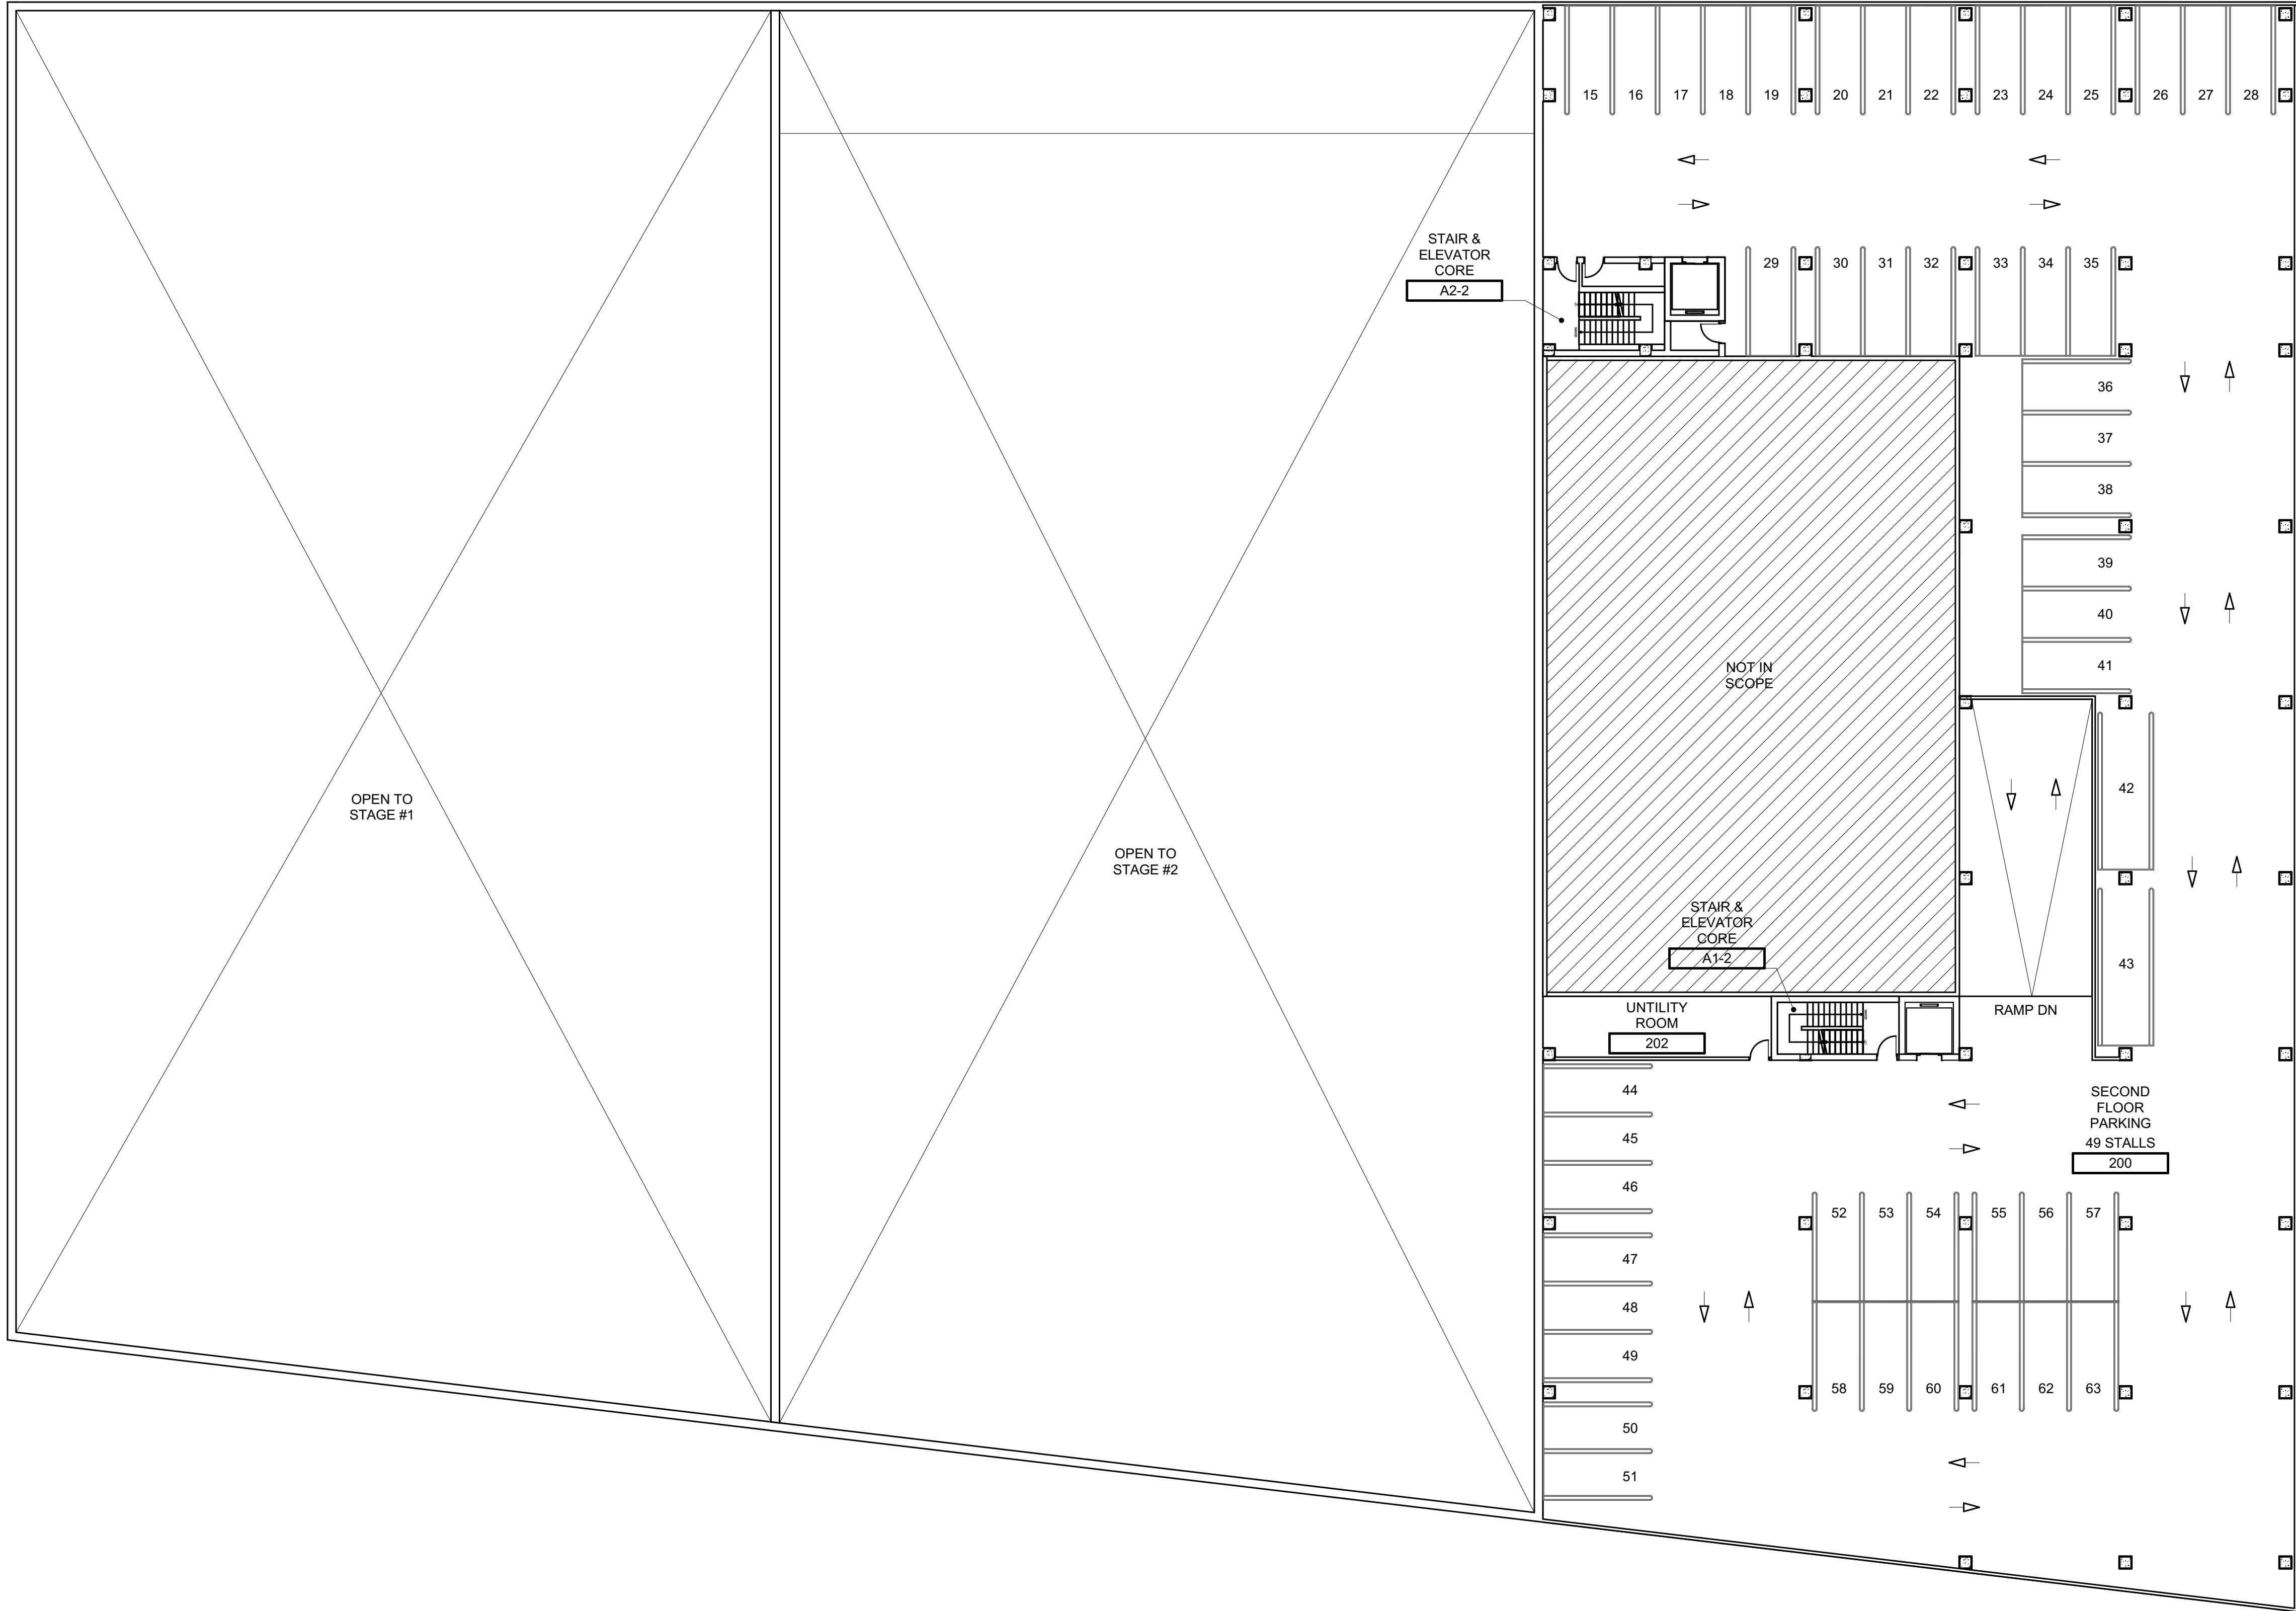

SECOND FLOOR PLAN

SCALE: 1/16" = 1'-0"

1


SECOND FLOOR PLAN

555 JOHNSON
555 JOHNSON AVE
BROOKLYN, NY 11237

DATE	ISSUE	#Project Description


DRAWN BY	
JOB NO.	#Pin
SCALE	1/16" = 1'-0"

SHEET
A220

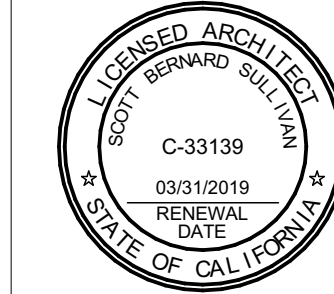

RELATIVITY
ARCHITECTS

www.relativityarchitects.com
1145 N MCCADDEN PL, LA, CA 90038 P:310.573.4300

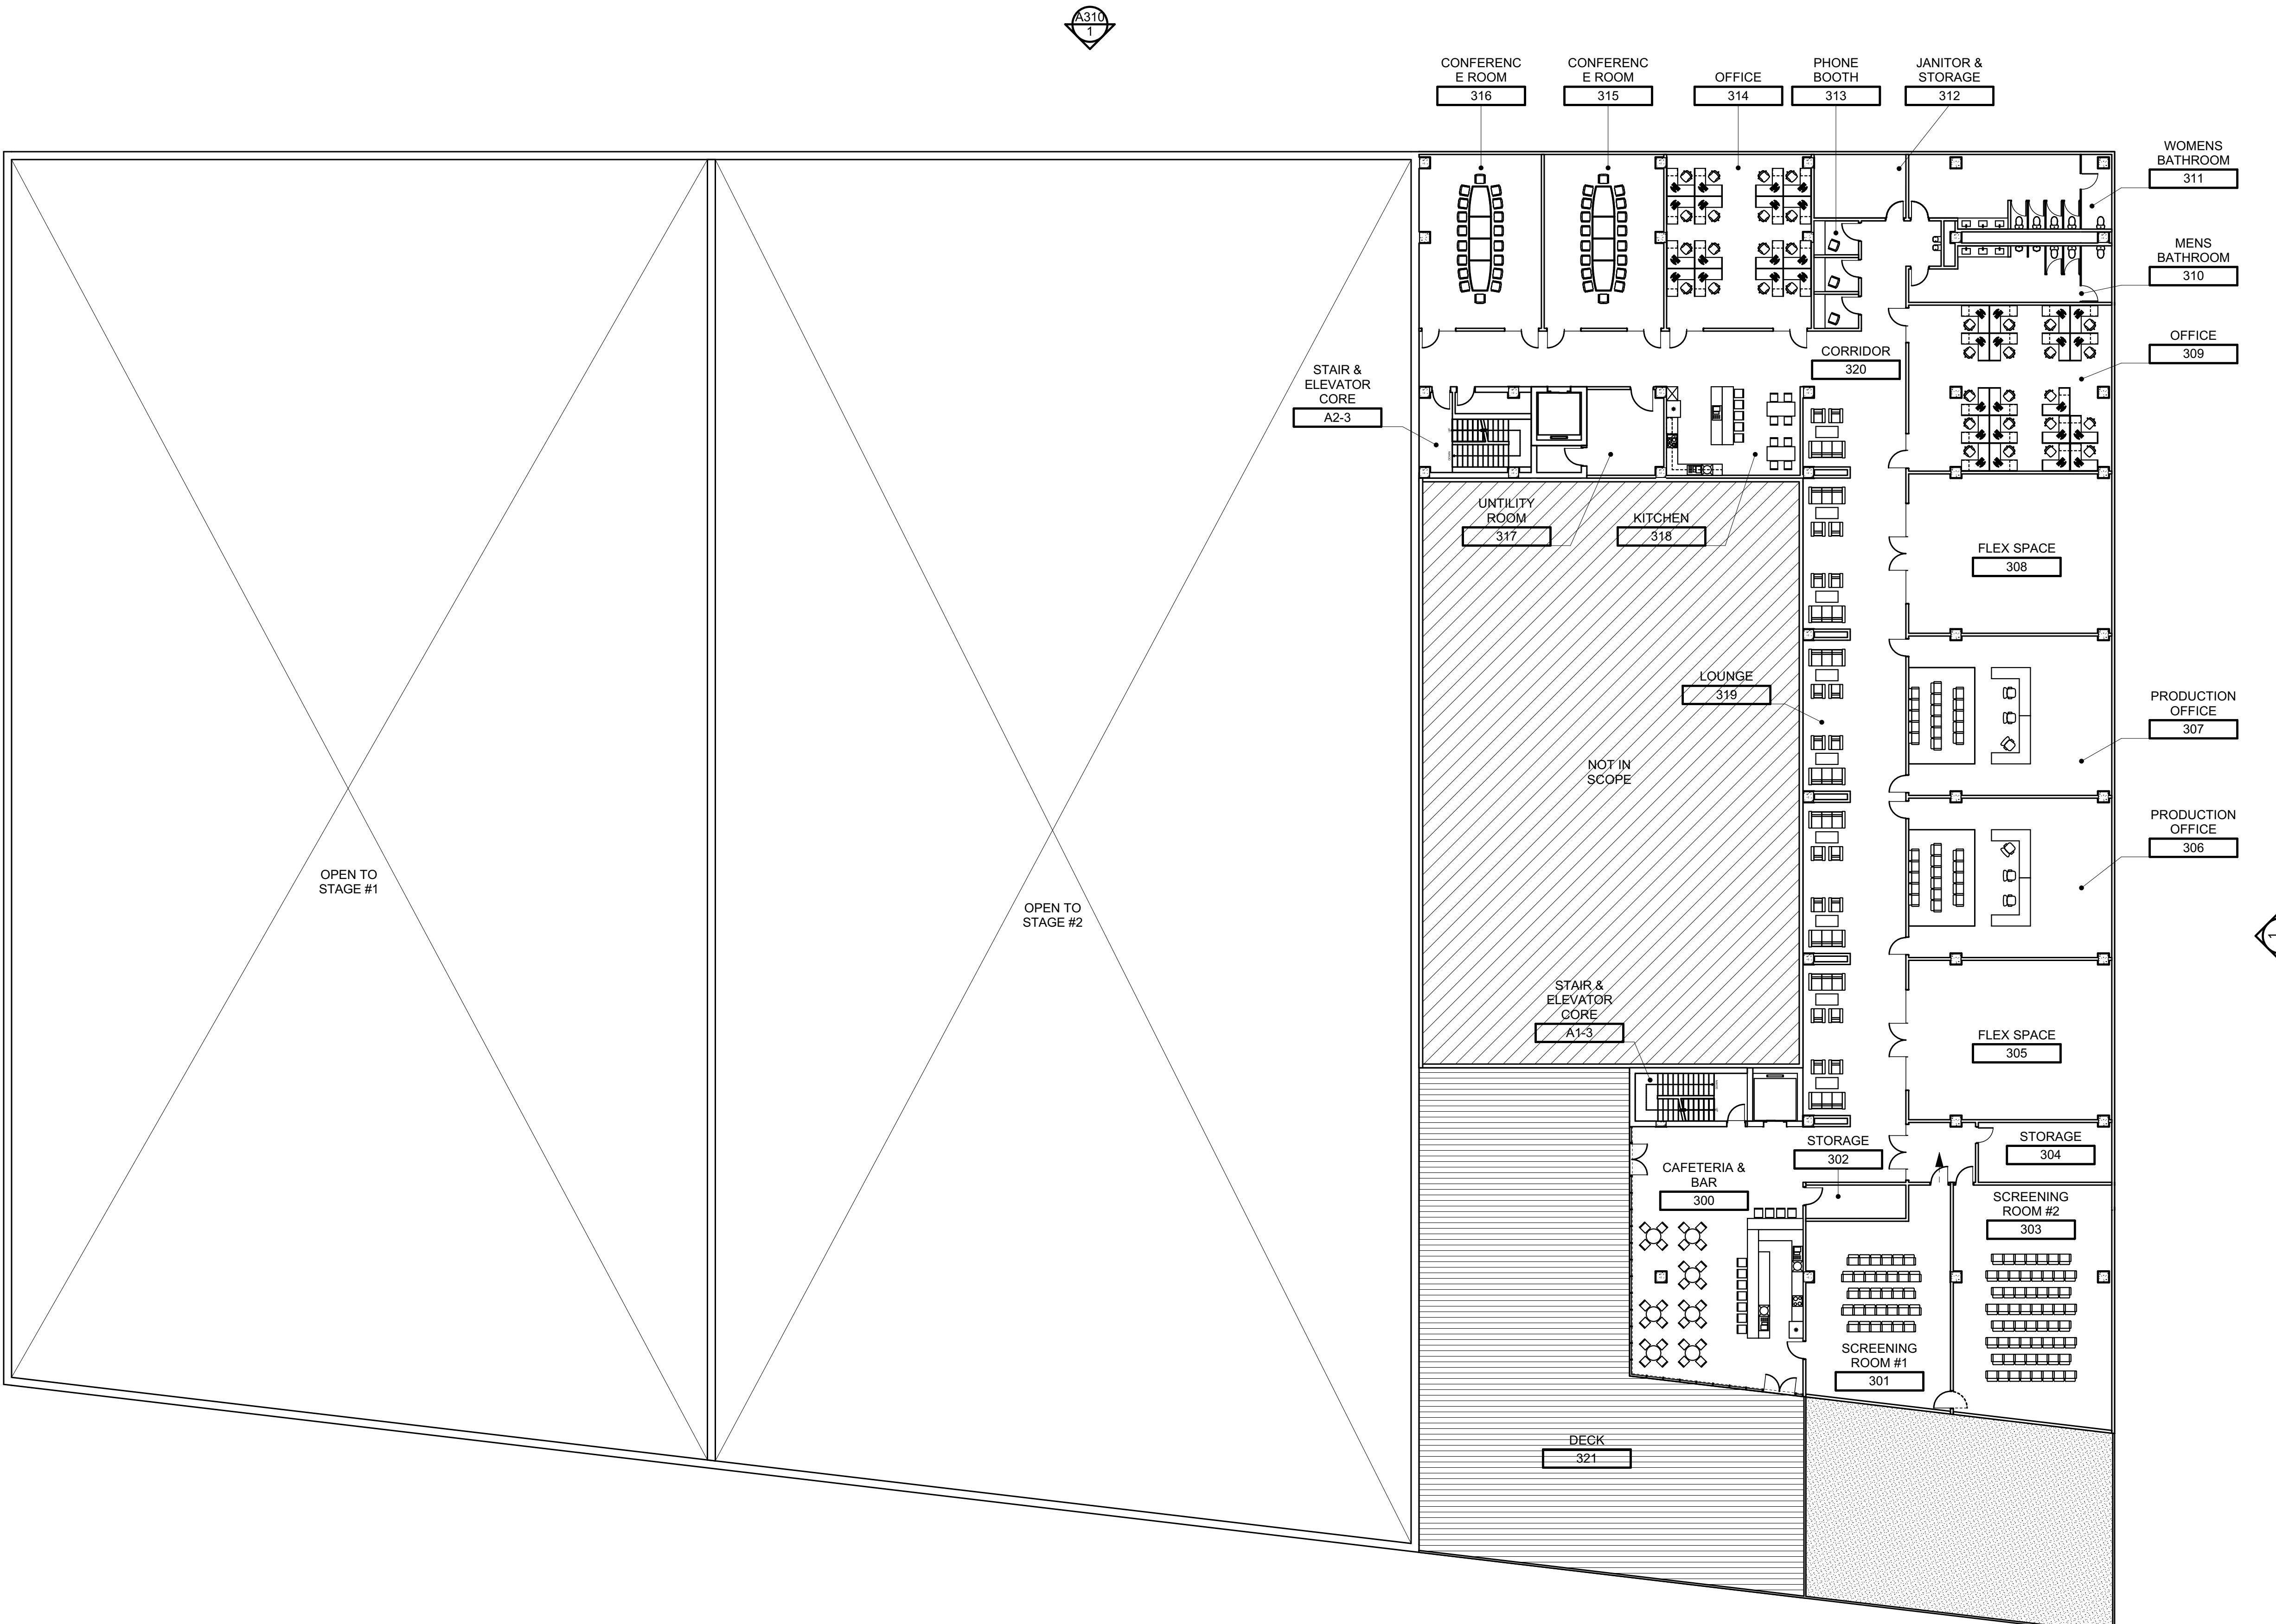

THIRD FLOOR PLAN

SCALE: 1/16" = 1'-0"

1

THIRD FLOOR PLAN

THIRD FLOOR	DATE	ISSUE
-------------	------	-------

ISSUE	#Project Description
-------	----------------------

DRAWN
BY

JOB
NO.

SCALE

#Pln


SCALE 1/16" = 1'-0"

SHEET



A230


5555 JOHNSON

555 JOHNSON AVE
BROOKLYN, NY 11237

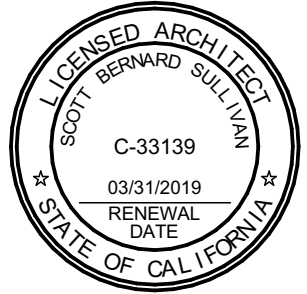RELATIVITY
ARCHITECTS

www.relativityarchitects.com
1145 N MCCADDEN PL, LA, CA 90038 P:310.573.4300

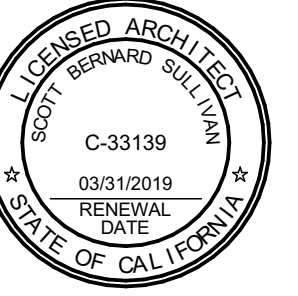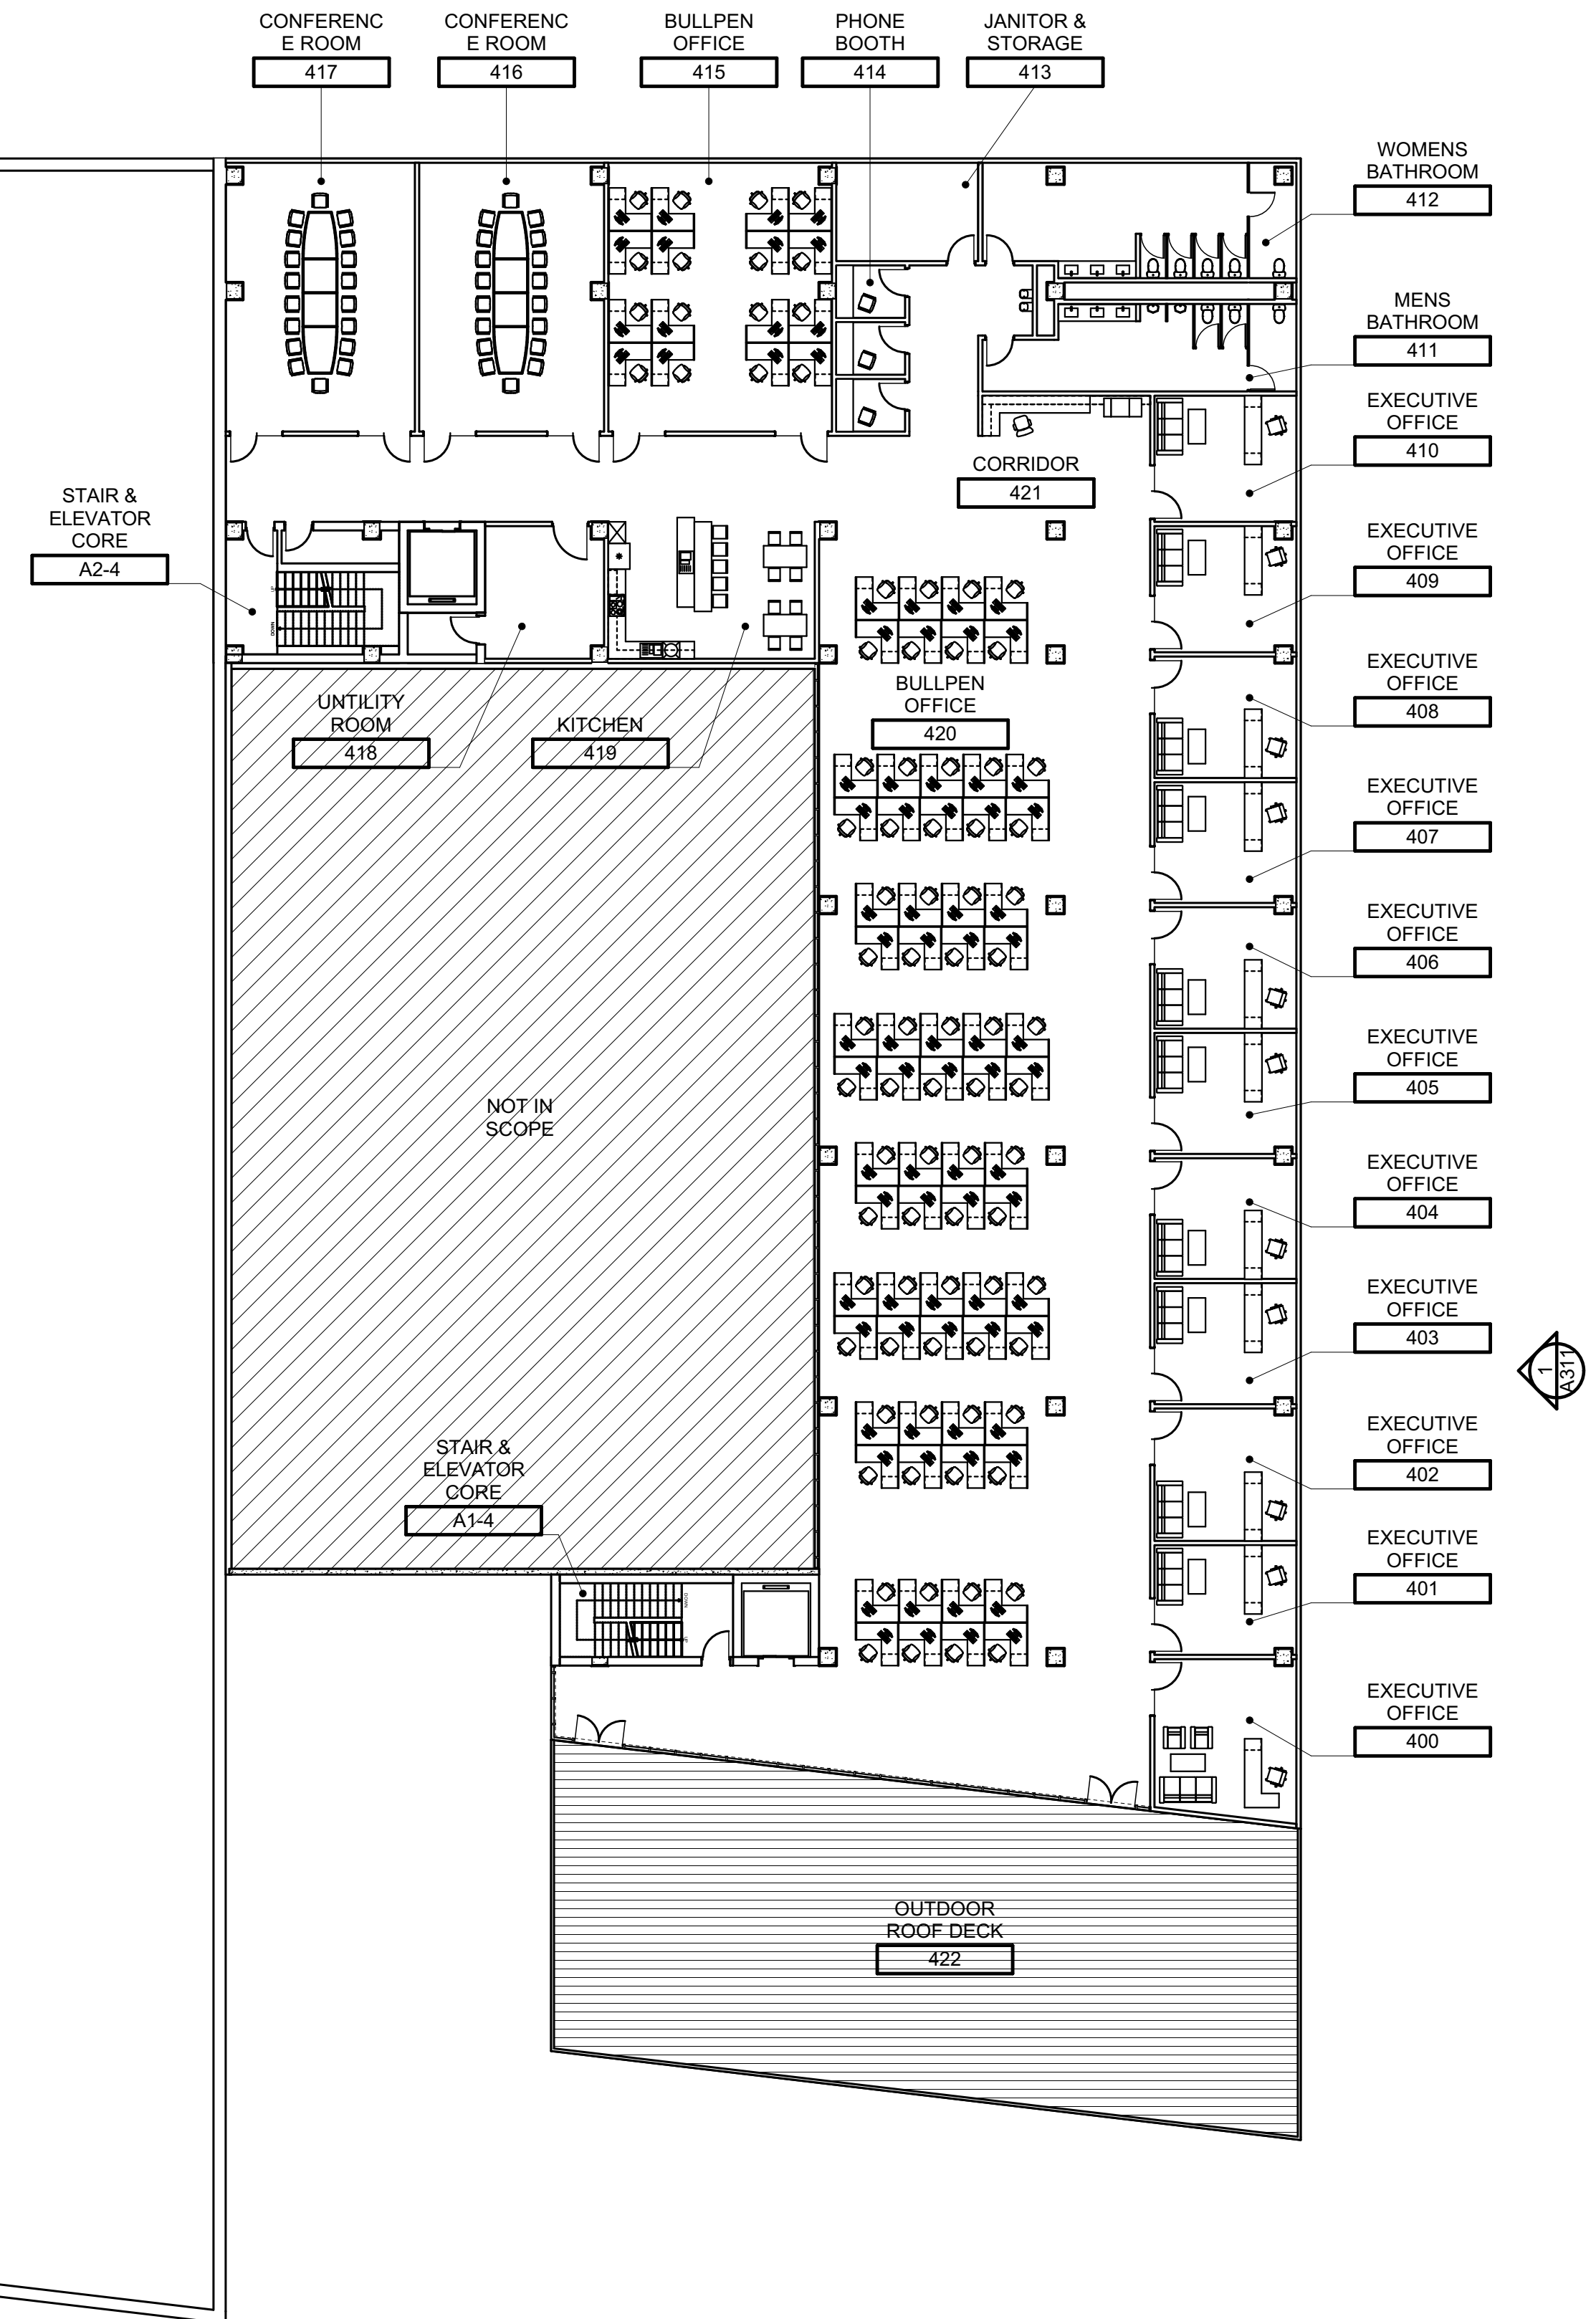

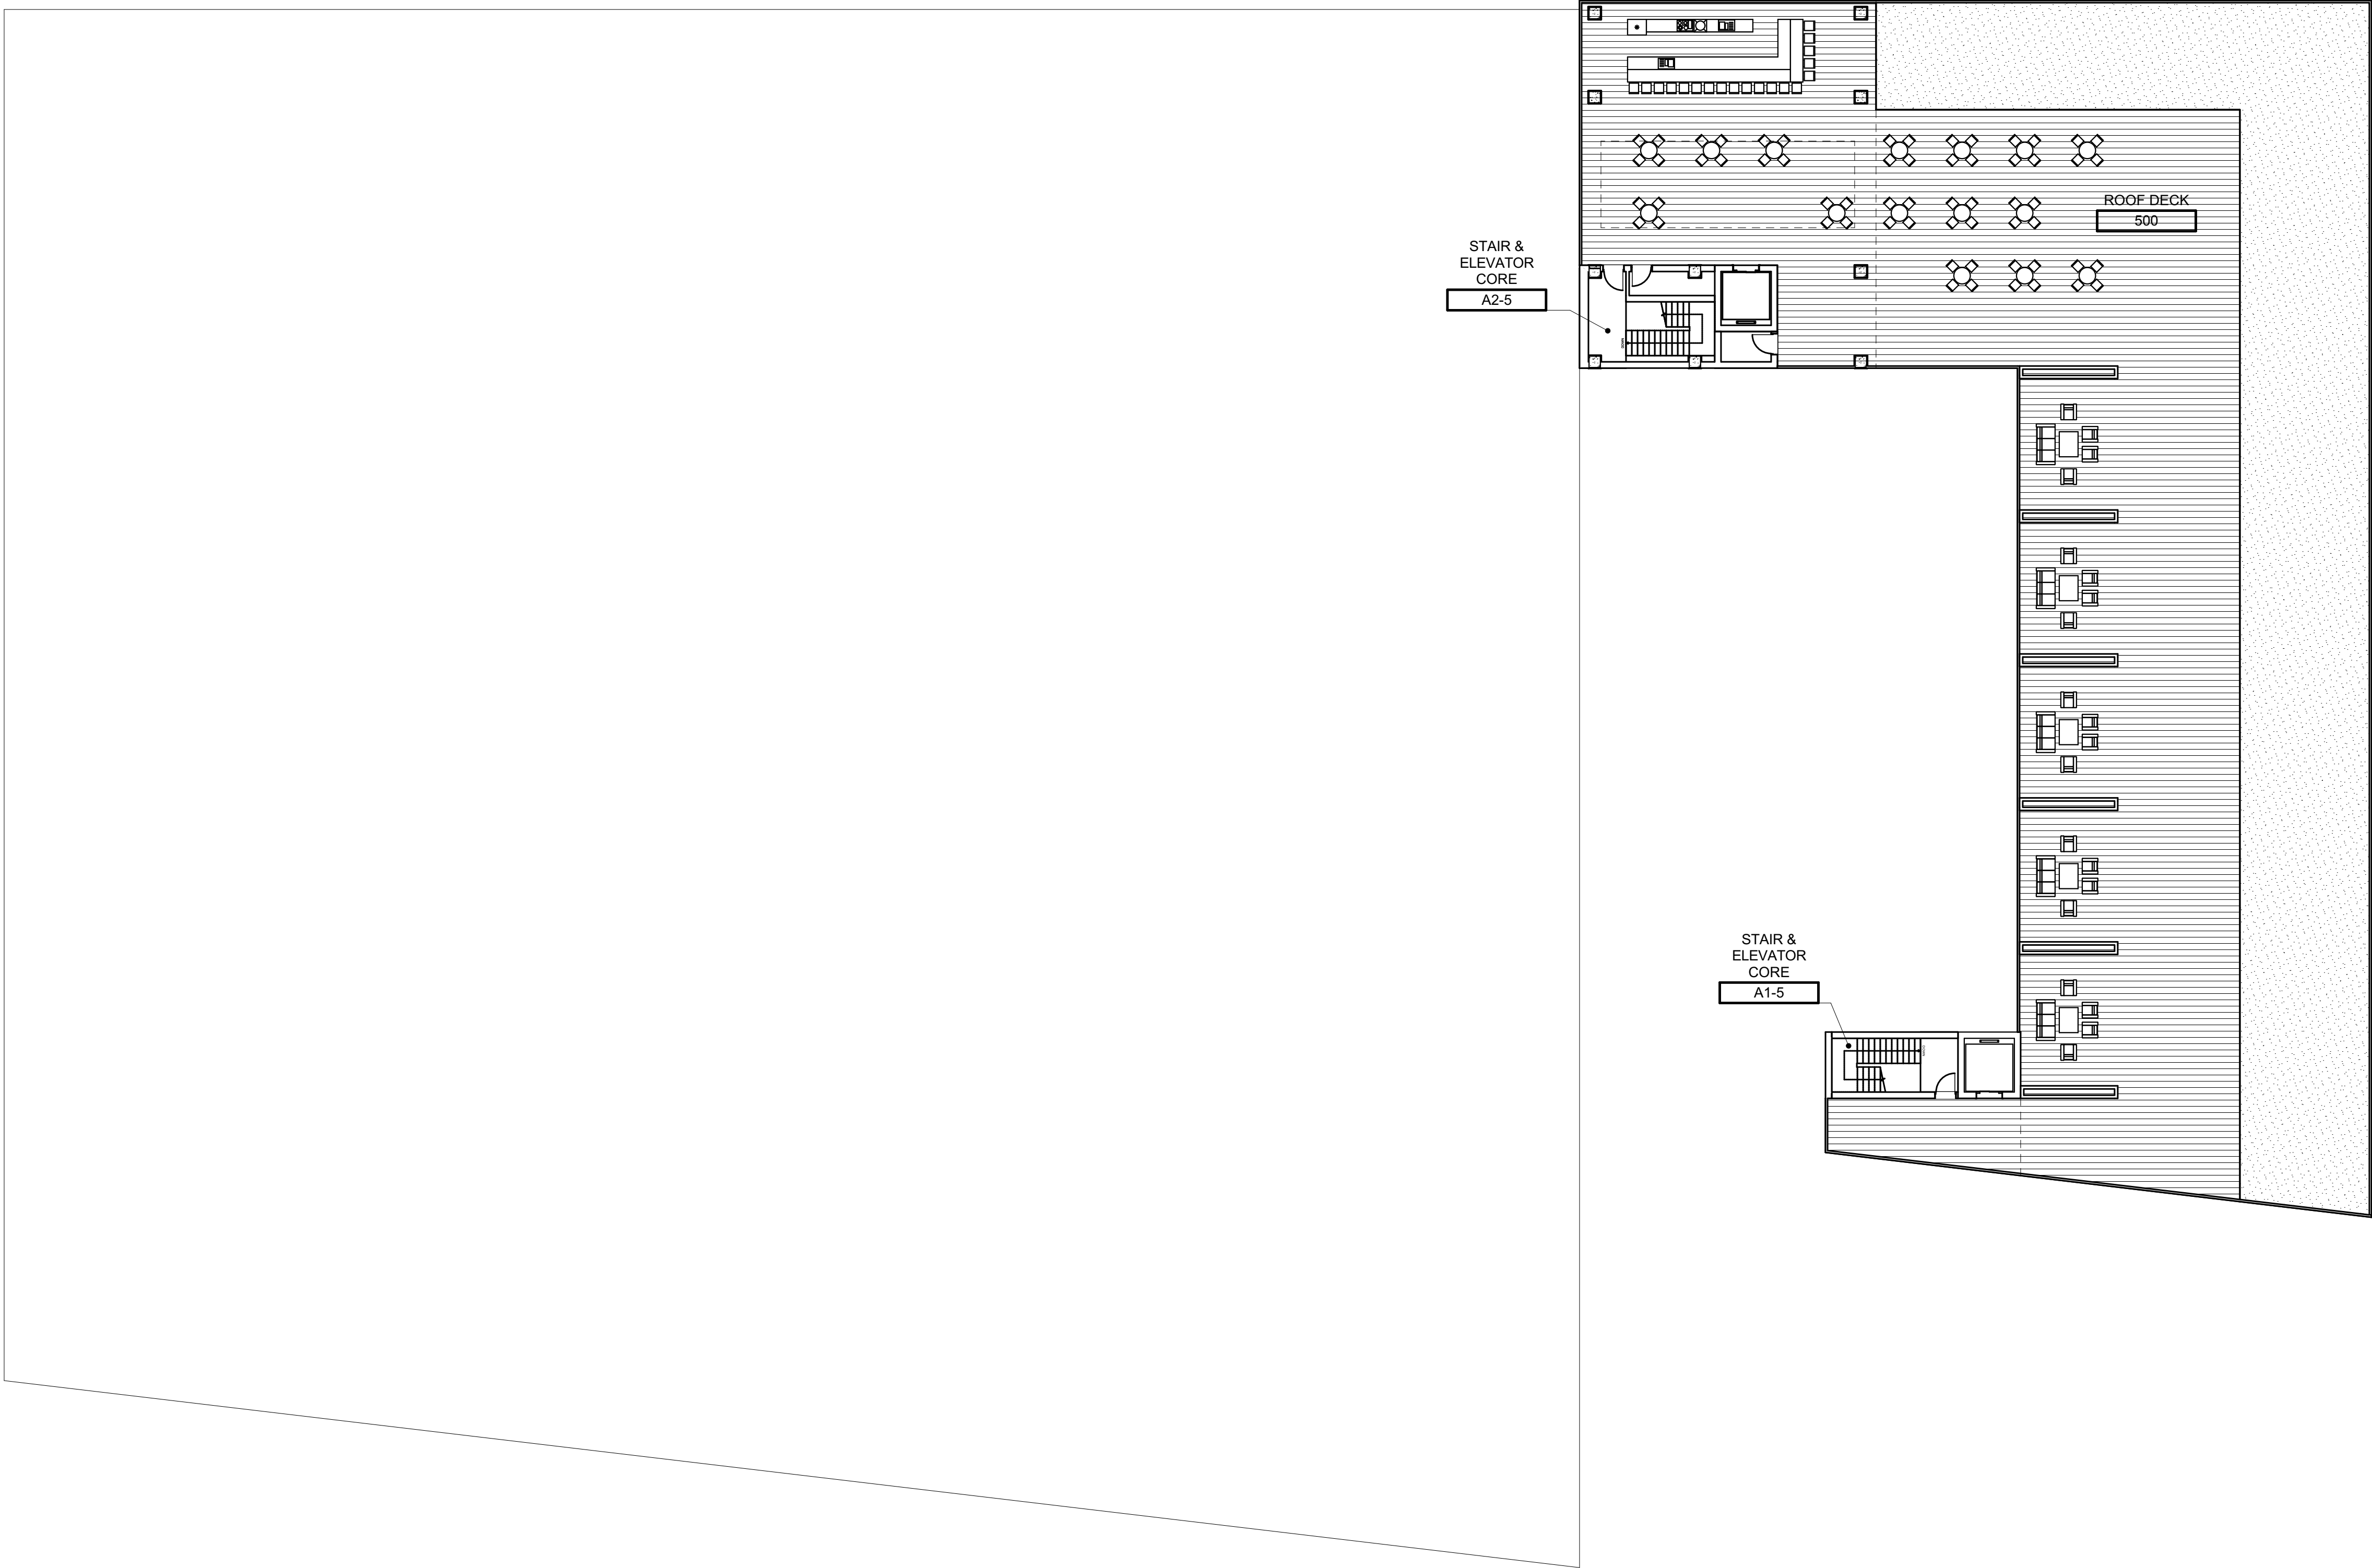

ROOF DECK PLAN
SCALE: 1/16" = 1'-0"

1


ROOF DECK PLAN

DRAWN BY	ISSUE	DATE	ISSUE	#Project Description
JOB NO.				
SCALE	1/16" = 1'-0"			

SHEET

A250


555 JOHNSON
555 JOHNSON AVE
BROOKLYN, NY 11237

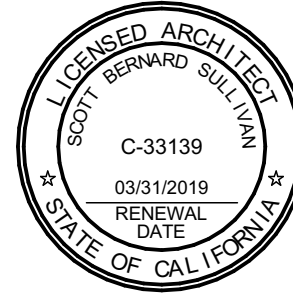

RELATIVITY
ARCHITECTS

www.relativityarchitects.com
1145 N MCCADDEN PL, LA, CA 90038 P:310.573.4300


P:\1826A_555 Johnson\8 Drawings\Working Models\201811205 - 555 Johnson - JS.jan 2018-12-06

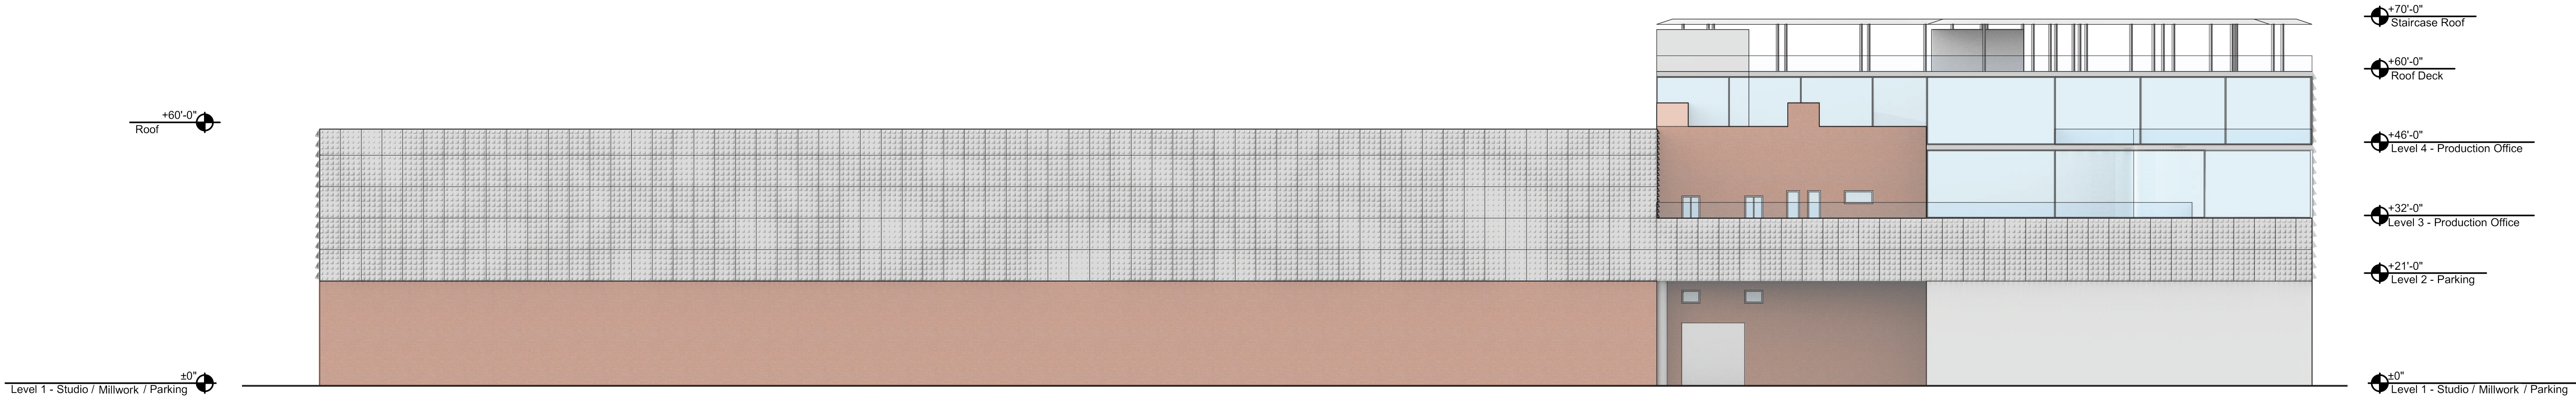

SOUTH ELEVATION

SCALE: 1/16" = 1'-0"

2

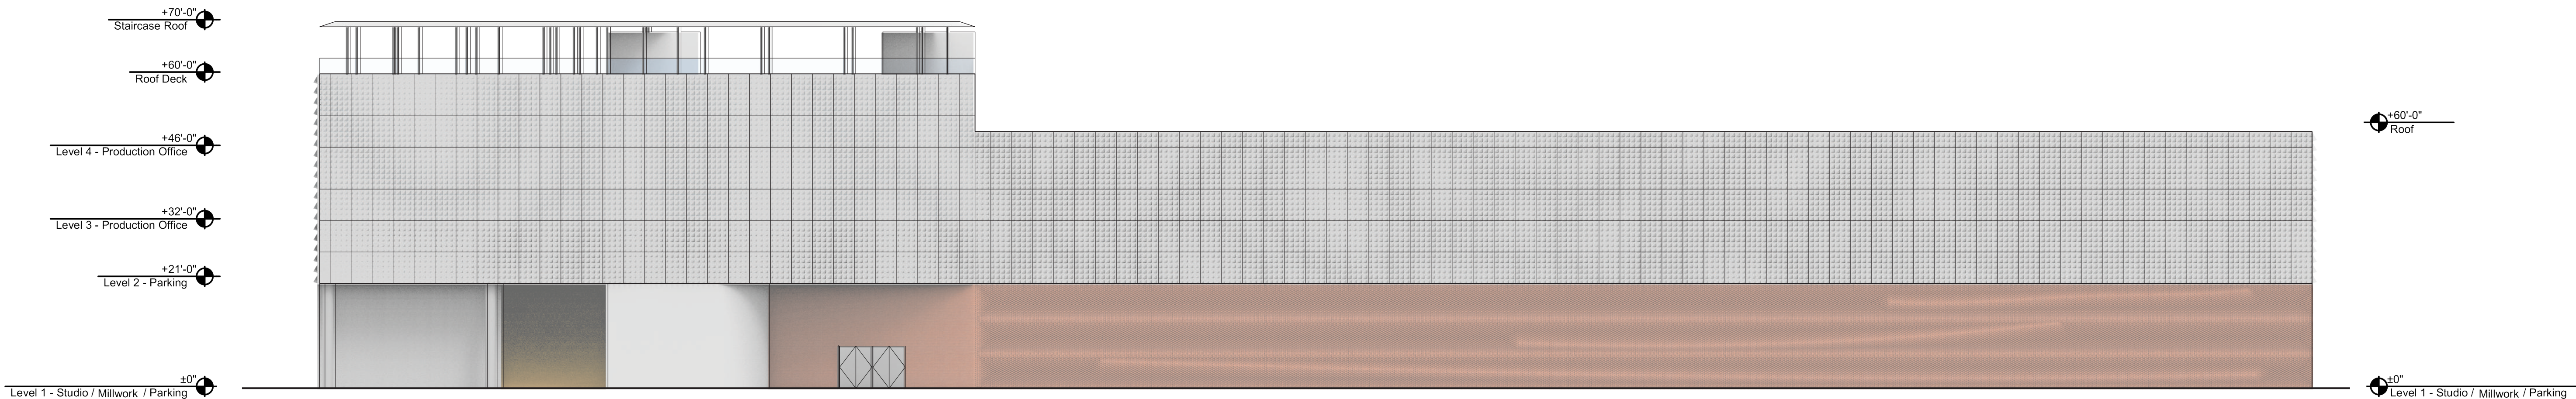


NORTH ELEVATION

SCALE: 1/16" = 1'-0"

1

RELATIVITY
ARCHITECTS

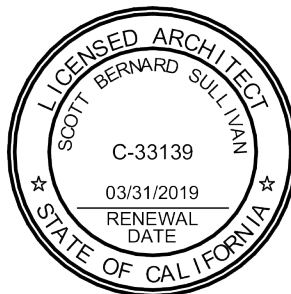

www.relativityarchitects.com
1145 N MCCADDEN PL, LA, CA 90038 P:310.573.4300

555 JOHNSON
555 JOHNSON AVE
BROOKLYN, NY 11237

Exterior Elevations

DATE

ISSUE

Schematic Design

DRAWN
BY

JOB
NO.

SCALE


1826A

1/16" = 1'-0"

SHEET

A310


P:\1926A_555 Johnson8 Drawings\Working Models\20181205 - 555 Johnson - 05.rvt 2018-12-26

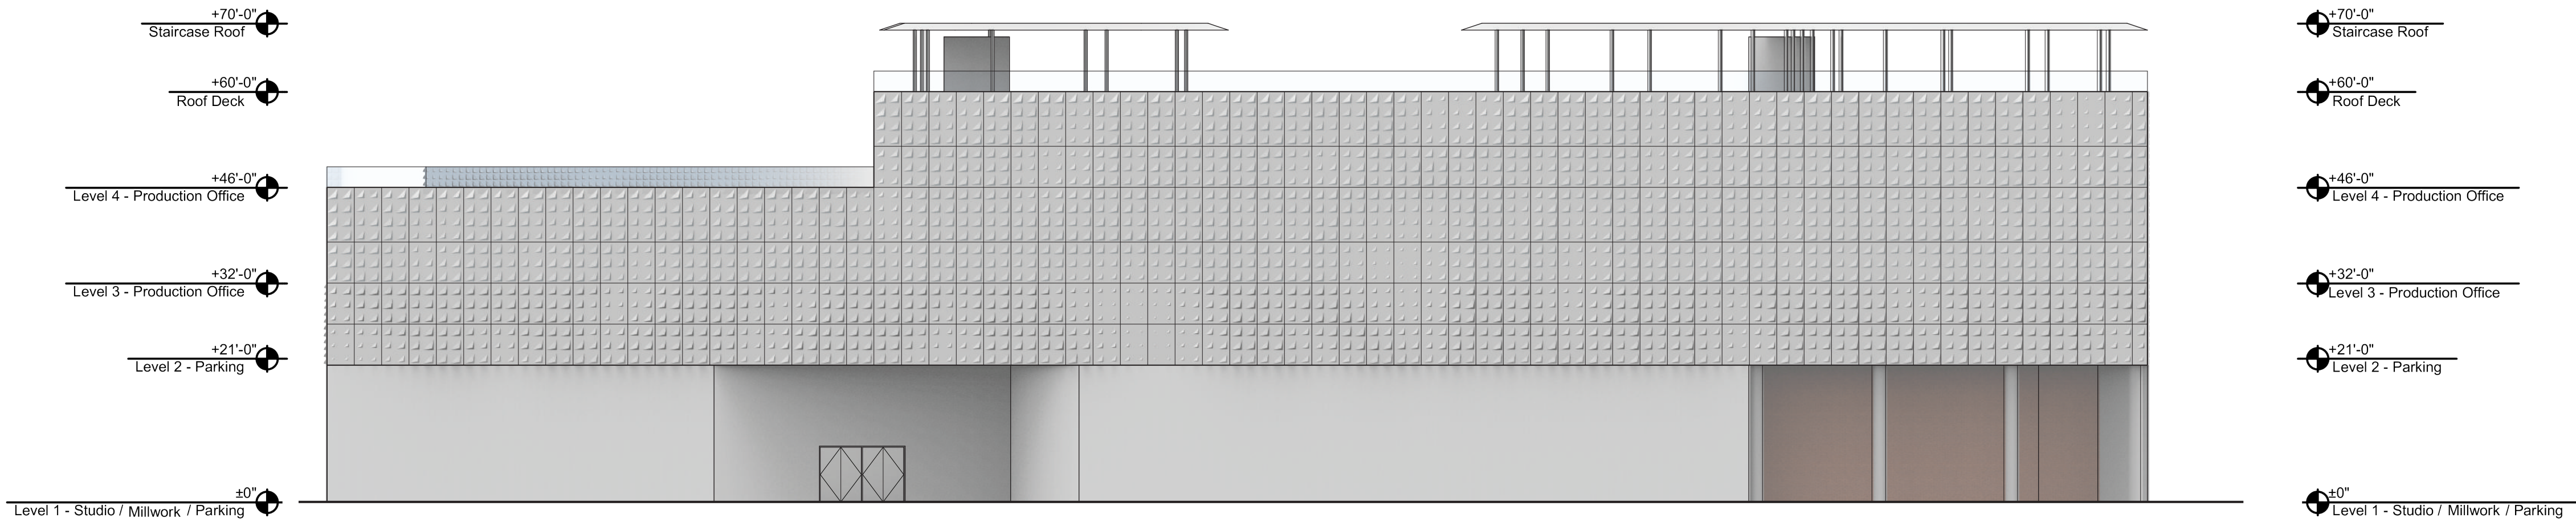

EAST ELEVATION

SCALE: 1/16" = 1'-0"

2

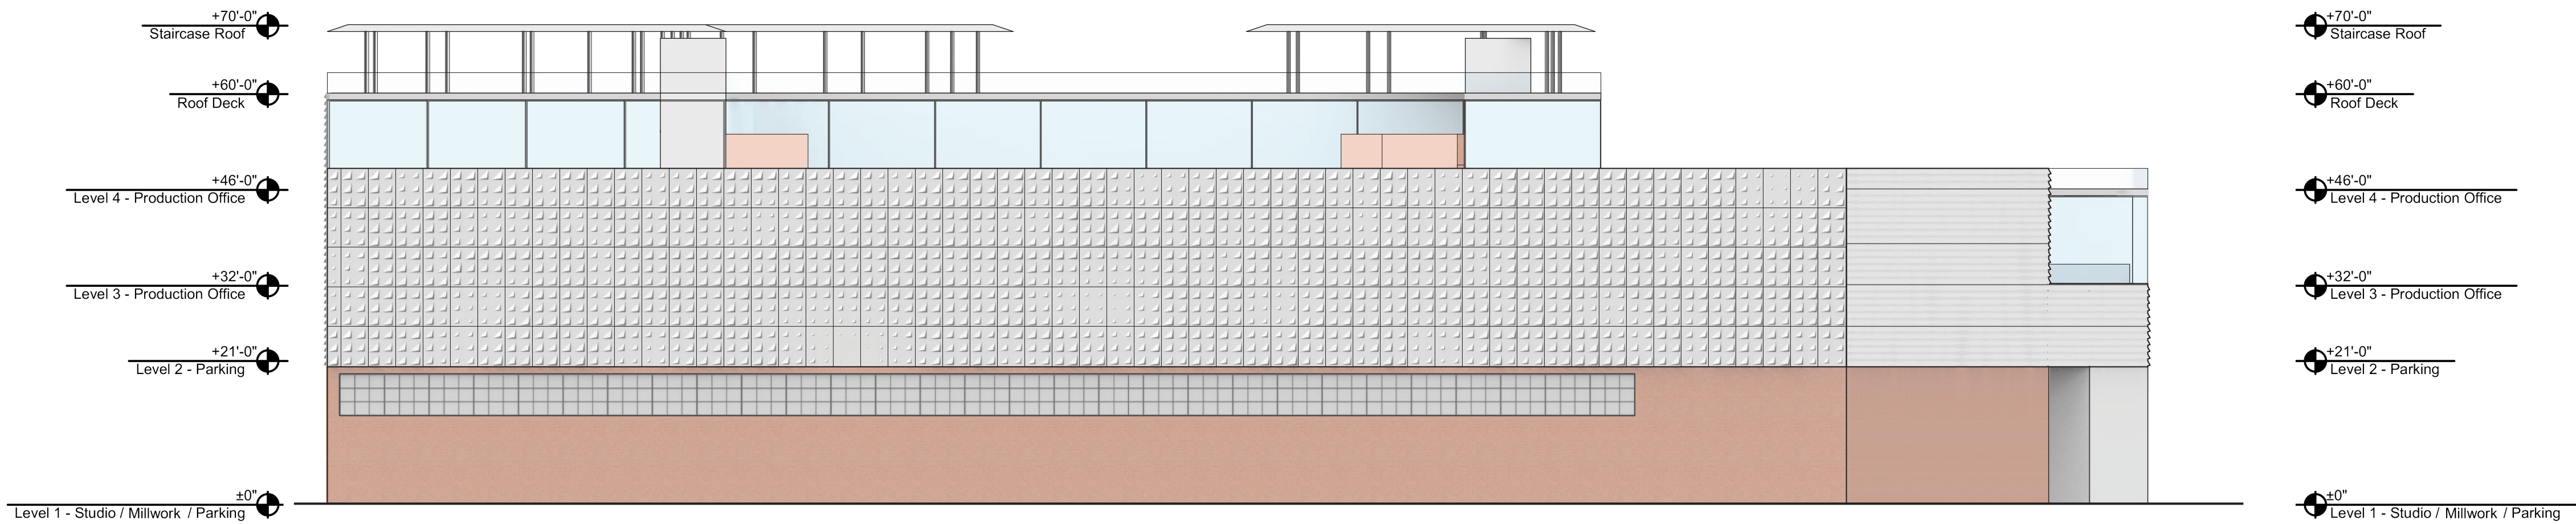


WEST ELEVATION

SCALE: 1/16" = 1'-0"

1

RELATIVITY
ARCHITECTS

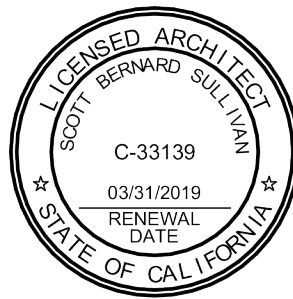

www.relativityarchitects.com
1145 N MCCADDEN PL, LA, CA 90038 P:310.373.4300

555 JOHNSON
555 JOHNSON AVE
BROOKLYN, NY 11237

Exterior Elevations

DATE

ISSUE

Schematic Design

DRAWN
BY

JOB
NO.

SCALE

1826A

1/16" = 1'-0"

SHEET

A311