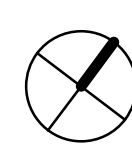


PROGRESS SET - NOT FOR CONSTRUCTION

 **Existing Masonry Wall, Foundation Layout and Proposed Pilecap Layout:**
Scale: 1/8" = 1'-0"

NOTES:

1. TOP OF CONC. SLAB ELEVATION (TSL) IS SHOWN THUS (+/-) ON PLAN.
2. SLAB TO BE A 6" THICK SLAB ON GRADE, REINFORCED W/6x6 - W2.9xW2.9 WWF ON VAPOR BARRIER.
3. EL. TO B.O. FOOTINGS ARE DENOTED THUS (+/-) ON PLAN RELATIVE TO BASEPLANE.
4. ALL FOOTINGS SHALL BEAR ON SOIL WITH A MINIMUM 2.5 TON/SQ. FT. CAPACITY.
5. WALL BUTTRESSES ARE TYPE WB1 UNLESS OTHERWISE NOTED.
6. BOTTOM ELEVATION OF SPREAD FOOTING TO BE (-2'-2") FROM TOP OF SLAB, UNLESS OTHERWISE NOTED.
7. TIE (OR STRAP) BEAMS ARE TO BE 2'-0" DEEP WITH TOP AND BOTTOM REINFORCEMENT 3 - (#6) EXTENDED A MINIMUM OF 3'-0" INTO THE FOOTINGS. STIRRUPS ARE TO BE #3 BARS @ 10" O.C. THE TIE BEAMS ARE THUS DENOTED ON PLANS (TB-1).
8. FOR FOOTING, BUTTRESS, AND WALL REINFORCEMENT SEE SCHEDULES AND DETAILS SHOWN ON THIS DRAWING AND SECTION DETAILS.
9. SEE DRAWINGS 5-001 FOR GENERAL NOTES, LIST OF ABBREVIATIONS AND LEGEND.
10. CONTRACTOR SHALL CONDUCT PRECONSTRUCTION SURVEY OF ADJACENT EXISTING BUILDINGS BEFORE EXCAVATION, UNDERPINNING OR STIFF SHEETING AS REQUIRED.

Ex. Conditions - Structural Interior Rendering:
Scale:

PROGRESS SET - NOT FOR CONSTRUCTION

Client: _____

Tel: --- Email: ---

Contractor: **Cristom Construction Services**
151-01 14th Avenue
Whitestone NY 11357

Tel: (718) 747-4747 Email: info@cristomconstruction.com

[illegible]


ADDRESS

**537-561 Johnson Avenue
Brooklyn NY 11237**

SHEET TITLE

**Existing Foundation Plan and
Slab Layout @ 561 Johnson
Avenue**

 Orient and affix BIS job number label here 

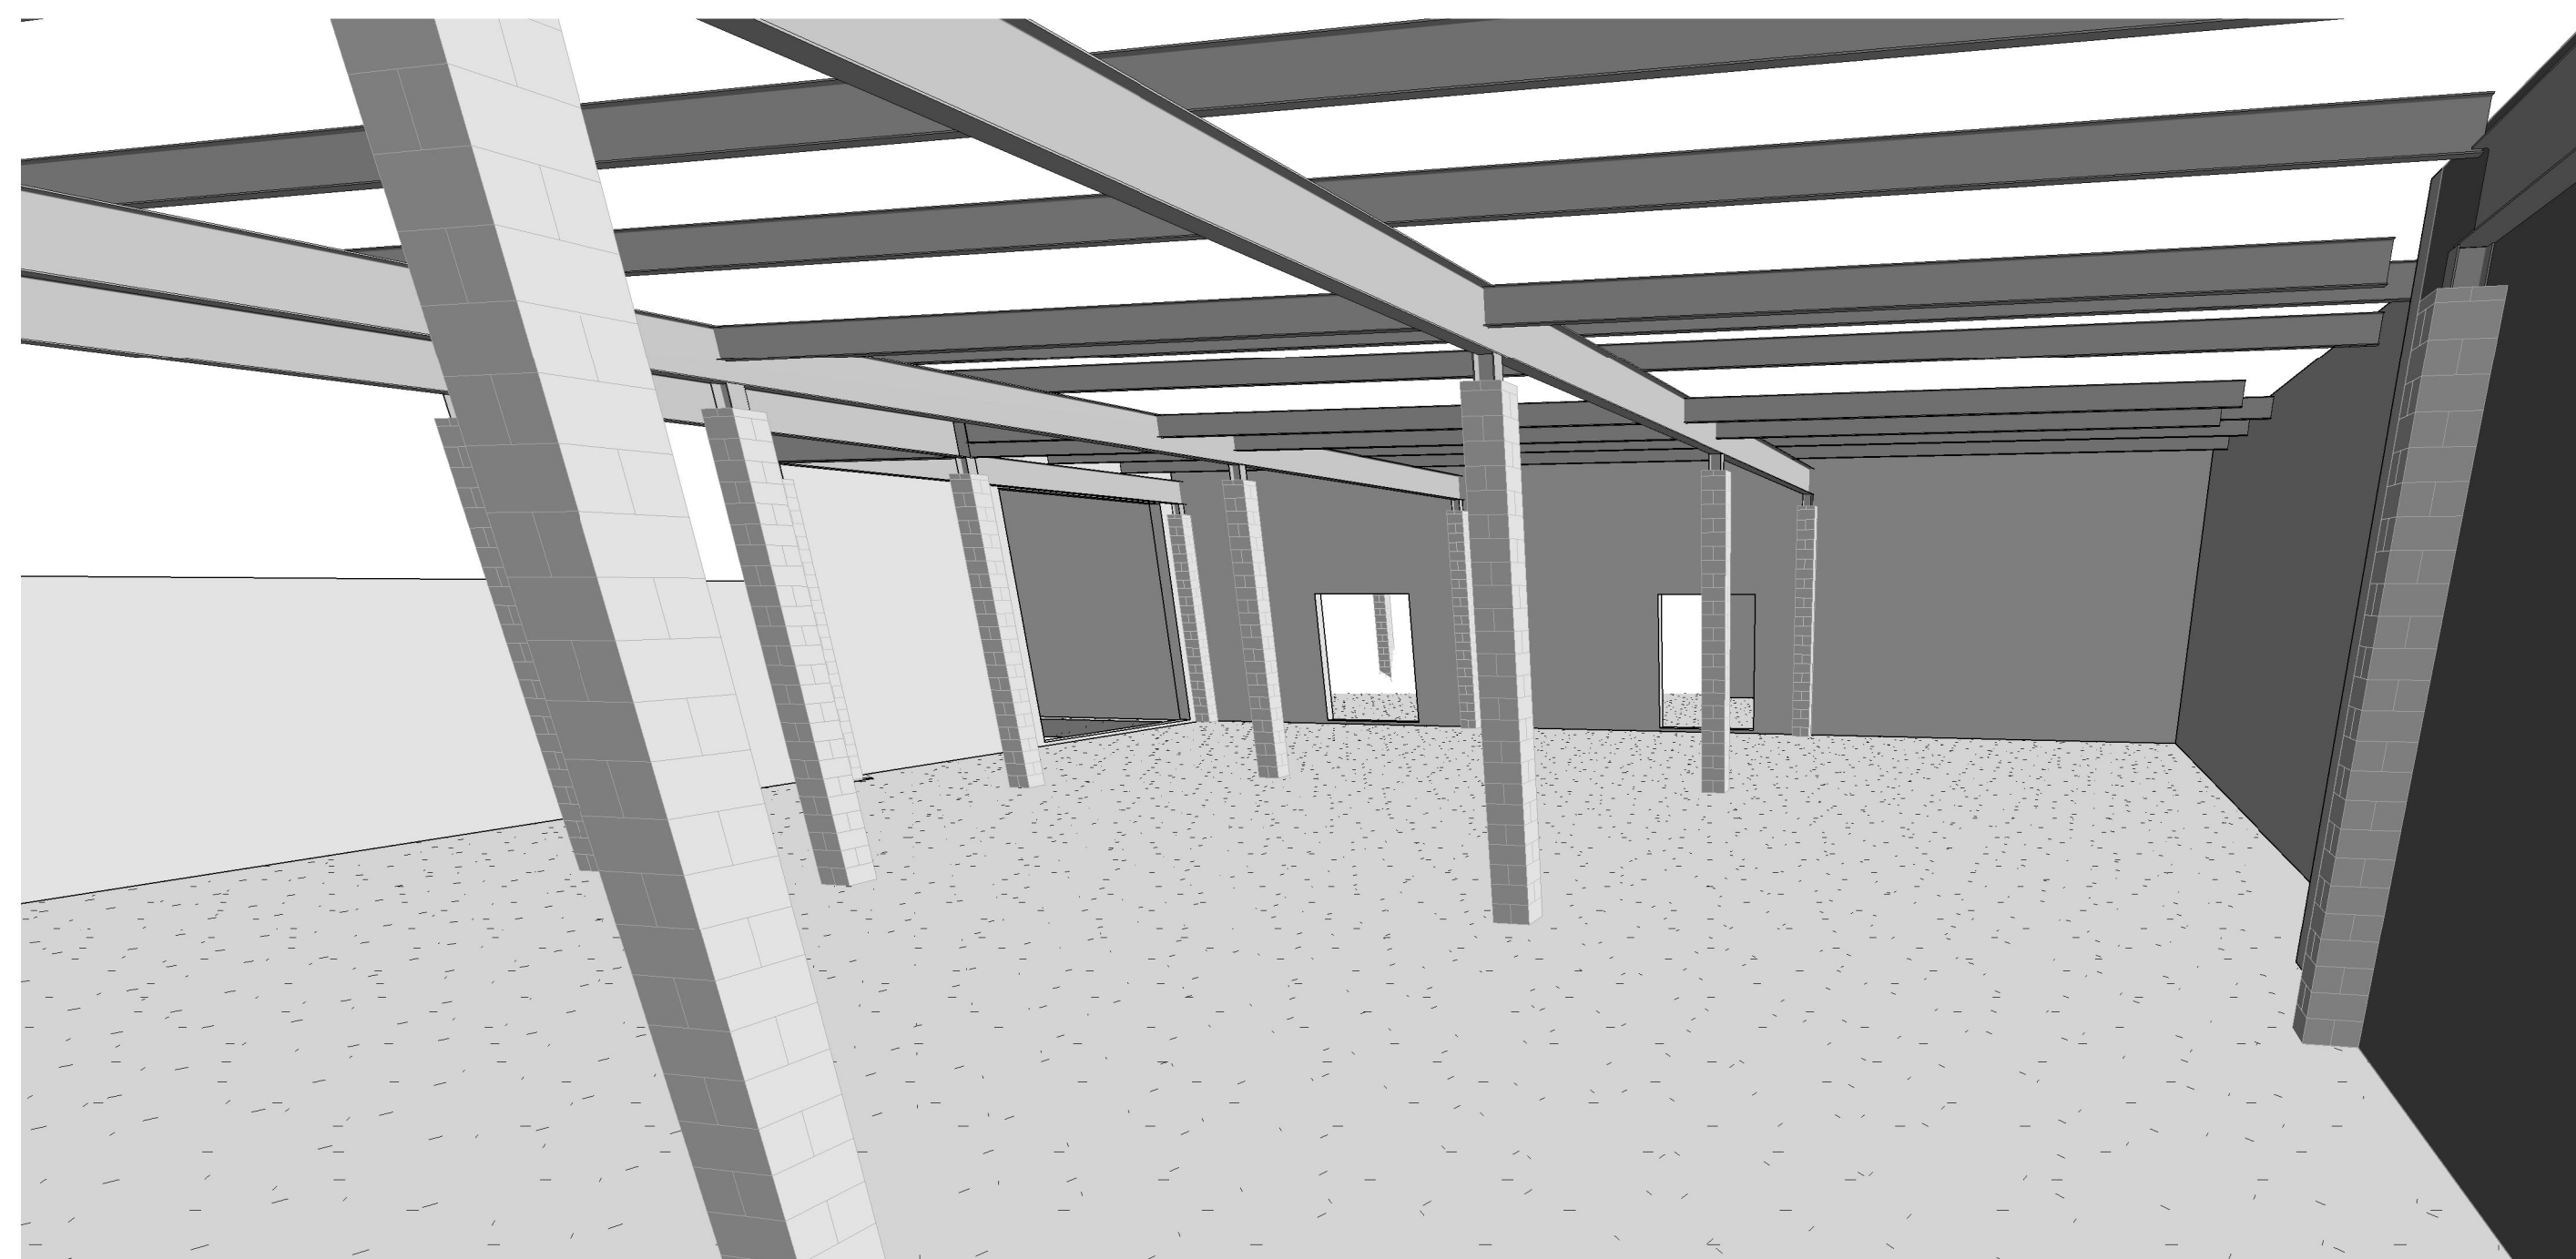

Scale:

PROGRESS SET - NOT FOR CONSTRUCTION




Partial Foundation Plan and Slab Layout (1 of 3):

Scale: 3/16" = 1'-0"


NOTES:

1. TOP OF CONC. SLAB ELEVATION (T/SL) IS SHOWN THUS [+/-] ON PLAN.
2. SLAB TO BE A 6" THICK SLAB ON GRADE, REINFORCED W6x6 - W2.9xW2.9 WWF ON VAPOR BARRIER.
3. EL. TO B.O. FOOTINGS ARE DENOTED THUS (+/-) ON PLAN RELATIVE TO BASEPLANE.
4. ALL FOOTINGS SHALL BEAR ON SOIL WITH A MINIMUM 2.5 TON/SQ. FT. CAPACITY.
5. WALL BUTTRESSES ARE TYPE WB1 UNLESS OTHERWISE NOTED.
6. BOTTOM ELEVATION OF SPREAD FOOTING TO BE (-2'-2") FROM TOP OF SLAB, UNLESS OTHERWISE NOTED.
7. TIE (OR STRAP) BEAMS ARE TO BE 2'-0" DEEP WITH TOP AND BOTTOM REINFORCEMENT 3 - (#6) EXTENDED A MINIMUM OF 3'-0" INTO THE FOOTINGS. STIRRUPS ARE TO BE #3 BARS @ 10" O.C. THE TIE BEAMS ARE THUS DENOTED ON PLANS (TB-1).
8. FOR FOOTING, BUTTRESS, AND WALL REINFORCEMENT SEE SCHEDULES AND DETAILS SHOWN ON THIS DRAWING AND SECTION DETAILS.
9. SEE DRAWINGS S-001 FOR GENERAL NOTES, LIST OF ABBREVIATIONS AND LEGEND.
10. CONTRACTOR SHALL CONDUCT PRECONSTRUCTION SURVEY OF ADJACENT EXISTING BUILDINGS BEFORE EXCAVATION. UNDERPINNING OR STIFF SHEETING AS REQUIRED.

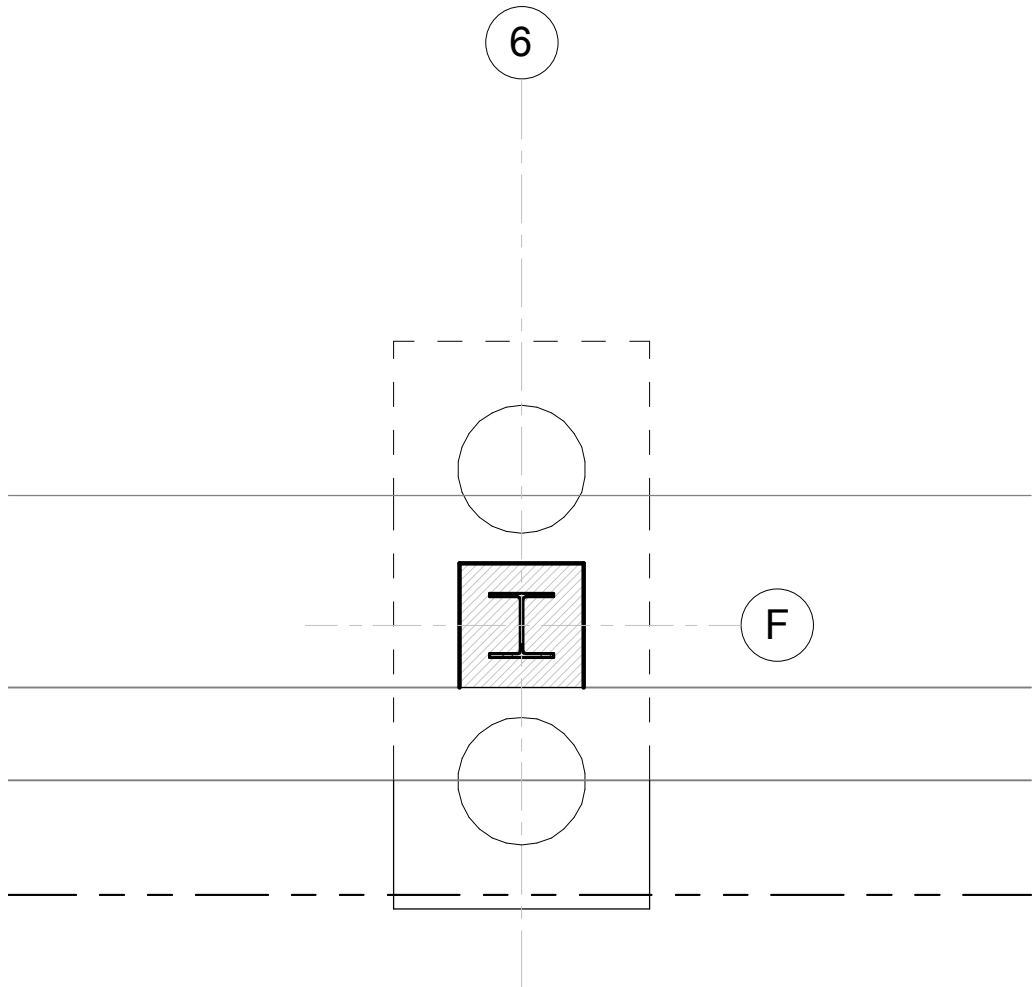

Detail 1 Proposed Pilecap Retrofit Detail:

Scale: 1/2" = 1'-0"

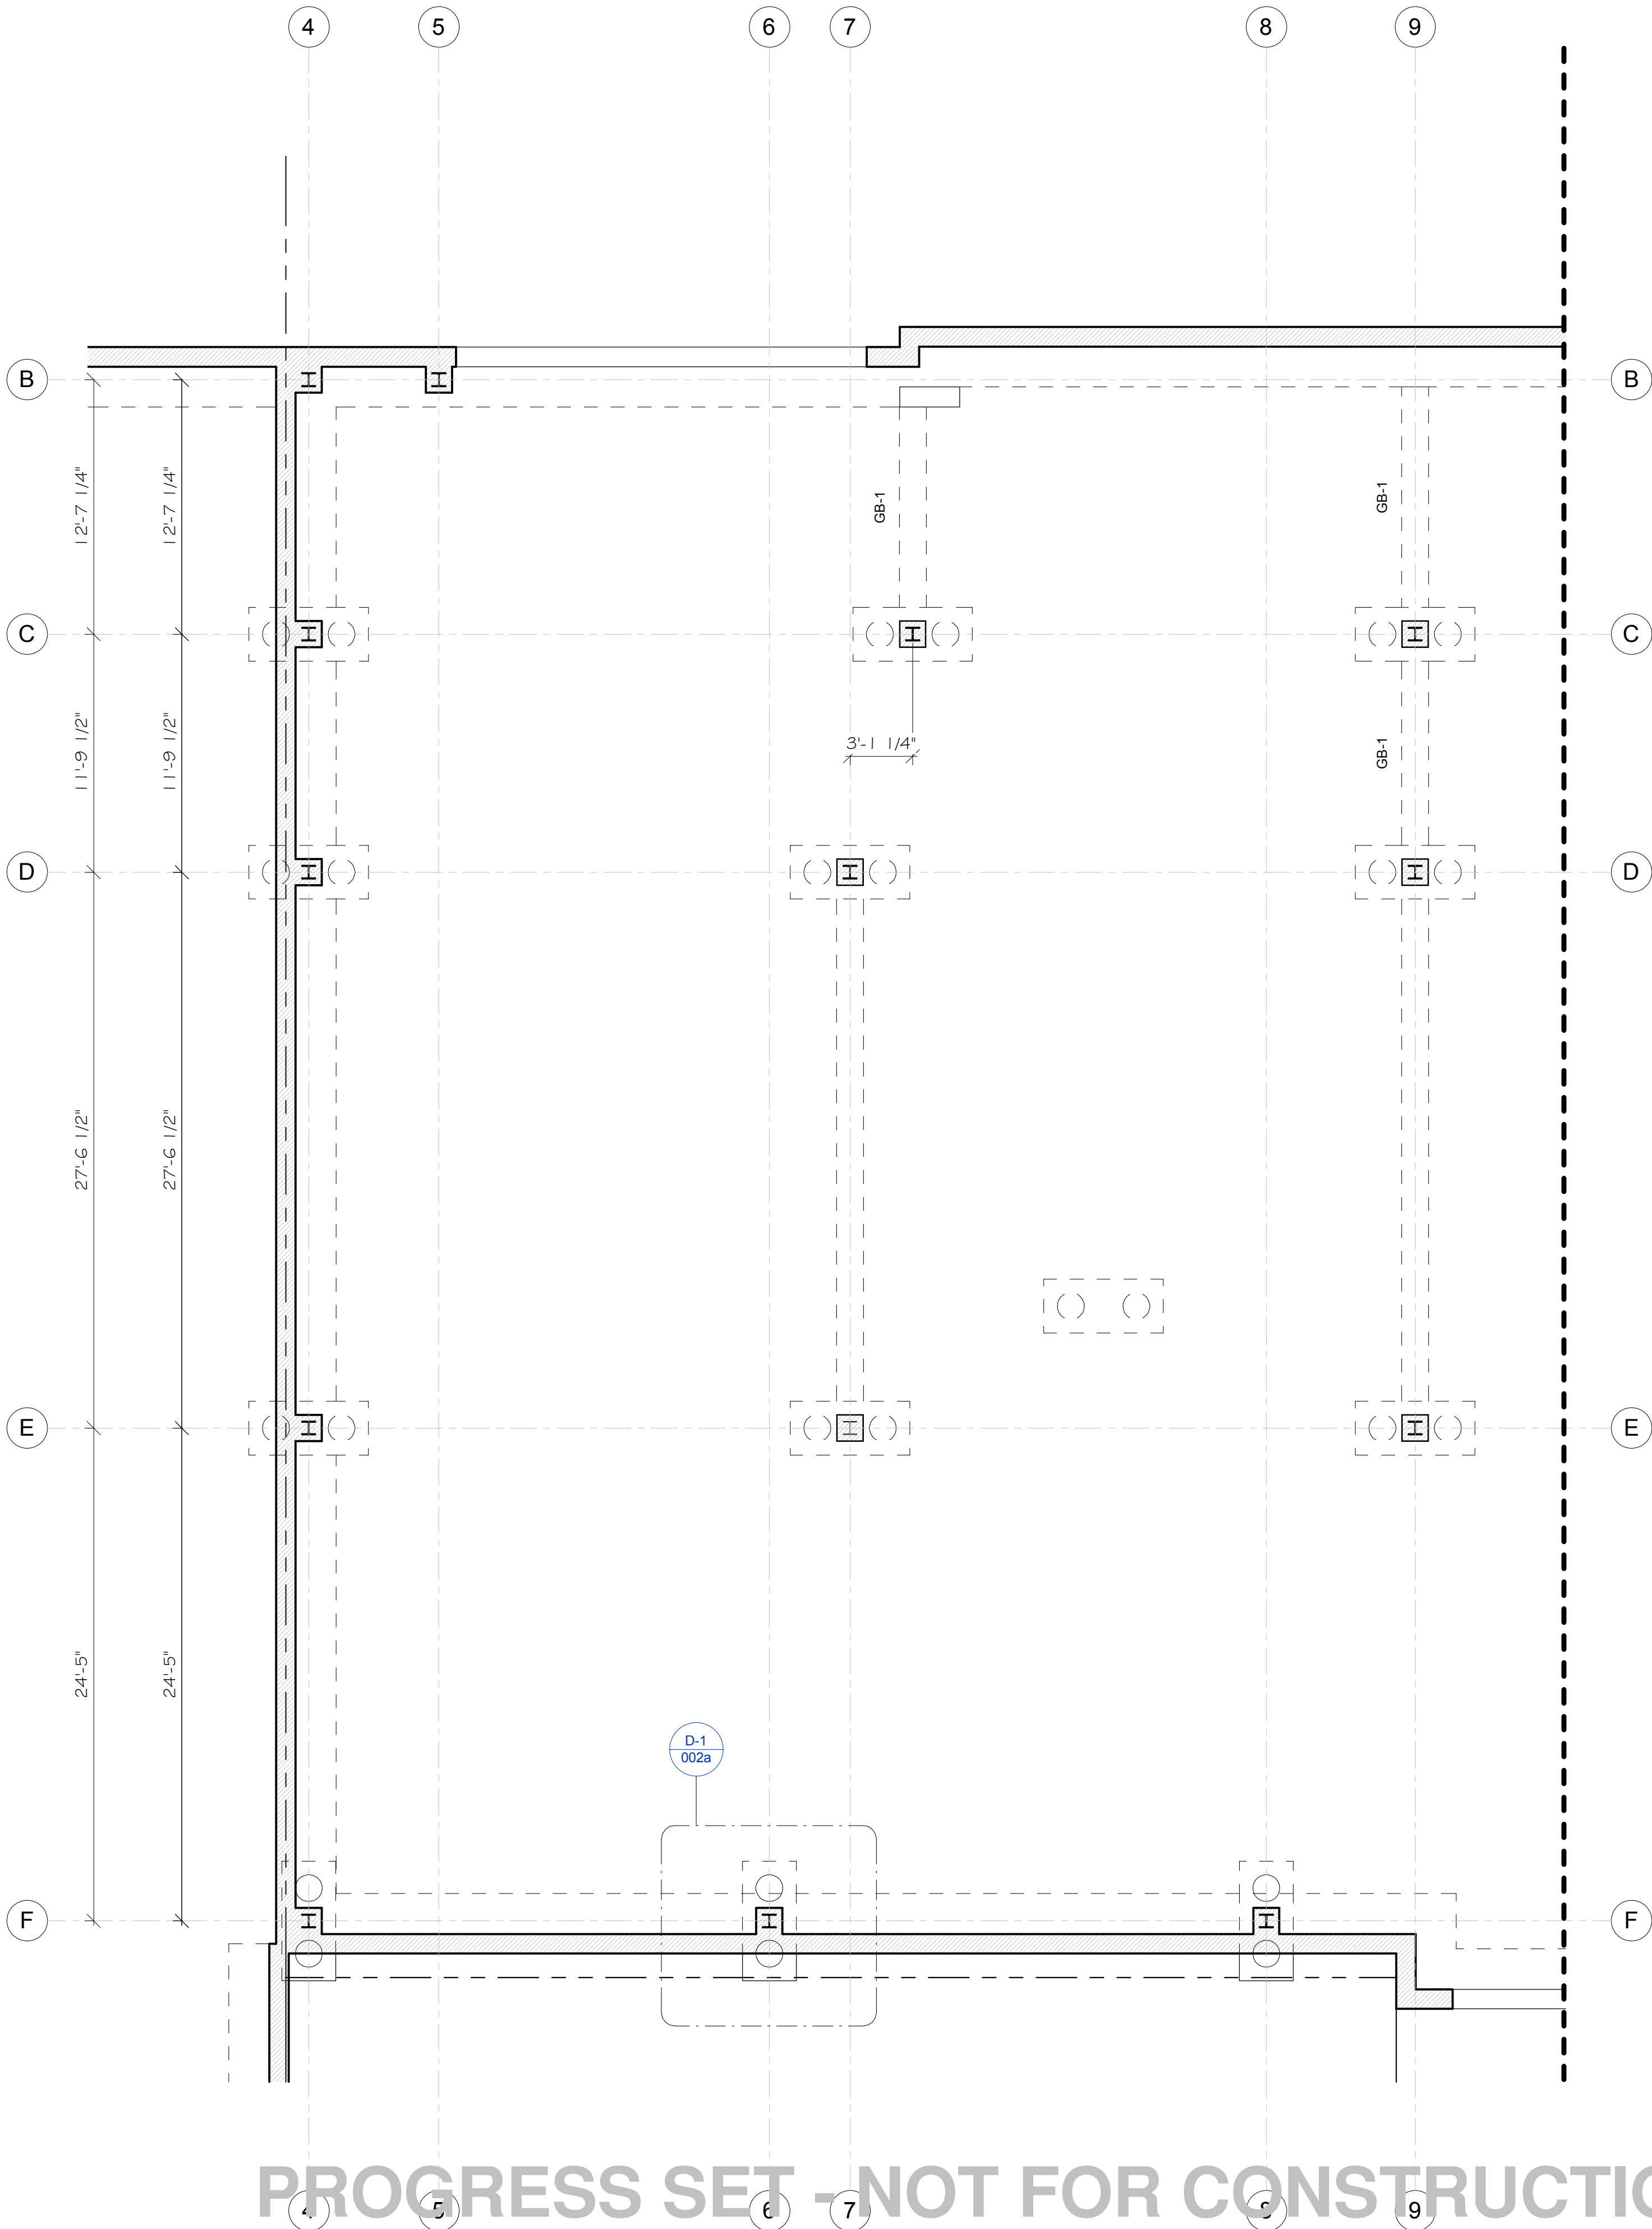

Copyright © 2015 Rizwan A. Salam PE Consulting Engineers (RAS) - This drawing is an instrument of service and the sole property of the RAS or the Applicant of Record (AoR). Any use of this drawing without the consent of RAS is prohibited. Drawing scales as indicated are for reference only and are not intended to accurately depict actual or designed conditions. Written dimensions shall govern.

CONTRACTOR SHALL VERIFY ALL FIELD CONDITIONS AND DIMENSIONS AND BE RESPONSIBLE FOR FIELD FIT AND QUALITY OF WORK. NO ALLOWANCES SHALL BE MADE IN BEHALF OF THE CONTRACTOR FOR ANY ERROR OR NEGLIGENCE ON HIS PART.

Client:

Tel: ---


Email:---

Contractor:

Cristom Construction Services
151-01 14th Avenue
Whitestone NY 11357

Tel: (718) 747-4747

Email: info@cristomconstruction.com

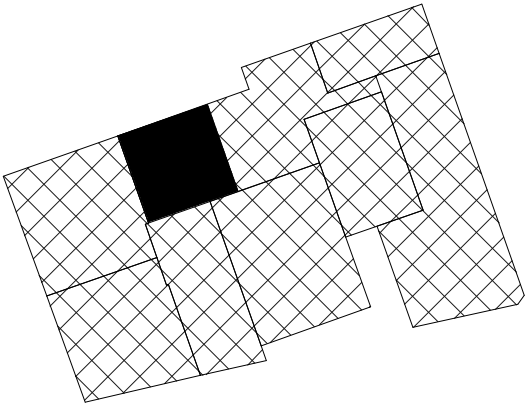

APPLICANT OF RECORD:



20 E 49TH ST. SUITE-3A
NEW YORK NY 10017

Tel: (212) 377-2456

Email: info@salamcons.com

1/19/2017 5:14:42 PM

PLOT TIME/DATE

Date	Issue No.	Rev.	Description

SCOPE OF WORK

**ALT II STRUCTURAL RENOVATION
OF EXISTING ONE STORY
WAREHOUSE STRUCTURE**

ADDRESS

**537-561 Johnson Avenue
Brooklyn NY 11237**

BLOCK: 2988

MAP #: 13b


LOT: 01, 49, 14

ZONING:M3-1

SHEET TITLE

**Partial Existing Foundation Plan
and Slab Layout @ 561 Johnson
Avenue (1 of 3)**

SEAL & SIGNATURE

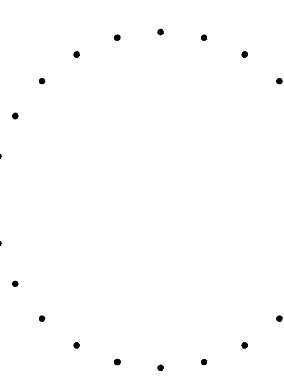

DATE: 7/28/2016

PROJECT NO.: 151002

DRAWING BY: HSK

CHK BY: RAS

DWG NO.:

S-002a.00

File Directory:
2-2017-151 Johnson Avenue Brooklyn
NY Drawing Folder\Drawings\001017
Drawing Number: 01

3 OF 5

Orient and affix BIS
job number label here



PROGRESS SET - NOT FOR CONSTRUCTION




Partial Foundation Plan and Slab Layout (2 of 3):

Scale: 3/16" = 1'-0"


NOTES:

1. TOP OF CONC. SLAB ELEVATION (T/S/L) IS SHOWN THUS [+/-] ON PLAN.
2. SLAB TO BE A 6" THICK SLAB ON GRADE, REINFORCED W6x6 - W2.9xW2.9 WWF ON VAPOR BARRIER.
3. EL. TO B.O. FOOTINGS ARE DENOTED THUS (+/-) ON PLAN RELATIVE TO BASEPLANE
4. ALL FOOTINGS SHALL BEAR ON SOIL WITH A MINIMUM 2.5 TON/SQ. FT. CAPACITY
5. WALL BUTTRESSES ARE TYPE WB-1 UNLESS OTHERWISE NOTED
6. BOTTOM ELEVATION OF SPREAD FOOTING TO BE (-2'-2") FROM TOP OF SLAB, UNLESS OTHERWISE NOTED
7. TIE (OR STRAP) BEAMS ARE TO BE 2'-0" DEEP WITH TOP AND BOTTOM REINFORCEMENT 3 - (#6) EXTENDED A MINIMUM OF 3'-0" INTO THE FOOTINGS. STIRRUPS ARE TO BE #3 BARS @ 10" O.C. THE TIE BEAMS ARE THUS DENOTED ON PLANS (TB-1)
8. FOR FOOTING, BUTTRESS, AND WALL REINFORCEMENT SEE SCHEDULES AND DETAILS SHOWN ON THIS DRAWING AND SECTION DETAILS.
9. SEE DRAWINGS 5-001 FOR GENERAL NOTES, LIST OF ABBREVIATIONS AND LEGEND
10. CONTRACTOR SHALL CONDUCT PRECONSTRUCTION SURVEY OF ADJACENT EXISTING BUILDINGS BEFORE EXCAVATION, UNDERPINNING OR STIFF SHEETING AS REQUIRED.

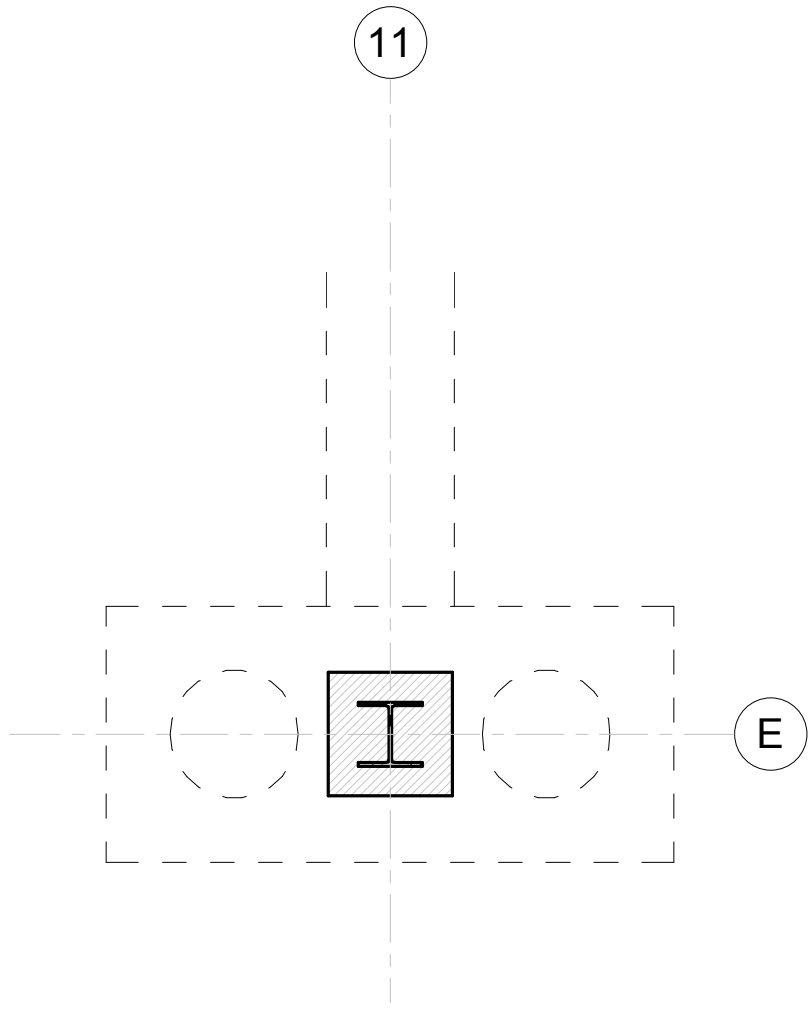

Detail 2 Proposed Pilecap Retrofit Detail:

Scale: 1/2" = 1'-0"

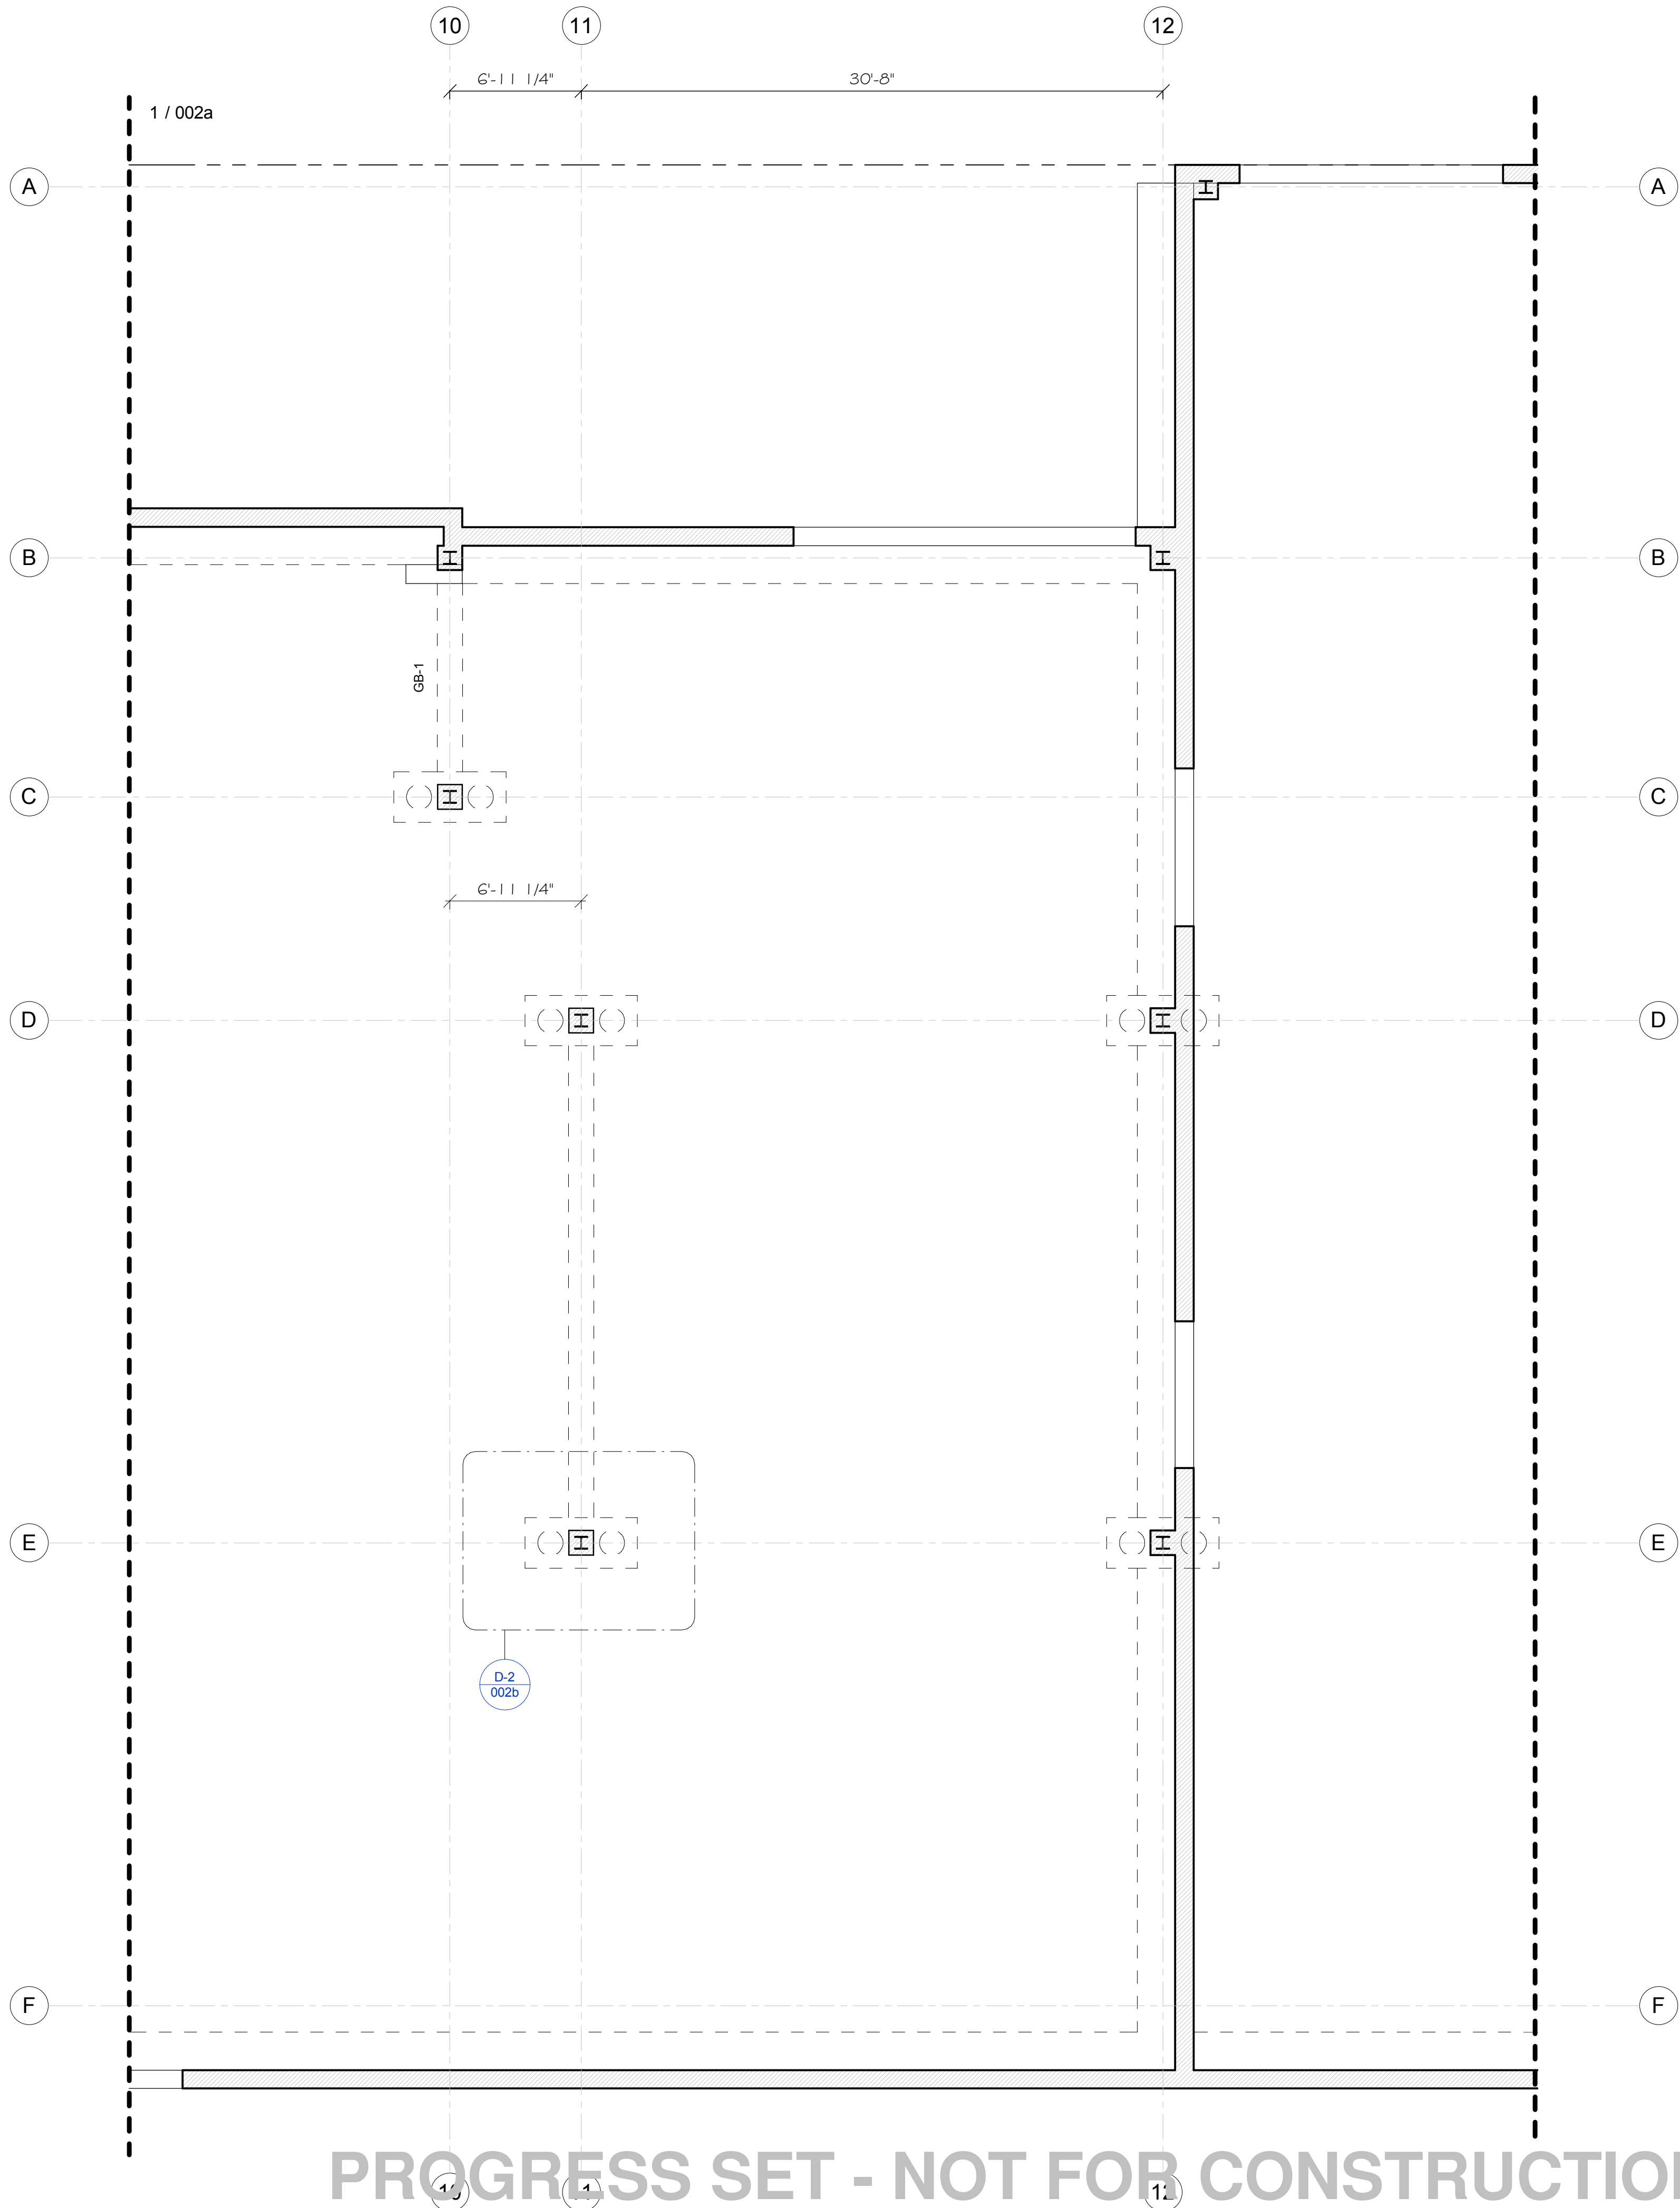

PROGRESS SET - NOT FOR CONSTRUCTION

Copyright © 2015 Rizwan A. Salam PE Consulting Engineers (RAS) - This drawing is an instrument of service and the sole property of the RAS or the Applicant of Record (AoR). Any use of this drawing without the consent of RAS is prohibited.
Drawing scales as indicated are for reference only and are not intended to accurately depict actual or designed conditions. Written dimensions shall govern.

CONTRACTOR SHALL VERIFY ALL FIELD CONDITIONS AND DIMENSIONS AND BE RESPONSIBLE FOR FIELD FIT AND QUALITY OF WORK. NO ALLOWANCES SHALL BE MADE IN BEHALF OF THE CONTRACTOR FOR ANY ERROR OR NEGLIGENCE ON HIS PART.

Client:

Tel: ---

Email:---


Contractor:

Cristom Construction Services

151-01 14th Avenue
Whitestone NY 11357

Tel: (718) 747-4747

Email: info@cristomconstruction.com

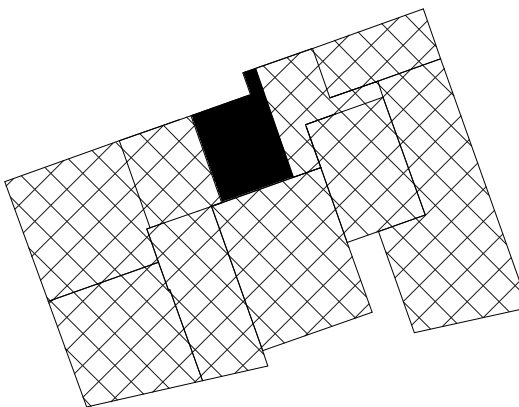

APPLICANT OF RECORD:



20 E 49TH ST. SUITE-3A
NEW YORK NY 10017

Tel: (212) 377-2456

Email: info@salamcons.com

1/19/2017 5:14:42 PM

PLOT TIME/DATE

Date	Issue No.	Rev.	Description

SCOPE OF WORK

**ALT II STRUCTURAL RENOVATION
OF EXISTING ONE STORY
WAREHOUSE STRUCTURE**

ADDRESS

**537-561 Johnson Avenue
Brooklyn NY 11237**

BLOCK: 2988

MAP #: 13b

LOT: 01, 49, 14

ZONING:M3-1

SHEET TITLE

**Partial Existing Foundation Plan
and Slab Layout @ 561 Johnson
Avenue (2 of 3)**

SEAL & SIGNATURE



DATE: 7/28/2016

PROJECT NO.: 151002

DRAWING BY: HSK

CHK BY: RAS

DWG NO.:

S-002b.00

File Directory:

20170728 537-561 Johnson Avenue

NY Drawing Folder\Drawings\001

001\002b.dwg

4 OF 5



Orient and affix BIS

job number label here



PROGRESS SET - NOT FOR CONSTRUCTION




Partial Foundation Plan and Slab Layout (3 of 3):

Scale: 3/16" = 1'-0"


NOTES:

1. TOP OF CONC. SLAB ELEVATION (T/S/L) IS SHOWN THUS [+/-] ON PLAN.
2. SLAB TO BE A 6" THICK SLAB ON GRADE, REINFORCED W6x6 - W2.9xW2.9 WWF ON VAPOR BARRIER
3. EL. TO B.O. FOOTINGS ARE DENOTED THUS (+/-) ON PLAN RELATIVE TO BASEPLANE
4. ALL FOOTINGS SHALL BEAR ON SOIL WITH A MINIMUM 2.5 TON/SQ. FT. CAPACITY
5. WALL BUTTRESSES ARE TYPE WB1 UNLESS OTHERWISE NOTED
6. BOTTOM ELEVATION OF SPREAD FOOTING TO BE (-2'-2") FROM TOP OF SLAB, UNLESS OTHERWISE NOTED
7. TIE (OR STRAP) BEAMS ARE TO BE 2'-0" DEEP WITH TOP AND BOTTOM REINFORCEMENT 3 - (#6) EXTENDED A MINIMUM OF 3'-0" INTO THE FOOTINGS. STIRRUPS ARE TO BE #3 BARS @ 10" O.C. THE TIE BEAMS ARE THUS DENOTED ON PLANS (TB-1)
8. FOR FOOTING, BUTTRESS, AND WALL REINFORCEMENT SEE SCHEDULES AND DETAILS SHOWN ON THIS DRAWING AND SECTION DETAILS.
9. SEE DRAWINGS 5-001 FOR GENERAL NOTES, LIST OF ABBREVIATIONS AND LEGEND
10. CONTRACTOR SHALL CONDUCT PRECONSTRUCTION SURVEY OF ADJACENT EXISTING BUILDINGS BEFORE EXCAVATION, UNDERPINNING OR STIFF SHEETING AS REQUIRED.

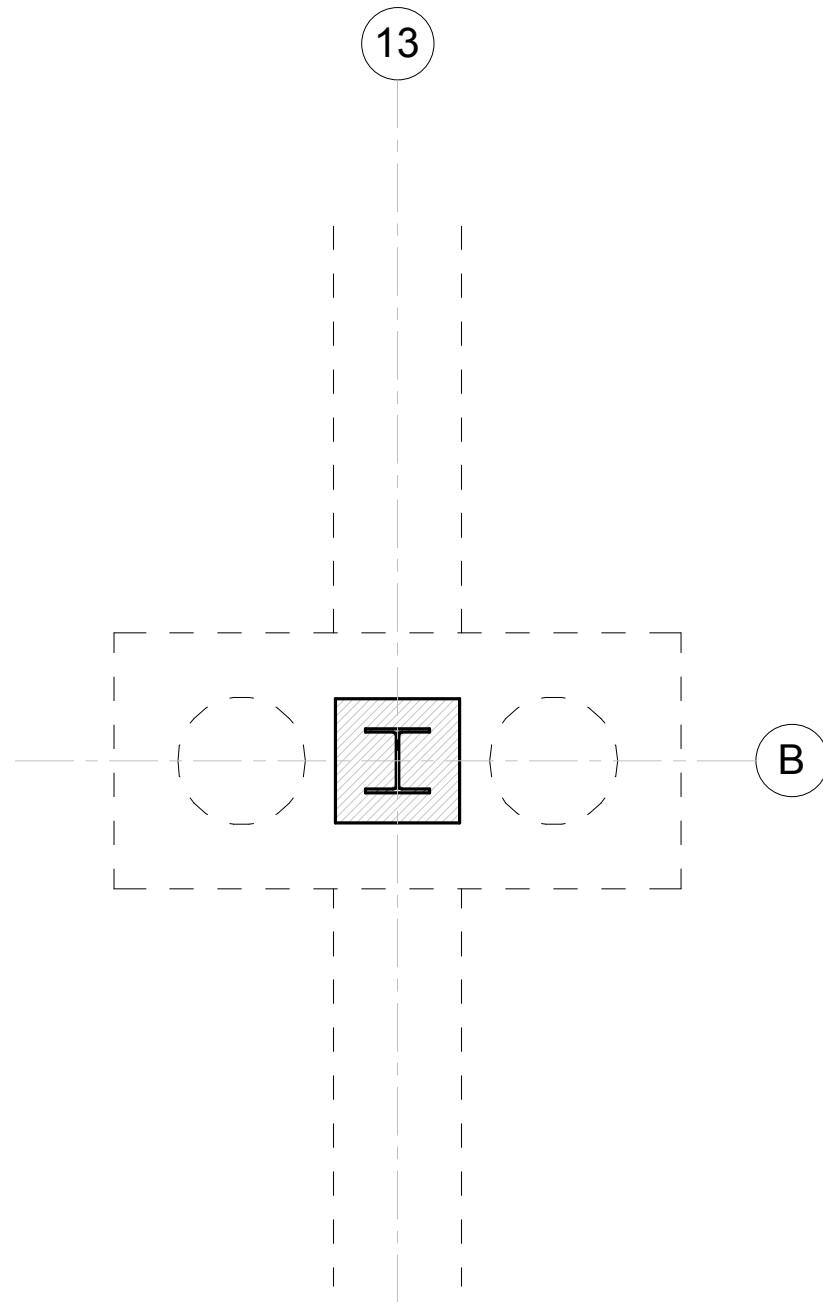

Detail 3 Proposed Pilecap Retrofit Detail:

Scale: 1/2" = 1'-0"

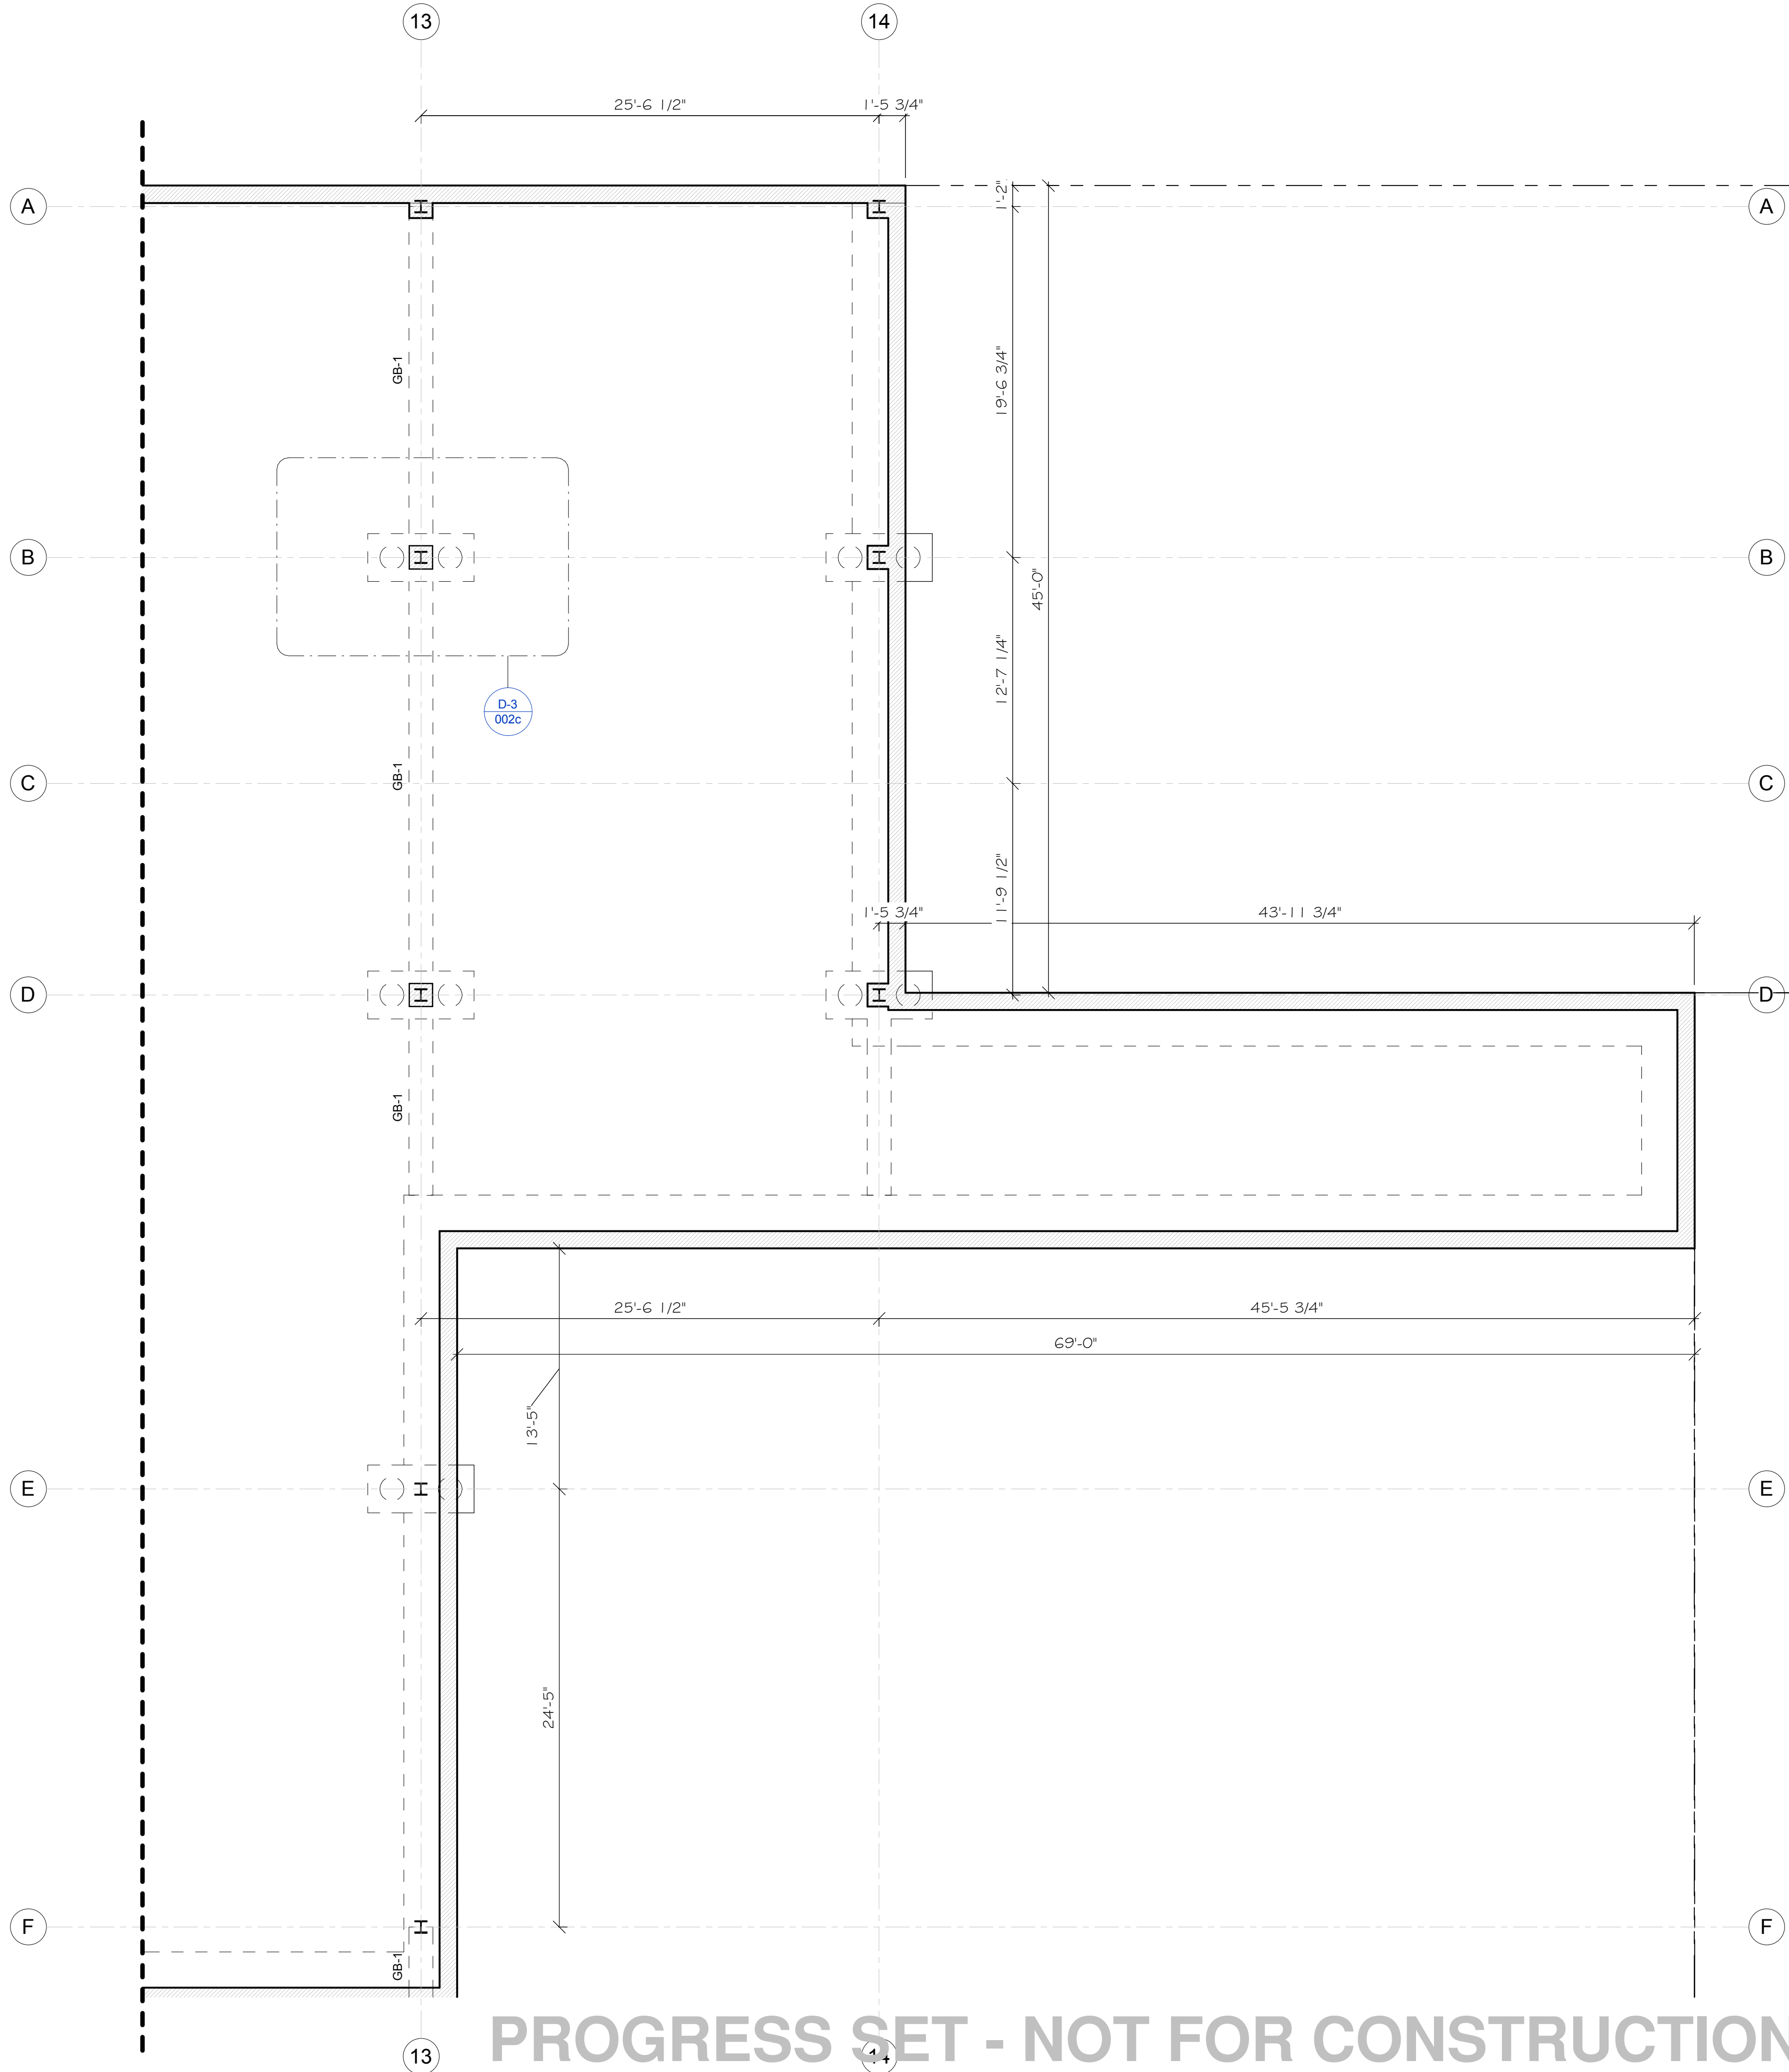

PROGRESS SET - NOT FOR CONSTRUCTION

Copyright © 2015 Rizwan A. Salam PE Consulting Engineers (RAS) - This drawing is an instrument of service and the sole property of the RAS or the Applicant of Record (AoR). Any use of this drawing without the consent of RAS is prohibited.
Drawing scales as indicated are for reference only and are not intended to accurately depict actual or designed conditions. Written dimensions shall govern.

CONTRACTOR SHALL VERIFY ALL FIELD CONDITIONS AND DIMENSIONS AND BE RESPONSIBLE FOR FIELD FIT AND QUALITY OF WORK. NO ALLOWANCES SHALL BE MADE IN BEHALF OF THE CONTRACTOR FOR ANY ERROR OR NEGLIGENCE ON HIS PART.

Client:

Tel: ---

Email:---


Contractor:

Cristom Construction Services

151-01 14th Avenue
Whitestone NY 11357

Tel: (718) 747-4747

Email: info@cristomconstruction.com

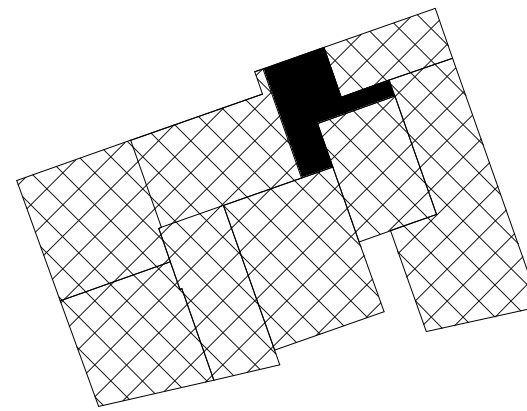

APPLICANT OF RECORD:



20 E 49TH ST. SUITE-3A
NEW YORK NY 10017

Tel: (212) 377-2456

Email: info@salamcons.com

1/19/2017 5:14:42 PM

PLOT TIME/DATE

Date	Issue No.	Rev.	Description

SCOPE OF WORK

**ALT II STRUCTURAL RENOVATION
OF EXISTING ONE STORY
WAREHOUSE STRUCTURE**

ADDRESS

**537-561 Johnson Avenue
Brooklyn NY 11237**

BLOCK: 2988

MAP #: 13b


LOT: 01, 49, 14

ZONING:M3-1

SHEET TITLE

**Partial Existing Foundation Plan
and Slab Layout @ 561 Johnson
Avenue (3 of 3)**

SEAL & SIGNATURE

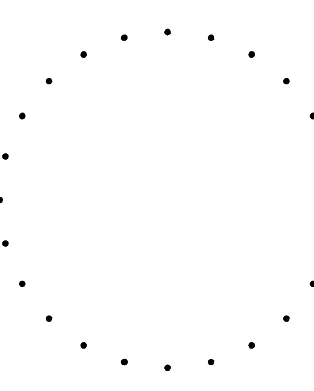

DATE: 7/28/2016

PROJECT NO.: 151002

DRAWING BY: HSK

CHK BY: RAS

DWG NO.:


S-002c.00

File Directory:
2-28-2017 5:14:42 PM
NY State Engineering Board
NY State Engineering Board
NY State Engineering Board

5 OF 5

Orient and affix BIS
job number label here

PROGRESS SET - NOT FOR CONSTRUCTION

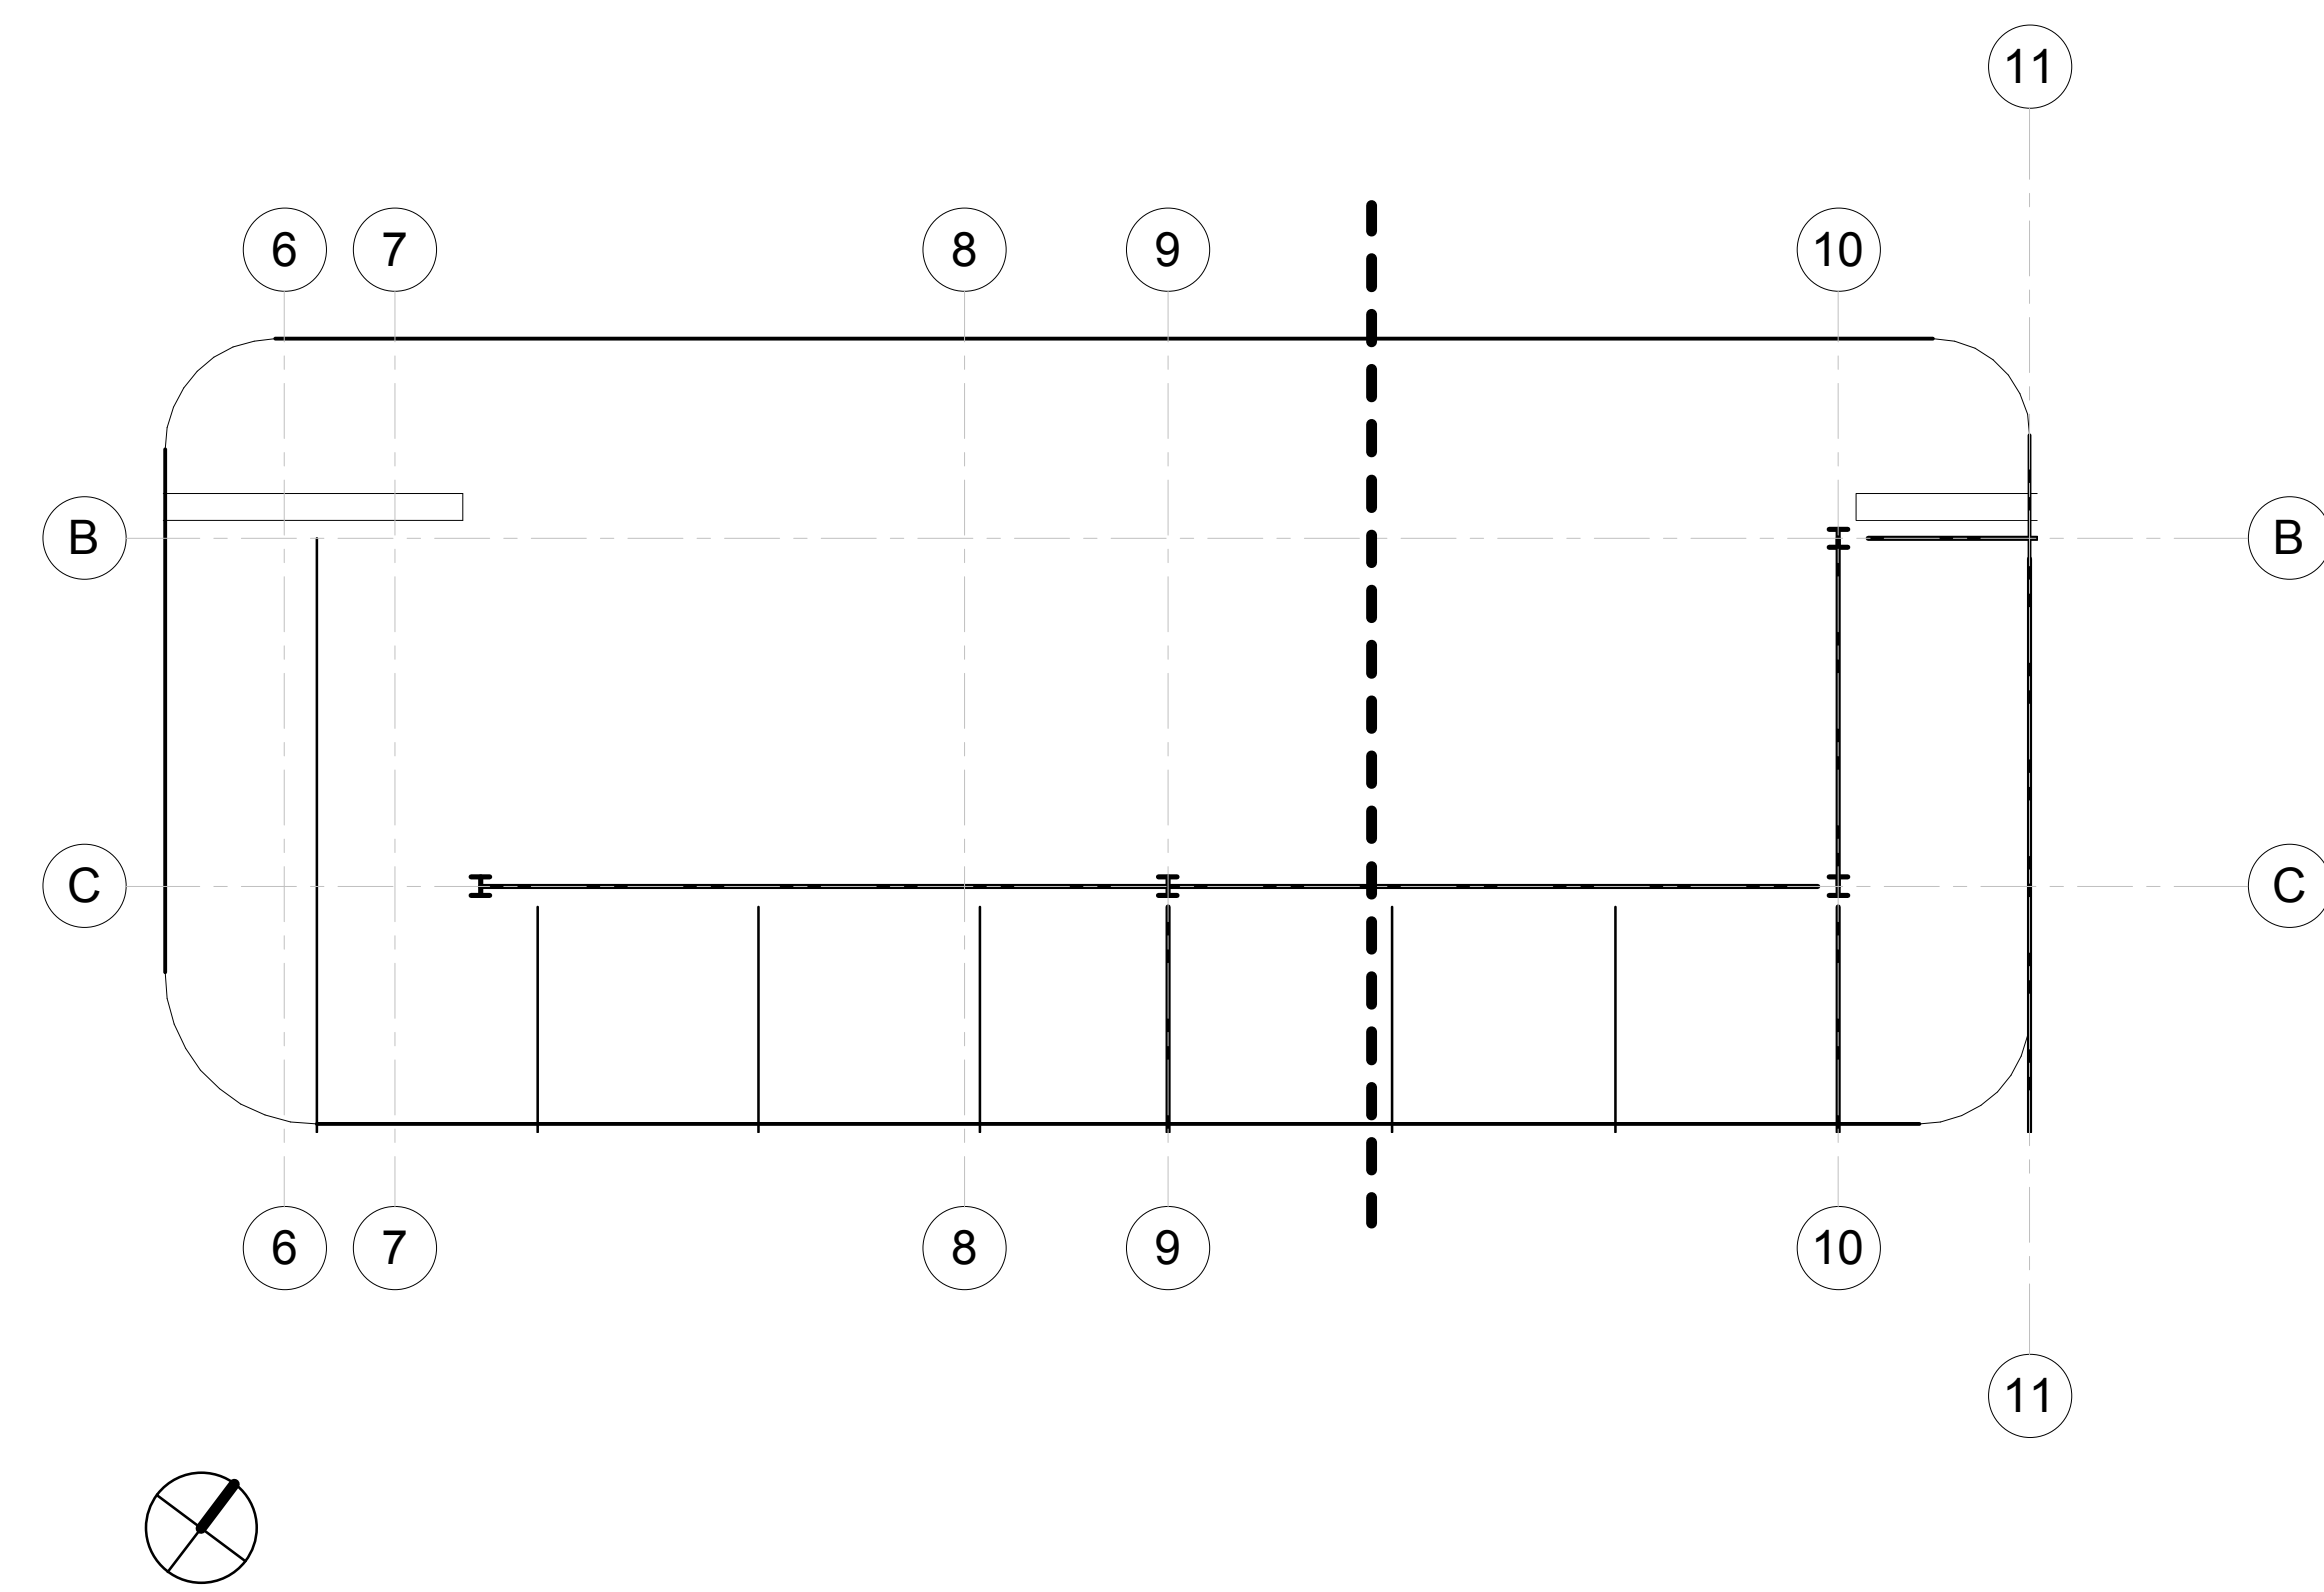

1/19/2017 5:16:23 PM	PLOT TIME/DATE	
Date	Issue No.	Rev. Description

SEAL & SIGNATURE	DATE:	7/28/2016
	PROJECT NO.:	151002
	DRAWING BY:	HSK
	CHK BY:	RAS
	DWG NO.:	S-003.00
	File Directory:	6 OF 5

 Orient and affix BIS
job number label here

PROGRESS SET - NOT FOR CONSTRUCTION

PROGRESS SET - NOT FOR CONSTRUCTION

Copyright © 2015 Rizwan A. Salam PE Consulting Engineers (RAS) - This drawing is an instrument of service and the sole property of the RAS or the Applicant of Record (AoR). Any use of this drawing without the consent of RAS is prohibited.
Drawing scales as indicated are for reference only and are not intended to accurately depict actual or designed conditions. Written dimensions shall govern.
CONTRACTOR SHALL VERIFY ALL FIELD CONDITIONS AND DIMENSIONS AND BE RESPONSIBLE FOR FIELD FIT AND QUALITY OF WORK. NO ALLOWANCES SHALL BE MADE IN BEHALF OF THE CONTRACTOR FOR ANY ERROR OR NEGLIGENCE ON HIS PART.

Client:

--
--
Tel: --- Email:---

Contractor:
Cristom Construction Services
151-01 14th Avenue
Whitestone NY 11357
Tel: (718) 747-4747 Email: info@cristomconstruction.com


APPLICANT OF RECORD:
**RAS P.E.**
CONSULTING ENGINEERS
RIZWAN A. SALAM, P.E.
20 E 49TH ST. SUITE-3A
NEW YORK NY 10017
Tel: (212) 377-2456 Email: info@salamcons.com

1/19/2017 5:14:43 PM		PLOT TIME/DATE
Date	Issue No.	Rev. Description

SCOPE OF WORK
**ALT II STRUCTURAL RENOVATION
OF EXISTING ONE STORY
WAREHOUSE STRUCTURE**

ADDRESS
**537-561 Johnson Avenue
Brooklyn NY 11237**
BLOCK: 2988 MAP #: 13b
LOT: 01, 49, 14 ZONING:M3-1

SHEET TITLE
**Proposed Structural Retrofit
Details**

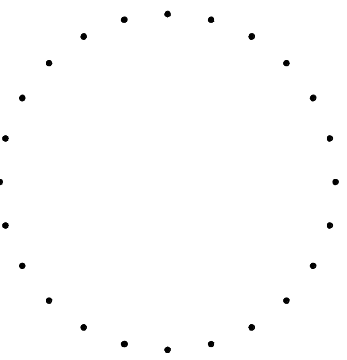	DATE: 7/28/2016
	PROJECT NO.: 151002
	DRAWING BY: HSK
	CHK BY: RAS
	DWG NO.: S-004.00
File Directory: 2:201515 Johnson Avenue Brooklyn NY Warehouse Renovation Mod0017 Drawing Number: 01	

7 OF 5

☒ Orient and affix BIS
job number label here ☒

PROGRESS SET - NOT FOR CONSTRUCTION



NOTES:

1. TOP OF CONC. SLAB ELEVATION (T/SU) IS SHOWN THUS (+/-) ON PLAN.
2. SLAB TO BE A 6" THICK SLAB ON GRADE, REINFORCED W/6X6 - W2.9XW2.9 WWF ON VAPOR BARRIER
3. EL. TO B.O. FOOTINGS ARE DENOTED THUS (+/-) ON PLAN RELATIVE TO BASEPLANE
4. ALL FOOTINGS SHALL BEAR ON SOIL WITH A MINIMUM 2.5 TON/SQ. FT. CAPACITY
5. WALL BUTTRESSES ARE TYPE WB1 UNLESS OTHERWISE NOTED
6. BOTTOM ELEVATION OF SPREAD FOOTING TO BE (-2'-2") FROM TOP OF SLAB, UNLESS OTHERWISE NOTED
7. TIE (OR STRAP) BEAMS ARE TO BE 2'-0" DEEP WITH TOP AND BOTTOM REINFORCEMENT 3 - (#6) EXTENDED A MINIMUM OF 3'-0" INTO THE FOOTINGS. STIRRUPS ARE TO BE #3 BARS @ 10" O.C. THE TIE BEAMS ARE THUS DENOTED ON PLANS (TB-1)
8. FOR FOOTING, BUTTRESS, AND WALL REINFORCEMENT SEE SCHEDULES AND DETAILS SHOWN ON THIS DRAWING AND SECTION DETAILS.
9. SEE DRAWINGS 5-001 FOR GENERAL NOTES, LIST OF ABBREVIATIONS AND LEGEND
10. CONTRACTOR SHALL CONDUCT PRECONSTRUCTION SURVEY OF ADJACENT EXISTING BUILDINGS BEFORE EXCAVATION. UNDERPINNING OR STIFF SHEETING AS REQUIRED.

CONTRACTOR SHALL VERIFY ALL FIELD CONDITIONS AND DIMENSIONS AND BE RESPONSIBLE FOR FIELD FIT AND QUALITY OF WORK. NO ALLOWANCES SHALL BE MADE IN BEHALF OF THE CONTRACTOR FOR ANY ERROR OR NEGLIGENCE ON HIS PART.

Tel: ---


Contractor:

Cristom Construction Services

151-01 14th Avenue
Whitestone NY 11357

Tel: (718) 747-4747

Tel: (718) 747-4747 Email: info@crustomconstruction.com

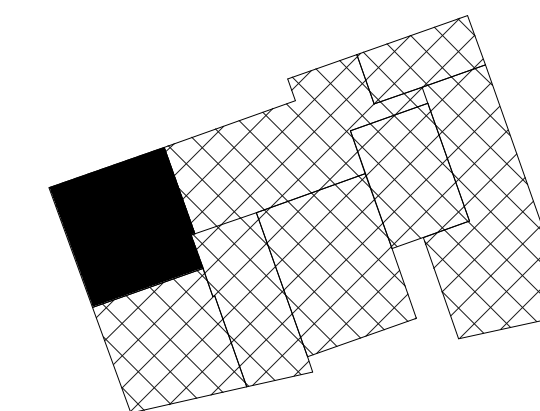

APPLICANT OF RECORD:



RAS P.E.
CONSULTING ENGINEERS
RIZWAN A. SALAM, P.E.

20 E 49TH ST. SUITE-3A
NEW YORK NY 10017

Tel: (212) 377-2456

Email: info@salamcons.com

1/19/2017 5:14:43 PM

PLOT TIME/DATE

Date	Issue No.	Rev. Description

SCOPE OF WORK

ALT II STRUCTURAL RENOVATION OF EXISTING ONE STORY WAREHOUSE STRUCTURE

ADDRESS

**537-561 Johnson Avenue
Brooklyn NY 11237**

BLOCK: 2988

LOT: 01, 49, 14

MAP #: 13b

ZONING:M3-1

SHEET TITLE

**Existing Foundation Plan and
Slab Layout @ 537 Johnson
Avenue (1 of 2)**

SEAL & SIGNATURE

DATE: 7/28/2016

PROJECT NO.:	151002
--------------	--------

DRAWING BY: HSK


CHK BY: RAS

DWG NO.:


S-006.00

File Directory:
J:\2014\537 Johnson Aronson Etc
NY Drawings Folder\Revit Mod
Johnson Aronson.rvt

8 QF.5

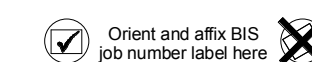

PROGRESS SET - NOT FOR CONSTRUCTION

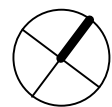

Scale: 1/8" = 1'-0"

- NOTES:**
1. TOP OF CONC. SLAB ELEVATION (7/5L) IS SHOWN THUS (+/-) ON PLAN.
 2. SLAB TO BE A 6" THICK SLAB ON GRADE, REINFORCED W/6x6 - W/2.9xW2.9 W/W/F ON VAPOR BARRIER
 3. EL. TO B.O. FOOTINGS ARE DENOTED THUS (+/-) ON PLAN RELATIVE TO BASEPLANE
 4. ALL FOOTINGS SHALL BEAR ON SOIL WITH A MINIMUM 2.5 TON/SQ. FT. CAPACITY
 5. WALL BUTTRESSES ARE TYPE WB1 UNLESS OTHERWISE NOTED
 6. BOTTOM ELEVATION OF SPREAD FOOTING TO BE (-2'-2") FROM TOP OF SLAB, UNLESS OTHERWISE NOTED
 7. TIE (OR STRAP) BEAMS ARE TO BE 2'-0" DEEP WITH TOP AND BOTTOM REINFORCEMENT 3 - (#6) EXTENDED A MINIMUM OF 3'-0" INTO THE FOOTINGS. STIRRUPS ARE TO BE #3 BARS @ 10" O.C. THE TIE BEAMS ARE THUS DENOTED ON PLANS (TB-1)
 8. FOR FOOTING, BUTTRESS, AND WALL REINFORCEMENT SEE SCHEDULES AND DETAILS SHOWN ON THIS DRAWING AND SECTION DETAILS.
 9. SEE DRAWINGS 5-001 FOR GENERAL NOTES, LIST OF ABBREVIATIONS AND LEGEND
 10. CONTRACTOR SHALL CONDUCT PRECONSTRUCTION SURVEY OF ADJACENT EXISTING BUILDINGS BEFORE EXCAVATION. UNDERPINNING OR STIFF SHEETING AS REQUIRED.

CONTRACTOR SHALL VERIFY ALL FIELD CONDITIONS AND DIMENSIONS AND BE RESPONSIBLE FOR FIELD FIT AND QUALITY OF WORK. NO ALLOWANCES SHALL BE MADE IN BEHALF OF THE CONTRACTOR FOR ANY ERROR OR NEGLIGENCE ON HIS PART.


Figure 1

Email:---

Cristom Construction Services

Tel: (718) 747-4747

Email: info@crisomconstruction.com

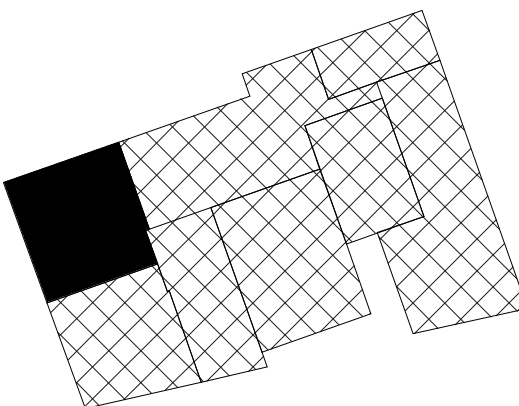

APPLICANT OF RECORD:



20 E 49TH ST. SUITE-3A
NEW YORK NY 10017

Tel: (212) 377-2456

Email: info@salamcons.com

1/19/2017 5:14:44 PM		PLOT TIME/DATE
Date	Issue No.	Rev. Description

SCOPE OF WORK

ALT II STRUCTURAL RENOVATION OF EXISTING ONE STORY WAREHOUSE STRUCTURE

ADDRESS

**537-561 Johnson Avenue
Brooklyn NY 11237**

BLOCK: 2988

MAP #: 13b

LOT: 01, 49, 14

ZONING:M3.

SHEET TITLE

Proposed Foundation Plan and Slab Layout @ 537 Johnson Avenue (1 of 2)

SEAL & SIGNATURE

DATE: 7/28/2016

PROJECT NO.: 151002

DRAWING BY: HSE

CHK BY: RA5

DWG NO.:

S-008.00

File Directory:
E:\2016\537 Johnson Axiom Draw
NY Drawings Folder\Revit Model
Johnson Axiom.rvt

10 OF 5



Orient and affix BIS
job number label box



